

Issue:	Date:	By:
SCHEMATIC DESIGN	01.07.26	BAC
DESIGN DEVELOPMENT	03.05.26	BAC

whs
engineering

2012 West 25th Street, Suite 900
Cleveland, OH 44113
Phone: 216 227 8505

**OSU
AIRPORT WEST
BUILDING C**

**3455 W. Dublin Granville Rd,
Columbus OH, 43235**


BUILDING C SITE ELECTRICAL PLAN

Date	Project Number
03.05.2026	24-065
Drawn by	Drawing Number
DJS	
Checked by	
KDS	ES.01C
Approved	
GSS	

Seal

**NOT FOR
CONSTRUCTION**

Issue:	Date:	By:
SCHEMATIC DESIGN	01.07.26	BA
DESIGN DEVELOPMENT	03.05.26	BA

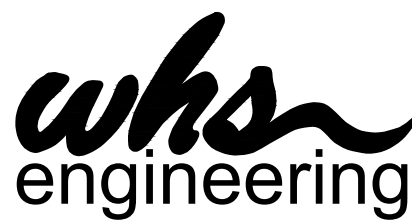This image shows a vertical rectangular sheet of white paper with horizontal blue or grey ruling lines. The lines are evenly spaced and run across the width of the page. There are approximately 20 lines visible. On the left side, there is a narrow margin where the lines do not reach the edge. The paper appears to be a standard notebook page or a sheet of stationery.

2012 West 25th Street, Suite 900
Cleveland, OH 44113
Phone: 216 227 8505

**OSU
AIRPORT WEST
BUILDING C**

**3455 W. Dublin Granville Rd,
Columbus OH, 43235**

Drawing Title


**BUILDING C SITE
ELECTRICAL DETAILS**

Date	Project Number
03.05.2026	24-065
Drawn by	Drawing Number
DJS	
Checked by	
KDS	ES.020
Approved	
GSS	

-

-

LUMINAIRE SCHEDULE						
TYPE	LAMP	WATTAGE	VOLTAGE	DIMMING TYPE	DESCRIPTION	EQUIVALENT MANUFACTURER/REMARKS
D-1			120		LED DOWNLIGHT USED IN CLUBROOM.	
D-1A			120		LED DOWNLIGHT USED IN FIRST FLOOR CORRIDOR.	
D-2			120		LED DOWNLIGHT USED THROUGHOUT THE BUILDINGS.	
D-4			120		LED DOWNLIGHT USED IN CLUBROOM.	
D-5			120		LED DOWNLIGHT USED IN OUTDOOR CORRIDOR.	
D-6			120		LED DOWNLIGHT USED IN CORRIDORS.	
ESC-2			120		LED EXTERIOR LIGHT.	
S-2			120		LED STRING LIGHT USED IN CLUBROOM.	
S-3			120		LED SQUARE LIGHT USED IN CORRIDOR.	
S-4			120		LED LIGHT USED IN PUBLIC BATHROOMS.	
P-1			120		LED SPHERE LIGHT USED IN CLUBROOM AND LOBBY AREA.	
P-6			120		LED STRIP LIGHT USED IN FITNESS AREA.	
P-7			120		LED STRIP LIGHT USED IN FITNESS AREA.	
P-8			120		LED STRING LIGHT USED ABOVE FITNESS AREA.	
SM-2			120		LED FIXTURE USED IN OFFICES.	
SM-3			120		LED FIXTURE USED IN PUBLIC BATHROOMS.	
U-1			120		LED STRIP LIGHT USED IN HOUSE AREAS.	
U-2			120		LED STRIP LIGHT USED IN STAIRWAYS, WITH ON-FIXTURE MOTION SENSOR.	
WS-1			120		LED SQUARE LIGHT USED IN CORRIDORS.	
X1						
X2						
X3						
LUMINAIRE SCHEDULE GENERAL NOTES:						
1. VERIFY ALL LUMINAIRE COLORS, TRIMS, LENGTHS, ETC. WITH THE ARCHITECT/OWNER/DEVELOPER/DESIGNER PRIOR TO PLACING FINAL PURCHASE ORDERS. SUBMISSION OF SHOP DRAWINGS WILL BE INTERPRETED AS HAVING BEEN COORDINATED WITH THE AFOREMENTIONED PARTIES.						
2. PROVIDE ALL LENGTHS, FEEDS, ACCESSORIES, CONNECTORS, WIRING, POWER SUPPLIES, DRIVERS, ETC. FOR A COMPLETE INSTALLATION. VERIFY THE COMPLETE BILL OF MATERIAL WITH MANUFACTURER'S REPRESENTATIVE AND ENSURE ALL EQUIPMENT IS INCLUDED IN BID PRICE. COORDINATE INSTALLATION WITH ARCHITECTURAL DETAILS.						
3. VERIFY FINAL LUMINAIRE LOCATIONS WITH OTHER CEILING MOUNTED EQUIPMENT SUCH AS DIFFUSERS, FIRE ALARM DEVICES, SPEAKERS, ETC., WITH ARCHITECTURAL REFLECTED CEILING PLANS.						
4. VERIFY EXACT MOUNTING HEIGHT AND LOCATIONS OF ALL WALL MOUNTED AND PENDANT MOUNTED LUMINAIRES WITH ARCHITECTURAL PLANS AND ELEVATIONS PRIOR TO ROUGH-IN.						
5. ANY PROPOSED ALTERNATE LUMINAIRES SHALL BE APPROVED BY THE ARCHITECT/OWNER/DEVELOPER/DESIGNER PRIOR TO FINAL BID PRICING.						
6. SHOULD THE CONTRACTOR PROPOSE TO FURNISH MATERIALS, EQUIPMENT, AND DEVICES, OTHER THAN THOSE SPECIFIED AND LISTED, THE CONTRACTOR SHALL SUBMIT A WRITTEN REQUEST FOR SUBSTITUTIONS, TO THE ENGINEER AT LEAST TEN (10) BUSINESS DAYS PRIOR TO BID OPENING. THE REQUEST SHALL BE AN ALTERNATE TO THE ORIGINAL BID AND SHALL INCLUDE A COMPLETE SPECIFICATIONS CUT SHEET SUBMITTAL AS OUTLINED IN THE SPECIFICATIONS, COMPLETE WITH DESCRIPTIVE (MANUFACTURER, BRAND NAME, CATALOG NUMBER, ETC.) AND TECHNICAL DATA FOR ALL ITEMS. INDICATE ANY ADDITIONS OR DEDUCTIONS TO THE CONTRACT PRICE WITH THE SUBSTITUTION SUBMITTAL AND ON THE BID FORM.						
7. ANY FINAL SELECTED/INSTALLED LIGHT FIXTURES WITHOUT A SPECIFICATION (OR TO BE SPECIFIED LATER BY ARCHITECT/OWNER/DEVELOPER/DESIGNER) LISTED IN THIS SCHEDULE SHALL NOT EXCEED THE WATTAGE LISTED, SHALL NOT HAVE A LOWERED DELIVERED LUMENS (IF LISTED), AND SHALL MATCH THE COLOR TEMPERATURE (IF LISTED).						

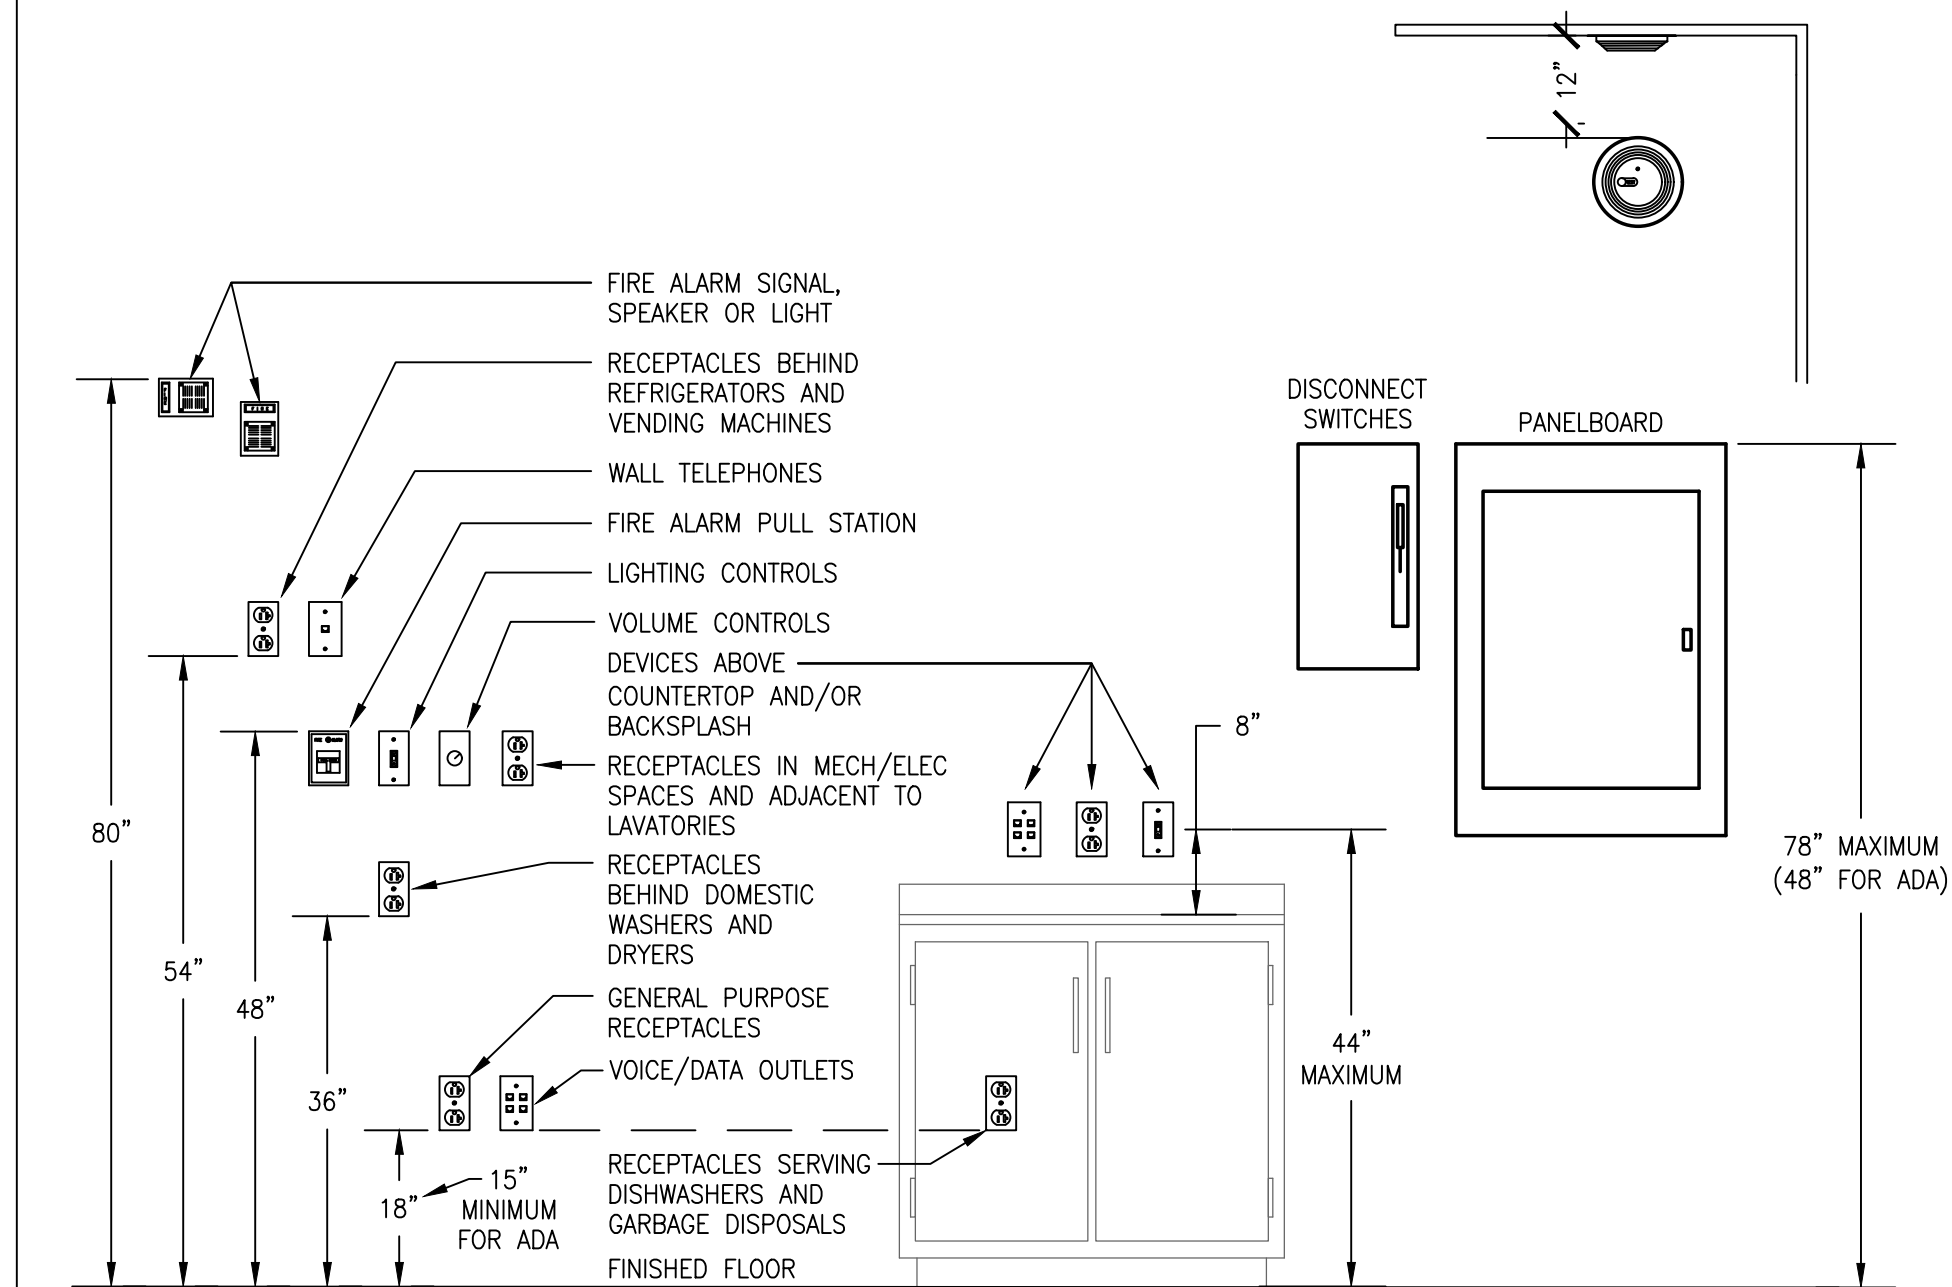

TYPICAL DEVICE MOUNTING DETAIL
NO SCALE

TYPICAL DEVICE MOUNTING DETAIL GENERAL NOTES:

- A. ALL MOUNTING HEIGHTS SHALL BE MEASURED FROM FINISHED FLOOR TO THE CENTERLINE OF DEVICE EXCEPT FIRE ALARM A/V DEVICES.
- B. NO WIRING DEVICES OR OUTLET BOXES SHALL BE MOUNTED BACK TO BACK.
- C. ALL MOUNTING DEVICES SHALL BE INSTALLED AT MOUNTING HEIGHTS AS INDICATED ON THIS DETAIL UNLESS OTHERWISE NOTED.
- D. FOR ALL ELEVATIONS (WHERE APPLICABLE), CASEWORK DETAILS, FIRE WALLS, SMOKE WALLS, LOCATION OF COUNTERTOP RECEPTACLES, LIGHTING FIXTURE SWITCHES, TELEPHONE ROUGH-INS, HEADWALLS, ETC., SEE ARCH DRAWINGS. WHERE NO ARCHITECTURAL ELEVATIONS OR DETAILS OCCUR, THE ELECTRICAL CONTRACTOR SHALL USE MEANS AND METHODS AS WELL AS THEIR FIELD KNOWLEDGE TO SPOT DEVICES IN THE BEST LOCATIONS FOR THE PROJECT.

ELEVATOR INSTALLATION GENERAL CONSTRUCTION NOTES

1. INCLUDE EXTERNALLY OPERABLE SHUNT TRIP CIRCUIT BREAKERS CAPABLE OF BEING LOCKED IN THE "OFF" POSITION FOR ELEVATOR 3-PHASE POWER FEED (NEC 620.51). PROVIDE WIRING FROM THE FIRE ALARM SYSTEM TO THE CIRCUIT BREAKER FOR SHUNT TRIP ACTIVATION UPON OPERATION OF THE ELEVATOR CONTROL HEAT DETECTORS, UNLESS OTHERWISE DIRECTED BY LOCAL ELEVATOR INSPECTOR (ASME A17.1-102 AND NEC 620.51(B)). ROUTE 120V WIRING THROUGH FIRE ALARM CONTROL PANEL TO MONITOR LOSS OF SHUNT TRIP POWER (TROUBLE ONLY INDICATION). IF BATTERY POWERED LOWERING IS SPECIFIED BY THE ARCHITECT, PROVIDE A NORMALLY CLOSED CONTACT AND WIRING TO ELEVATOR CONTROLLER TO DISCONNECT ADDITIONAL POWER SOURCE (NEC 620.91(C)).
2. INCLUDE 4-PAIR UNSHIELDED TWISTED PAIR CABLE, MINIMUM-CATEGORY 3 FROM CONTROLLER TO NEAREST AVAILABLE TELEPHONE SERVICES FOR CAR EMERGENCY PHONE/INTERCOM (ANSI A-17.1 - 211). COORDINATE EXACT LOCATION OF TELEPHONE SERVICES. **TYPICAL OF EACH ELEVATOR.**
3. INCLUDE FUSIBLE DISCONNECT OR EXTERNALLY OPERABLE CIRCUIT BREAKER CAPABLE OF BEING LOCKED IN THE "OFF" POSITION FOR 120 VOLT SINGLE PHASE FEED (NEC 620.53). PROVIDE A SECOND SWITCH IF A BRANCH CIRCUIT FOR A HEATING OR AIR CONDITIONING POWER SUPPLY IS PROVIDED (NEC 620.54). **TYPICAL OF EACH ELEVATOR.**
4. INCLUDE DEDICATED 20 AMP, 120 VOLT BRANCH CIRCUIT ON FOR CAR LIGHTS, RECEPTACLES, AUXILIARY LIGHTING SOURCE AND VENTILATOR (NEC 620.22). PROVIDE A SECOND SWITCH IF A BRANCH CIRCUIT FOR A HEATING OR AIR CONDITIONING POWER SUPPLY IS PROVIDED (NEC 620.22). **TYPICAL OF EACH ELEVATOR.**
5. INCLUDE WEATHERPROOF DUPLEX RECEPTACLE - (FOR ELEVATOR SERVICING) AND SWITCH FOR LIGHTS. COORDINATE LOCATION IN FIELD WITH ELEVATOR INSTALLER.
6. INCLUDE SMOKE DETECTOR WITH AUXILIARY CONTACTS FOR ELEVATOR RECALL - LOCATE OUTSIDE EACH ELEVATOR LANDING, AT TOP AND BOTTOM OF THE HOISTWAY (2 FEET ABOVE FLOOR) AND IN THE MACHINE ROOM (ANSI A-17.1 - 211.3b).
7. INCLUDE FIXED TEMPERATURE HEAT DETECTOR AT SETTING LESS THAN SPRINKLER HEAD TO BE MOUNTED ADJACENT TO HEAD. HEAT DETECTORS SHALL INITIATE AN AUTOMATIC POWER SHUTDOWN FOR 3-PHASE POWER TO THE ELEVATOR CONTROLLER, UNLESS OTHERWISE DIRECTED BY THE LOCAL ELEVATOR INSPECTOR. LOCATE HEAT DETECTORS IN THE MACHINE ROOM, AT THE TOP OF THE SHAFT AND AT THE BOTTOM OF THE SHAFT (2 FEET ABOVE THE FLOOR).

GENERAL ELECTRICAL NOTES

1. ANY AND ALL "BUILDING STANDARDS" AND/OR "BUILDING SPECIFICATIONS" SHALL BE CONSIDERED AN INTEGRAL PART OF THESE DOCUMENTS AND THE CONTRACTOR SHALL BE RESPONSIBLE TO OBTAIN A COPY OF THESE REQUIREMENTS/THIS DOCUMENT AND COMPLY WITH ALL REQUIREMENTS AND STANDARDS CONTAINED WITHIN.
2. THESE DRAWINGS ARE GENERALLY DIAGRAMMATIC AND ARE INTENDED TO CONVEY THE SCOPE OF WORK AND INDICATE GENERAL ARRANGEMENT OF LIGHTING FIXTURES, DEVICES, CONTROLS, ELECTRICAL FIXTURES, MOTORS, PANELBOARDS, EQUIPMENT, ETC. THE LOCATIONS OF ALL ITEMS SHOWN ON THESE DRAWINGS OR CALLED FOR IN THE SPECIFICATIONS THAT ARE NOT DEFINITELY FIXED BY DIMENSIONS ARE APPROXIMATE. THE EXACT LOCATIONS NECESSARY TO SECURE THE BEST CONDITIONS AND RESULTS MUST BE DETERMINED AT THE PROJECT. ALL LOCATIONS OF WORK EXPOSED TO VIEW ARE SUBJECT TO APPROVAL OF THE ARCHITECT PRIOR TO INSTALLATION.
3. THE ELECTRICAL CONTRACTOR SHALL VERIFY EXISTING CONDITIONS TO ENSURE THAT ALL NEW WORK WILL FIT INTO THE EXISTING STRUCTURE IN THE MANNER INTENDED AND AS SHOWN ON THE DRAWINGS. THE CONTRACTOR SHALL NOTIFY THE ARCHITECT/OWNERS REPRESENTATIVE PRIOR TO ANY ROUGH-INS, FABRICATIONS, OR PERFORMING ANY WORK IN THE AREA INVOLVING DIFFERENCES. NOTIFICATION SHALL BE IN THE FORM OF A DRAWING OR SKETCH INDICATING FIELD MEASUREMENTS AND NOTES RELATED TO THE AREA.
4. ANY DISCREPANCIES BETWEEN DRAWINGS AND SPECIFICATIONS SHALL BE PROMPTLY BROUGHT TO THE ATTENTION OF THE ENGINEER FOR CLARIFICATION DURING THE BIDDING PERIOD. NO ALLOWANCE SHALL SUBSEQUENTLY BE MADE TO THE CONTRACTOR BY REASON OF THEIR FAILURE TO HAVE BROUGHT SAID DISCREPANCIES TO THE ATTENTION OF THE ENGINEER DURING THE BIDDING PERIOD OR OF ANY ERROR ON THE CONTRACTOR'S PART.
5. ALL EQUIPMENT SHALL BE INSTALLED IN A NEAT, PROFESSIONAL AND WORKMANLIKE MANNER, RECTILINEAR TO BUILDING STRUCTURE.
6. ALL COMPONENTS SHOWN ON THE RISER/ONE-LINE DIAGRAMS, BUT NOT ON THE PLAN OR VICE VERSA, SHALL BE INCLUDED AS IF SHOWN ON BOTH.
7. REVIEW ALL TRADES' CONTRACT DOCUMENTS TO DETERMINE SPECIFIC MOUNTING LOCATIONS FOR ELECTRICAL EQUIPMENT. COORDINATE EXACT MOUNTING LOCATIONS WITH THE ARCHITECT.
8. REFER TO ARCHITECTURAL ELEVATIONS TO DETERMINE EXACT LOCATIONS OF ALL RECEPTACLES, OUTLETS/JACKS, SWITCHES, ETC. LUMINAIRES AND CEILING MOUNTED EQUIPMENT SHALL BE COORDINATED WITH THE ARCHITECTURAL REFLECTED CEILING PLANS.
9. EXACT LOCATION OF MECHANICAL EQUIPMENT THAT REQUIRE ELECTRICAL CONNECTION ARE SHOWN ON THE MECHANICAL DRAWINGS. FIELD VERIFY EXACT LOCATIONS WITH MECHANICAL CONTRACTOR PRIOR TO ANY ROUGH-INS.
10. ALL RACEWAY/CIRCUITING SHALL BE RUN CONCEALED UNLESS SPECIFIED OTHERWISE. CUT/FISH/PATCH WALLS AS REQUIRED. USE OF SURFACE RACEWAY MUST BE APPROVED BY ARCHITECT ALONG WITH PROPOSED ROUTING AND SURFACE RACEWAY TYPE.
11. ALL RACEWAYS RUNNING THROUGH BUILDING EXPANSION JOINTS SHALL BE EQUIPPED WITH EXPANSION FITTINGS.
12. CONDUIT HOME RUNS SHOWN ON THE DRAWING WITH MORE THAN (3) CURRENT CARRYING CONDUCTORS ARE SHOWN DIAGRAMMATICALLY. THIS CONTRACTOR SHALL NOT INSTALL MORE THAN (3) CURRENT CARRYING CONDUCTORS IN A RACEWAY UNLESS NATIONAL ELECTRICAL CODE (N.E.C.), ARTICLE 310.15 DERATING FACTORS ARE APPLIED.
13. ALL LIGHTING AND GENERAL POWER BRANCH CIRCUITS SHALL INCLUDE A SEPARATE NEUTRAL CONDUCTOR, UNLESS SPECIFICALLY NOTED OTHERWISE.
14. THE ELECTRICAL CONTRACTOR SHALL REFER TO THE ELECTRICAL SPECIFICATIONS FOR ACCEPTABLE CONDUIT TYPES/LOCATIONS. ALL CONDUIT SIZES ON THE DRAWINGS ARE BASED ON THE LATEST EDITION OF THE N.E.C. CONDUIT FILL TABLES FOR ELECTRICAL METALLIC TUBING (E.M.T.). CONDUIT SIZES SHALL BE REVISED TO THE SIZE REQUIRED, RELATIVE TO THE ACTUAL CONDUIT TYPE TO BE INSTALLED.
15. IT IS NOT INTENDED THAT THE PLANS INDICATE ALL THE NECESSARY BENDS, OFFSETS, PULL BOXES AND OBSTRUCTIONS. IT SHALL BE THE RESPONSIBILITY OF THE CONTRACTOR TO INSTALL THEIR WORK TO CONFORM TO THE STRUCTURE, MAINTAIN HEADROOM AND KEEP OPENINGS AND PASSAGEWAYS CLEAR. REFER TO THE ARCHITECTURAL DRAWINGS FOR ALL DIMENSIONS AS REQUIRED.
16. IT IS NOT INTENDED THAT THE PLANS INDICATE ALL CONDUIT ROUTES, PULL BOXES, ETC. CONTRACTOR SHALL BE RESPONSIBLE FOR DETERMINING ACTUAL CONDUIT ROUTING, QUANTITY AND LOCATION OF PULL BOXES WITHIN ACCESSIBLE LOCATIONS.
17. PROVIDE SCREW-COVER PULL BOXES IN CONDUIT RUNS AS REQUIRED TO LIMIT THE NUMBER OF BENDS TO NO MORE THAN THREE (3) OR 270 DEGREES TOTAL. SIZE PULL BOXES IN ACCORDANCE WITH NEC, ARTICLE 314.28. DOCUMENT ON RECORD DRAWINGS, SIZE AND LOCATION OF PULL BOXES USED IN FEEDER CONDUIT RUNS.
18. ALL OUTLET BOXES IN WALLS SHALL HAVE A MINIMUM OF ONE (1) DEDICATED VERTICAL CONDUIT ENTERING AT THE TOP OF THE BOX. HORIZONTAL CONDUIT CONNECTIONS SHALL ONLY BE PERMITTED UNDER WINDOWS OR UNLESS OTHERWISE NOTED ON DRAWINGS.
19. WHERE MULTIPLE DEVICES ARE INDICATED IN A COMMON LOCATION, GANG INTO A SINGLE COVER PLATE.
20. NEW OR MODIFIED PANELS SHALL BE PROVIDED WITH ENGRAVED NAMEPLATES AS DESIGNATED ON PANEL SCHEDULES SECURED TO PANEL FACE AND DENOTING ORIGIN OF FEEDER FROM WHICH PANEL IS SERVED.

SYMBOL LEGEND

SYMBOL	DESCRIPTION
	LUMINAIRE. "A" INDICATES TYPE; "N" INDICATES SWITCH CONTROL. "/EM" INDICATES LUMINAIRE HAS INTEGRAL 90-MINUTE EMERGENCY BATTERY DRIVER.
	LUMINAIRE WIRED FOR 24 HOUR OPERATION, INDICATED WITH HATCH AND A "/N" DESIGNATION.
	SELF CONTAINED LED UNIVERSAL MOUNTED "EXIT" SIGN. PROVIDE QUANTITY OF FACES AND DIRECTIONAL ARROWS AS INDICATED ON FLOOR PLANS. REFER TO LUMINAIRE SCHEDULE FOR ADDITIONAL INFORMATION.
	EMERGENCY LIGHTING BATTERY UNIT WITH HEADS AS INDICATED. REFER TO LUMINAIRE SCHEDULE FOR ADDITIONAL INFORMATION.
	LIGHT SWITCH, SINGLE POLE; 20 AMPERE, 120/277 VOLT, 1HP. "X" INDICATES SWITCH CONTROL. "X" INDICATES THE FOLLOWING:
	"3" CONTROL OF SPECIFIED LUMINAIRES.
	"4" THREE-WAY TYPE.
	"2" FOUR-WAY TYPE.
	"1" SWITCH TO BE WIRED AHEAD OF DOWNSTREAM LINE VOLTAGE WALLBOX TYPE DIMMING SWITCH, INDICATED BY THE SAME SWITCH CONTROL TAG.
	"2P" DOUBLE POLE TYPE.
	"TM" PROGRAMMABLE TIMER SWITCH, TYPICALLY HONEYWELL #RPLS730B.
	"OS" LINE VOLTAGE MULTI-TECHNOLOGY WALL SWITCH OCCUPANCY SENSOR WITH MANUAL ON/OFF SWITCH. REFER TO DIAGRAM ON DRAWING ### .
	"VS" LINE VOLTAGE MULTI-TECHNOLOGY WALL SWITCH VACANCY SENSOR WITH MANUAL ON/OFF SWITCH. REFER TO DIAGRAM ON DRAWING ### .
	"COS" LINE VOLTAGE PIR WALL SWITCH CORRIDOR-TYPE OCCUPANCY SENSOR WITHOUT CONTROL SWITCH, TYPICALLY SENSOR SWITCH #HWR13-SN SERIES. MOUNT AT 7'-0" A.F.F. UNLESS OTHERWISE SHOWN.
	"CYS" LINE VOLTAGE PIR WALL SWITCH CORRIDOR-TYPE OCCUPANCY SENSOR WITH CONTROL SWITCH, TYPICALLY SENSOR SWITCH #HWR13 SERIES. MOUNT AT 7'-0" A.F.F. UNLESS OTHERWISE SHOWN.
	"VDS" LINE VOLTAGE ON/OFF SWITCH WITH DIMMER FUNCTION AND VACANCY SENSOR. REFER TO DIAGRAM ON DRAWING ### .
	"LV" LOW VOLTAGE ON/OFF SWITCH.
	"LV2" DUAL ZONE LOW VOLTAGE ON/OFF SWITCH.
	"LV4" QUAD ZONE LOW VOLTAGE ON/OFF SWITCH.
	"LVD" LOW VOLTAGE ON/OFF SWITCH WITH DIMMER FUNCTION.
	"LVD2" DUAL ZONE LOW VOLTAGE ON/OFF SWITCH WITH DIMMER FUNCTION.
	"LVD4" QUAD ZONE LOW VOLTAGE ON/OFF SWITCH WITH DIMMER FUNCTION.
	"SCN" SCENE CONTROLLER CAPABLE OF A MINIMUM OF FOUR PRESETS.
	LINE VOLTAGE WALLBOX TYPE DIMMING SWITCH. COORDINATE DIMMING PROTOCOL OF THIS DIMMING SWITCH AND LIGHTING LOAD SERVED PRIOR TO PLACING PURCHASE ORDER. "S" INDICATES SWITCH CONTROL.
	120/277V RATED CEILING MOUNTED OCCUPANCY SENSOR. A "OR" DESIGNATIONS INDICATES A DUAL RELAY SENSOR FOR 3/4 WAY SWITCHING. "X" REPRESENTS CONTROLLED LIGHTING ZONE (IF LOCATED IN A ROOM/AREA WITH MULTIPLE LIGHTING ZONES). TYPICALLY SENSOR SWITCH #CMR SERIES.
	LOW VOLTAGE CEILING MOUNTED PHOTOSENSOR, "X" REPRESENTS CONTROLLED LIGHTING ZONE.
	LOW VOLTAGE MULTI-TECHNOLOGY CEILING MOUNTED OCCUPANCY SENSOR, "X" REPRESENTS CONTROLLED LIGHTING ZONE.
	LOW VOLTAGE MULTI-TECHNOLOGY CEILING MOUNTED VACANCY SENSOR, "X" REPRESENTS CONTROLLED LIGHTING ZONE.
	CIRCUITRY TURNING UP
	CIRCUITRY TURNING DOWN
	UNDERGROUND OR UNDERSLAB CONDUIT/RACEWAY AND/OR CIRCUITING.
	CONDUIT HOME RUN TO PANEL/CIRCUIT BREAKER AS INDICATED. ALL UNMARKED HOMERUNS TO CONTAIN 2-12 AWG AND IN 3/4" CONDUIT (MINIMUM), UNLESS NOTED OTHERWISE. SIZE CONDUIT AND PROVIDE JUNCTION BOXES PER CODE UNLESS OTHERWISE NOTED.
	DWELLING UNITS; DWELLING UNIT SINGLE-PHASE LOAD CENTER.
	ALL OTHER AREAS; BRANCH CIRCUIT PANELBOARD.
	DISCONNECT SWITCH. REFER TO EQUIPMENT SCHEDULE OR PLAN NOTE FOR FUSING NECESSITY, SIZES, RATINGS, ETC.
	DUPLEX RECEPTACLE - 125 VOLT, 20 AMPERE, 2 POLE, 3 WIRE, GROUNDING TYPE MOUNTED AT 18" AFF UNLESS NOTED OTHERWISE.
	DOUBLE DUPLEX RECEPTACLE - 125 VOLT, 20 AMPERE, 2 POLE, 3 WIRE, GROUNDING TYPE MOUNTED AT 18" AFF UNLESS NOTED OTHERWISE.
	GFCI GROUND TYPE DUPLEX RECEPTACLE - 125 VOLT, 20 AMPERE, 2 POLE, 3 WIRE, GROUNDING TYPE MOUNTED AT 18" AFF UNLESS NOTED OTHERWISE.
	DUPLEX RECEPTACLE - 125 VOLT, 20 AMPERE, 2 POLE, 3 WIRE, GROUNDING TYPE MOUNTED AT 18" AFF UNLESS NOTED OTHERWISE. RECEPTACLE SHALL BE SPLIT WIRED SUCH THAT TOP OUTLET TO BE WIRED FOR SWITCHING TO SWITCH INDICATED BY 'S'.
	TAMPER RESISTANT, POP-UP COUNTER RECEPTACLE - 125 VOLT, 20 AMPERE, 2 POLE, 3 WIRE, GROUNDING TYPE. TYPICALLY BRYANT #RGT220xx.
	FLOOR BOX WITH DUPLEX RECEPTACLE. PROVIDE APPROPRIATE BOX TYPE FOR CONCRETE OR WOOD FLOOR CONSTRUCTION.
	RECEPTACLE SYMBOL WITH ADDITIONAL SUBSCRIPT DESIGNATES TYPE OR SPECIFIC REQUIREMENTS AS FOLLOWS:
	"AC" INDICATES MOUNTED 8" ABOVE COUNTER UNLESS NOTED OTHERWISE ON ARCHITECTURAL ELEVATIONS.
	"CLG" FLUSH CEILING MOUNTED OR 12" ABOVE WINDOW.
	"H8" RECEPTACLE MOUNTED AT HEIGHT INDICATED.
	"IL" RECEPTACLE WITH ILLUMINATED NIGHT LIGHT.
	"VF" VERIFY EXISTING MOUNTING HEIGHT IN FIELD, OR CONFIRM EXACT LOCATION IN OF NEW DEVICE IN FIELD.
	"WP" WEATHERPROOF "WHILE-IN-USE" (HUBBELL #WP26M) COVER.
	"U" DUPLEX RECEPTACLE WITH ONE USB TYPE "A" PORT AND ONE TYPE "C" PORT, LEVITON #TS633 SERIES OR EQUAL.
	"T" TAMPER RESISTANT (ONLY INDICATED OUTSIDE OF DWELLING UNITS).
	"G" RECEPTACLE PROTECTED BY UPSTREAM GFCI OR GFI-TYPE BREAKER WITH "GFCI PROTECTED" LABEL ON THE FACE OF DEVICE.
	"CR" RECEPTACLE CONTROLLED BY AN AUTOMATIC CONTROL DEVICE FOR PLUG LOAD CONTROL. DURABLY AND PERMANENTLY MARKED WITH THE WORD "CONTROLLED" AND THE SYMBOL SHOWN IN NEC FIGURE #406.3(F) .
	SPECIAL PURPOSE RECEPTACLE. REFER TO EQUIPMENT SCHEDULE OR PLAN NOTE FOR RECEPTACLE TYPE AND RATINGS. COORDINATE EXACT NEMA CONFIGURATION WITH EQUIPMENT PRIOR TO ROUGH-IN.
	JUNCTION BOX - SIZE PER N.E.C. ARTICLE 314 REQUIREMENTS.
	ALL AREAS, BESIDES IN DWELLING UNITS; COMBINATION VOICE/DATA OUTLET (4" x 2-1/8" DEEP JUNCTION BOX) COMPLETE WITH SINGLE GANG MUD RING (VERIFY DRYWALL THICKNESS) AND COVER PLATE (COLOR SELECTION BY ARCHITECT) MOUNTED AT 18" A.F.F. PROVIDE 1-0" CONDUIT WITH INSULATING BUSHING AND PULLSTRING STUBBED UP 12" INTO ACCESSIBLE CEILING SPACE.
	WITHIN DWELLING UNITS; REFER TO TYPICAL APARTMENT DATA FACEPLATE DETAILS ON DRAWING ### .
	FLOOR BOX WITH DATA/VOICE OUTLET AS DESCRIBED ABOVE. PROVIDE APPROPRIATE BOX TYPE FOR CONCRETE OR WOOD FLOOR CONSTRUCTION.
	FIRE ALARM SYSTEM MANUAL PULL STATION.
	FIRE ALARM COMBINATION AUDIBLE/VISUAL (HORN/STROBE) SIGNALING DEVICE. LF DESIGNATION INDICATES LOW FREQUENCY ALARM DEVICE.
	FIRE ALARM VISUAL (STROBE) ONLY SIGNALING DEVICE.
	ALL AREAS, BESIDES IN DWELLING UNITS; FIRE ALARM SYSTEM SMOKE DETECTOR.
	WITHIN DWELLING UNITS; DWELLING UNIT SMOKE ALARM. REFER TO DETAIL(S) ON DRAWING ### .
	WITHIN DWELLING UNITS; BUILDING FIRE ALARM SYSTEM ADDRESSABLE SMOKE DETECTOR WITH 520HZ LOW FREQUENCY SOUNDER BASE.
	"CO" DESIGNATION INDICATES COMBINATION, "MULTI-CRITERIA" SMOKE/CARBON MONOXIDE CAPABILITY.
	FIRE ALARM CONTROL PANEL. THE BRANCH CIRCUIT SERVING THIS PANEL SHALL ONLY SERVE FIRE ALARM EQUIPMENT. REFER TO PANEL SCHEDULE(S).
	FIRE ALARM ANNUNCIATOR PANEL. THE BRANCH CIRCUIT SERVING THIS PANEL SHALL ONLY SERVE FIRE ALARM EQUIPMENT. REFER TO PANEL SCHEDULE(S).
	TAMPER SWITCH. COORDINATE ALL REQUIREMENTS WITH SPRINKLER/FIRE SUPPRESSION DRAWINGS.
	FLOW SWITCH. COORDINATE ALL REQUIREMENTS WITH SPRINKLER/FIRE SUPPRESSION DRAWINGS.
	MAGNETIC DOOR HOLD OPEN

WIRING SCHEDULE FOR 15/20A RECEPTACLE & LIGHTING CIRCUITS	
DISTANCE	120V
1' - 100'	#12 (AWG)
100' - 150'	#10 (AWG)
150' - 200'	#10 (AWG)
200' - 300'	#8 (AWG)

Seal

NOT FOR CONSTRUCTION

Issue:	Date:	By:
SCHEMATIC DESIGN	01.07.26	BAC
DESIGN DEVELOPMENT	03.05.26	BAC

who's engineering
2012 West 25th Street, Suite 900
Cleveland, OH 44113
Phone: 216 227 8505

**OSU
AIRPORT WEST
BUILDING C**

**3455 W. Dublin Granville Rd,
Columbus OH, 43235**

Drawing Title
**ELECTRICAL LEGEND
AND DETAILS**


Date:	Project Number:
03.05.2026	24-065
Drawn By: DJS	Drawing Number:
Checked By: KDS	
Approved: GSS	

E0.03C

Seal

**NOT FOR
CONSTRUCTION**

Issue:	Date:	By:
SCHEMATIC DESIGN	01.07.26	BAC
DESIGN DEVELOPMENT	03.05.26	BAC

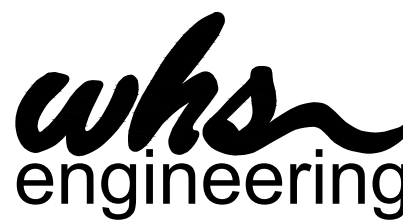[illegible]

2012 West 25th Street, Suite 900
Cleveland, OH 44113
Phone: 216 227 8505

**OSU
AIRPORT WEST
BUILDING C**

**3455 W. Dublin Granville Rd,
Columbus OH, 43235**

ELECTRICAL SCHEDULES AND DETAILS


Date	Project Number
03.05.2026	24-065
Drawn by	Drawing Number
DJS	E0.04C
Checked by	
KDS	
Approved	
GSS	

- GENERAL LIGHTING PLAN NOTES
- ALL EXIT SIGNS, EMERGENCY LIGHTING BATTERY PACKS, EMERGENCY LUMINAIRES AND NIGHT LIGHTS (DENOTED "NL") SHALL BE CONNECTED TO THE LOCAL LIGHTING CIRCUIT AHEAD OF ANY CONTROLS SUCH AS: SWITCHES (DEVICE), OCCUPANCY SENSORS AND/OR RELAY CONTROLS.
 - EXACT LOCATION OF ALL LUMINAIRES, AND EXACT MOUNTING HEIGHT OF ALL PENDANT MOUNTED LUMINAIRES SHALL BE COORDINATED WITH ARCHITECTURAL DRAWINGS PRIOR TO ANY ROUGH-INS.
 - REFER TO WIRING SCHEDULE ON SHEET #E0.03A/B/C FOR 15A/20A LIGHTING BRANCH CIRCUITS FOR ALL CONDUCTOR SIZES TO ACCOUNT FOR VOLTAGE DROP.
 - ALL WIRING SHALL BE IDENTIFIED BY PANELBOARD AND CIRCUIT NUMBER(S) IN ALL CABINETS, JUNCTION BOXES, WIRING TROUGHS, ENCLOSURES, SPLICE OR TERMINATION POINTS, ETC.
 - A NEW TYPED PANELBOARD DIRECTORY CARD SHALL BE PROVIDED FOR ALL PANELS INSTALLED OR MODIFIED UNDER THIS CONTRACT. NEW DIRECTORY CARDS SHALL BE LOCATED ON THE INSIDE DOOR OF ASSOCIATED PANELS.

Seal

NOT FOR
CONSTRUCTION

Issue:	Date:	By:
SCHEMATIC DESIGN	01.07.26	BAC
DESIGN DEVELOPMENT	03.05.26	BAC

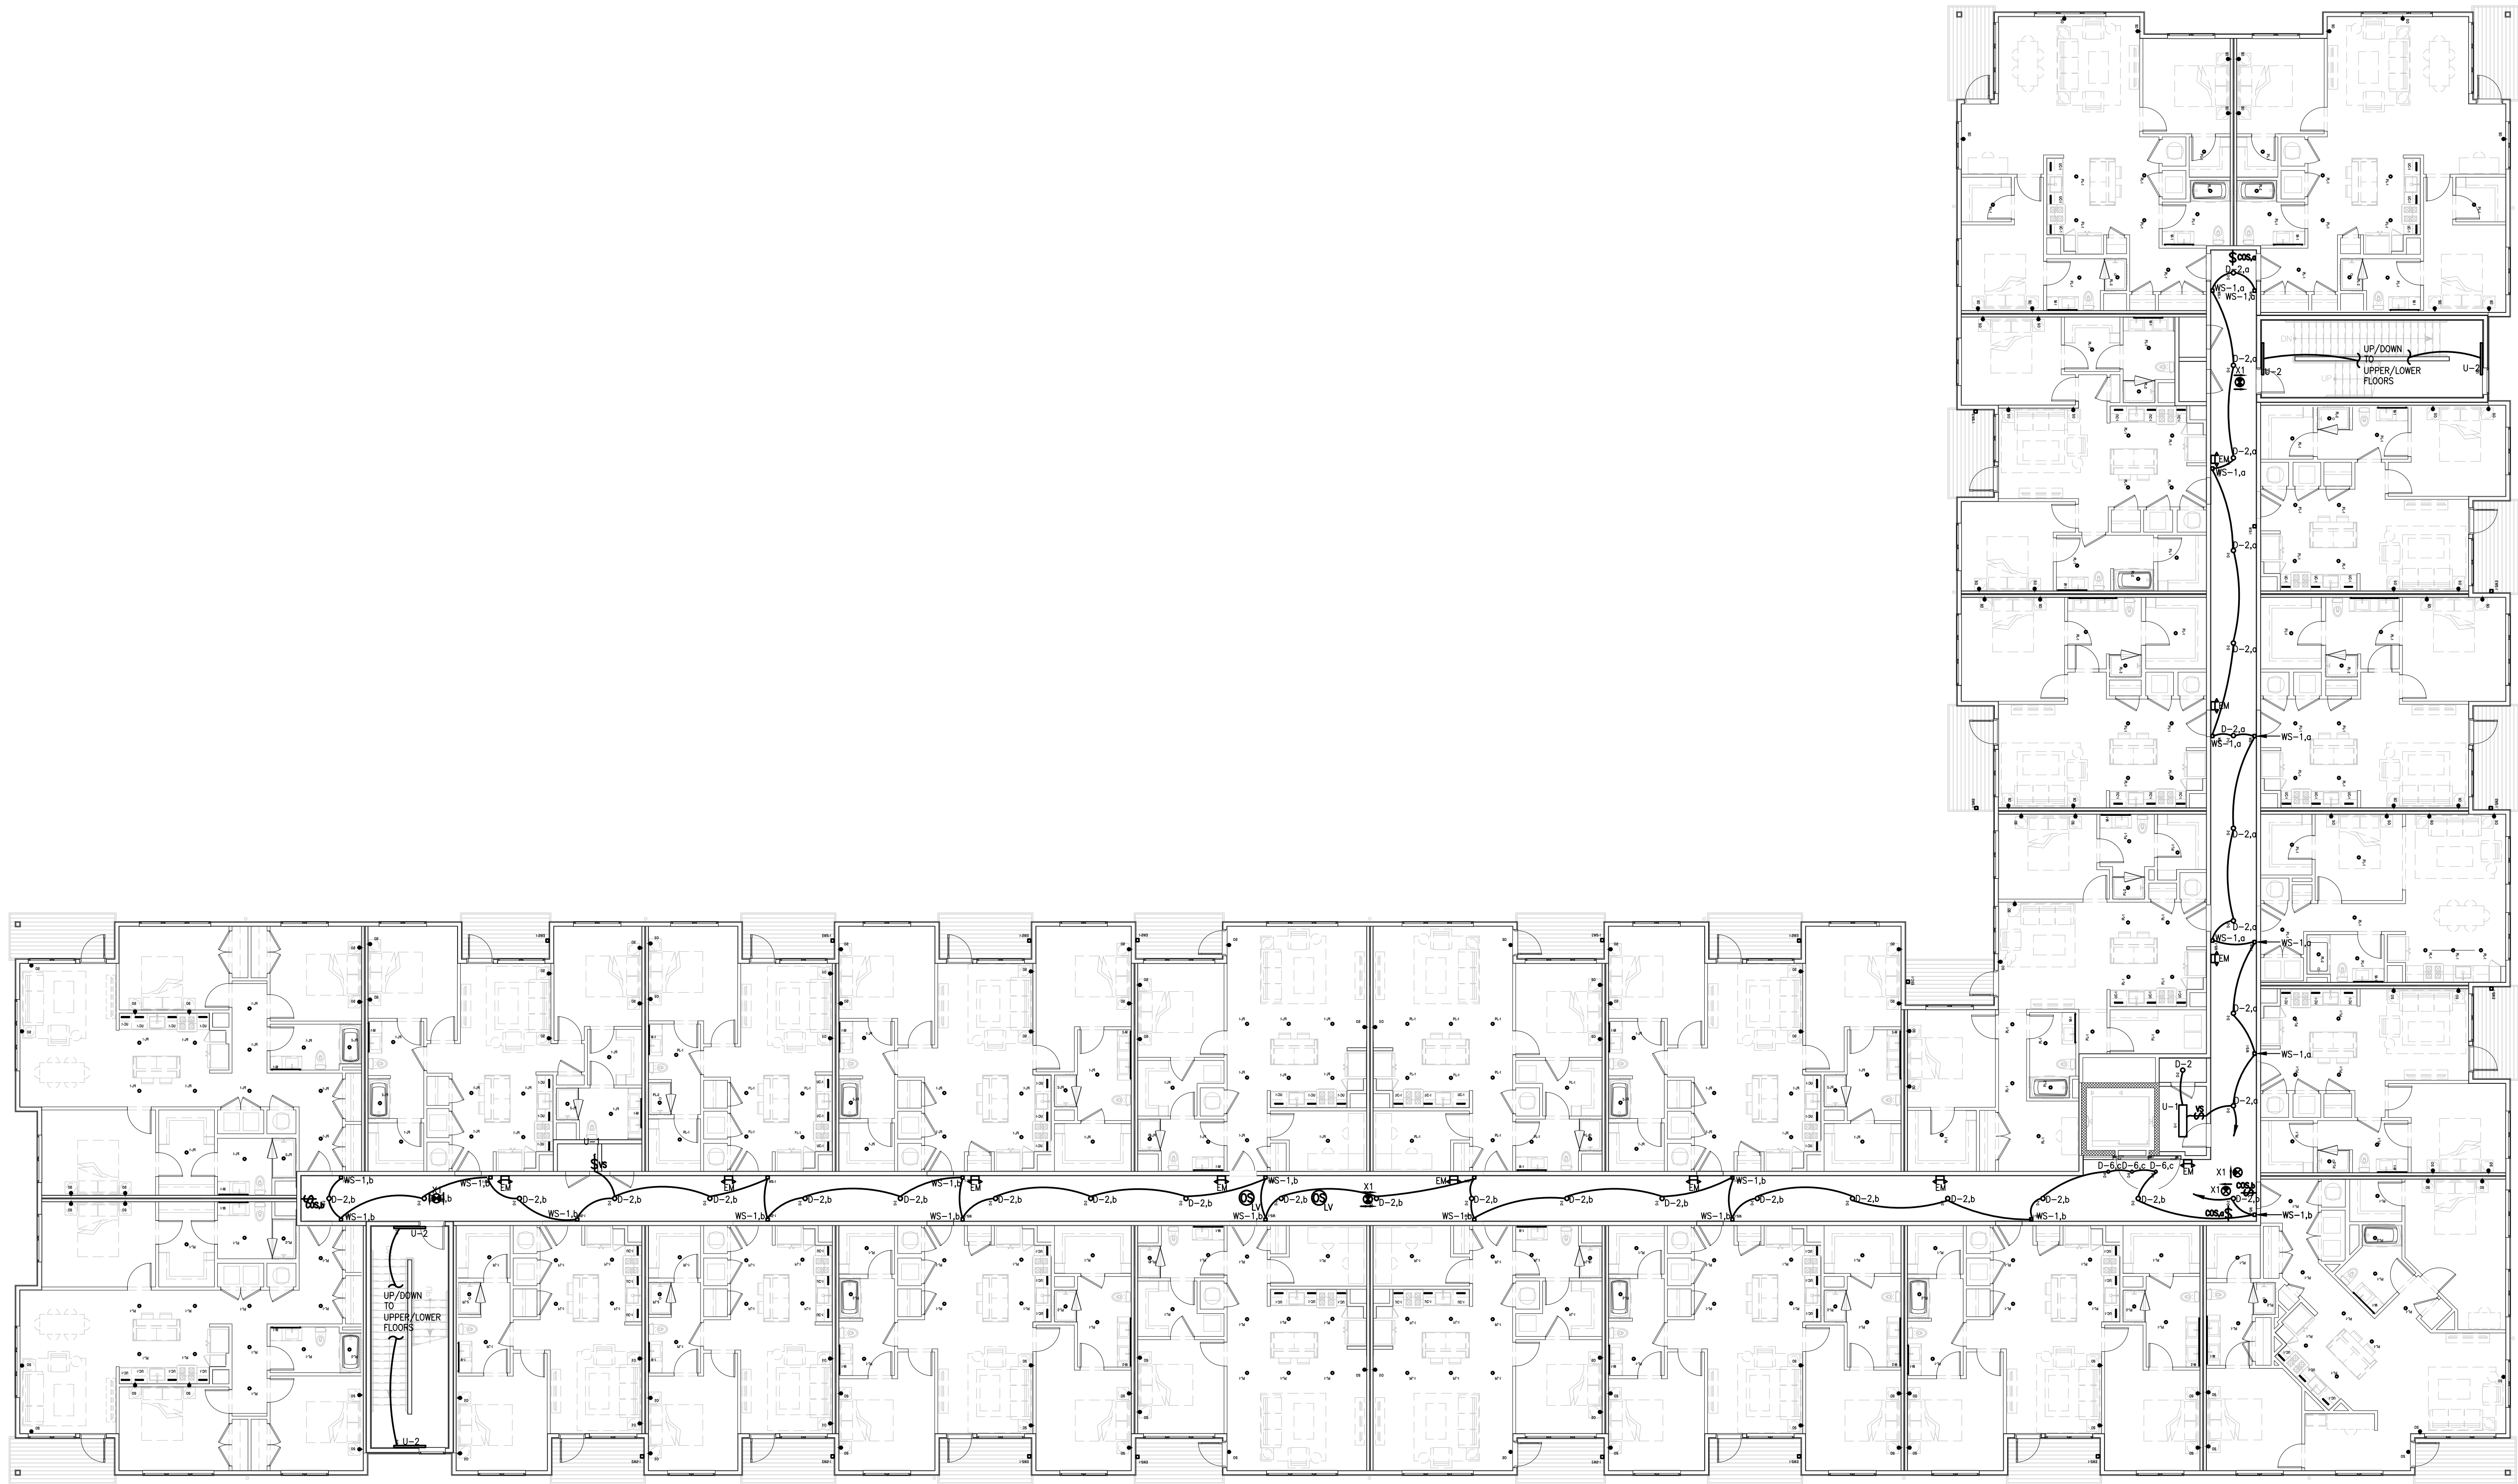

1
E1.02C
BUILDING C
SECOND FLOOR LIGHTING PLAN
SCALE: 3/32" = 1'-0"

whs
engineering
2012 West 25th Street, Suite 900
Cleveland, OH 44113
Phone: 216 227 8505

**OSU
AIRPORT WEST
BUILDING C**


3455 W. Dublin Granville Rd,
Columbus OH, 43235

Drawing Title
**SECOND FLOOR LIGHTING
PLAN**

Date: 03.05.2026	Project Number: 24-065
Drawn By: DJS	Drawing Number: E1.02C
Checked By: KDS	
Approved: GSS	

2	LOCATION OF AREA OF RESCUE COMMUNICATION BASE STATION. REFER TO DIAGRAM ON DRAWING #E0-02. REFER TO ELEVATOR GENERAL INSTALLATION NOTES ON DRAWING #E0-03 FOR ALL ELEVATOR ROOM AND ELEVATOR PIT ELECTRICAL REQUIREMENTS.
3	ALL ELEVATOR PIT WALLS AND BACKDROP PAINTED WITH FIRE RETARDANT PAINT FOR MAIN COMMUNICATION TERMINAL BOARD (TELEPHONE, TELEVISION, ETC.). INCLUDE ALL WORK REQUIRED BY RESPECTIVE UTILITIES. PROVIDE A COPPER GROUNDING BUS AND #6 AWG ALUMINUM CONDUCTOR TO EACH COMMUNICATIONS TERMINAL BOARD. PROVIDE 1/2" DIA. COPPER RODS TO EACH COMMUNICATIONS RECEPTACLE INSTALLED AT THIS TERMINAL BOARD SERVED FROM (2) 20A-120V-1P DEDICATED CIRCUITS. REFER TO COMMUNICATION RISER DIAGRAM ON DRAWING #E0-02 FOR ADDITIONAL INFORMATION.
4	PROVIDE COPPER GROUNDING FOR ALL RECEPTACLES AT THIS LOCATION VERTICALLY AT EACH FLOOR. PROVIDE DOWNER AS SHOWN ON DRAWING WITH FLOOR.

- EXIST LOCATION OF MECHANICAL, PLUMBING, CHILTRON, FURNITURE SYSTEMS, OWNER FURNISHED EQUIPMENT, ETC. THAT REQUIRE ELECTRICAL CONNECTIONS ARE SHOWN ON THE MECHANICAL, PLUMBING, AND/OR ARCHITECTURAL DRAWINGS. COORDINATE EXIST LOCATIONS WITH RESPECTIVE CONTRACTORS AND/OR VENDORS PRIOR TO ANY ROUGH-IN.
- PRIOR TO ROUGH-IN, REVIEW AND COORDINATE WITH ALL OTHER TRADES' CONTRACT DOCUMENTS TO DETERMINE SPECIFIC MOUNTING LOCATIONS AND ELECTRICAL REQUIREMENTS (VOLTAGE, PHASE, KW, HP, CONNECTION TYPE, ETC.) FOR HVAC AND PLUMBING EQUIPMENT. COORDINATE EXIST MOUNTING LOCATIONS WITH THE SPECIFIC TRADE AND ARCHITECT.
- REFER TO WIRING SCHEDULE ON SHEET **600305/B/C** FOR 15A/20A RECEPTACLE BRANCH CIRCUITS FOR ALL CONDUCTOR SIZES TO ACCOUNT FOR VOLTAGE DROP.
- ALL WIRING SHALL BE IDENTIFIED BY PANELBOARD AND CIRCUIT NUMBER(S) IN THE FOLLOWING: JUNCTION BOXES, WIRING TROUGHS, ENCLOSURES, SPICE OR TERMINATION POINTS, ETC.
- A NEW TYPED PANELBOARD DIRECTORY CARD SHALL BE PROVIDED FOR ALL PANELS INSTALLED OR MODIFIED UNDER THIS CONTRACT. NEW DIRECTORY CARDS SHALL BE LOCATED ON THE INSIDE DOOR OF ASSOCIATED PANELS.

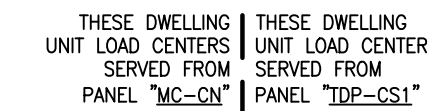

THESE DWELLING UNIT LOAD CENTERS SERVED FROM PANEL "MC-CN"	THESE DWELLING UNIT LOAD CENTER SERVED FROM PANEL "TDP-CS1"
---	--

1
E001C

**NOT FOR
CONSTRUCTION**

DESIGN DEVELOPMENT	03.05.26	BAC
--------------------	----------	-----

2012 West 25th Street, Suite 900
Cleveland, OH 44113
Phone: 216 227 8505

3455 W. Dublin Granville Rd,
Columbus OH, 43235

Drawing Title

**FIRST FLOOR POWER
PLAN**

03.05.2026	24-065
------------	--------

Checked by **E2 01C**

RDS	L2.01C
Approved	


E2.01C

CODED NOTES

- 1 LOCATION OF AREA OF RESCUE COMMUNICATION BASE STATION. REFER TO DIAGRAM ON DRAWING #E0-02.
- 2 REFER TO ELEVATOR GENERAL INSTALLATION NOTES ON DRAWING #E0-03 FOR ALL ELEVATOR ROOM AND ELEVATOR PIT ELECTRICAL REQUIREMENTS.
- 3 PROVIDE A 4' x 4' x 3/4" THICK PLYWOOD BACKBOARD PAINTED WITH FIRE RETARDANT PAINT FOR MAIN COMMUNICATION TERMINAL BOARD (TELEPHONE, TELEVISION, ETC.). INCLUDE ALL WORK REQUIRED BY RESPECTIVE UTILITIES. PROVIDE A COPPER GROUNDING BUS AND #6 AWG GROUNDING CONDUCTOR TO SERVICE GROUNDING POINT(S) (REFER TO DETAIL ON DRAWING #E0-02). INCLUDE (2) DOUBLE DUPLEX RECEPTACLES INSTALLED AT THIS TERMINAL BOARD SERVED FROM (2) 20A-120V-1Ø DEDICATED CIRCUITS. REFER TO COMMUNICATION RISER DIAGRAM ON DRAWING #E0-02 FOR ADDITIONAL INFORMATION.
- 4 ROUTE BRANCH CIRCUITING FOR RECEPTACLES AT THIS LOCATION VERTICALLY AT EACH FLOOR. PROVIDE HOMERUN AS SHOWN ON FOURTH FLOOR.

GENERAL POWER AND COMMUNICATION PLAN NOTES

- EXACT LOCATION OF MECHANICAL, PLUMBING, KITCHEN, FURNITURE SYSTEMS, OWNER FURNISHED EQUIPMENT, ETC. THAT REQUIRE ELECTRICAL CONNECTIONS ARE SHOWN ON THE MECHANICAL, PLUMBING, AND/OR ARCHITECTURAL DRAWINGS. COORDINATE EXACT LOCATIONS WITH RESPECTIVE CONTRACTORS AND/OR VENDORS PRIOR TO ANY ROUGH-INS.
- PRIOR TO ROUGH-IN, REVIEW AND COORDINATE WITH ALL OTHER TRADES' CONTRACT DOCUMENTS TO DETERMINE SPECIFIC MOUNTING LOCATIONS AND ELECTRICAL REQUIREMENTS (VOLTAGE, PHASE, KW, HP, CONNECTION TYPE, ETC.) FOR HVAC AND PLUMBING EQUIPMENT. COORDINATE EXACT MOUNTING LOCATIONS WITH THE SPECIFIC TRADE AND ARCHITECT.
- REFER TO WIRING SCHEDULE ON SHEET #E0.03A/B/C FOR 15A/20A RECEPTACLE BRANCH CIRCUITS FOR ALL CONDUCTOR SIZES TO ACCOUNT FOR VOLTAGE DROP.
- ALL WIRING SHALL BE IDENTIFIED BY PANELBOARD AND CIRCUIT NUMBER(S) IN ALL CABINETS, JUNCTION BOXES, WIRING TROUGHS, ENCLOSURES, SPLICE OR TERMINATION POINTS, ETC.
- A NEW TYPED PANELBOARD DIRECTORY CARD SHALL BE PROVIDED FOR ALL PANELS INSTALLED OR MODIFIED UNDER THIS CONTRACT. NEW DIRECTORY CARDS SHALL BE LOCATED ON THE INSIDE DOOR OF ASSOCIATED PANELS.

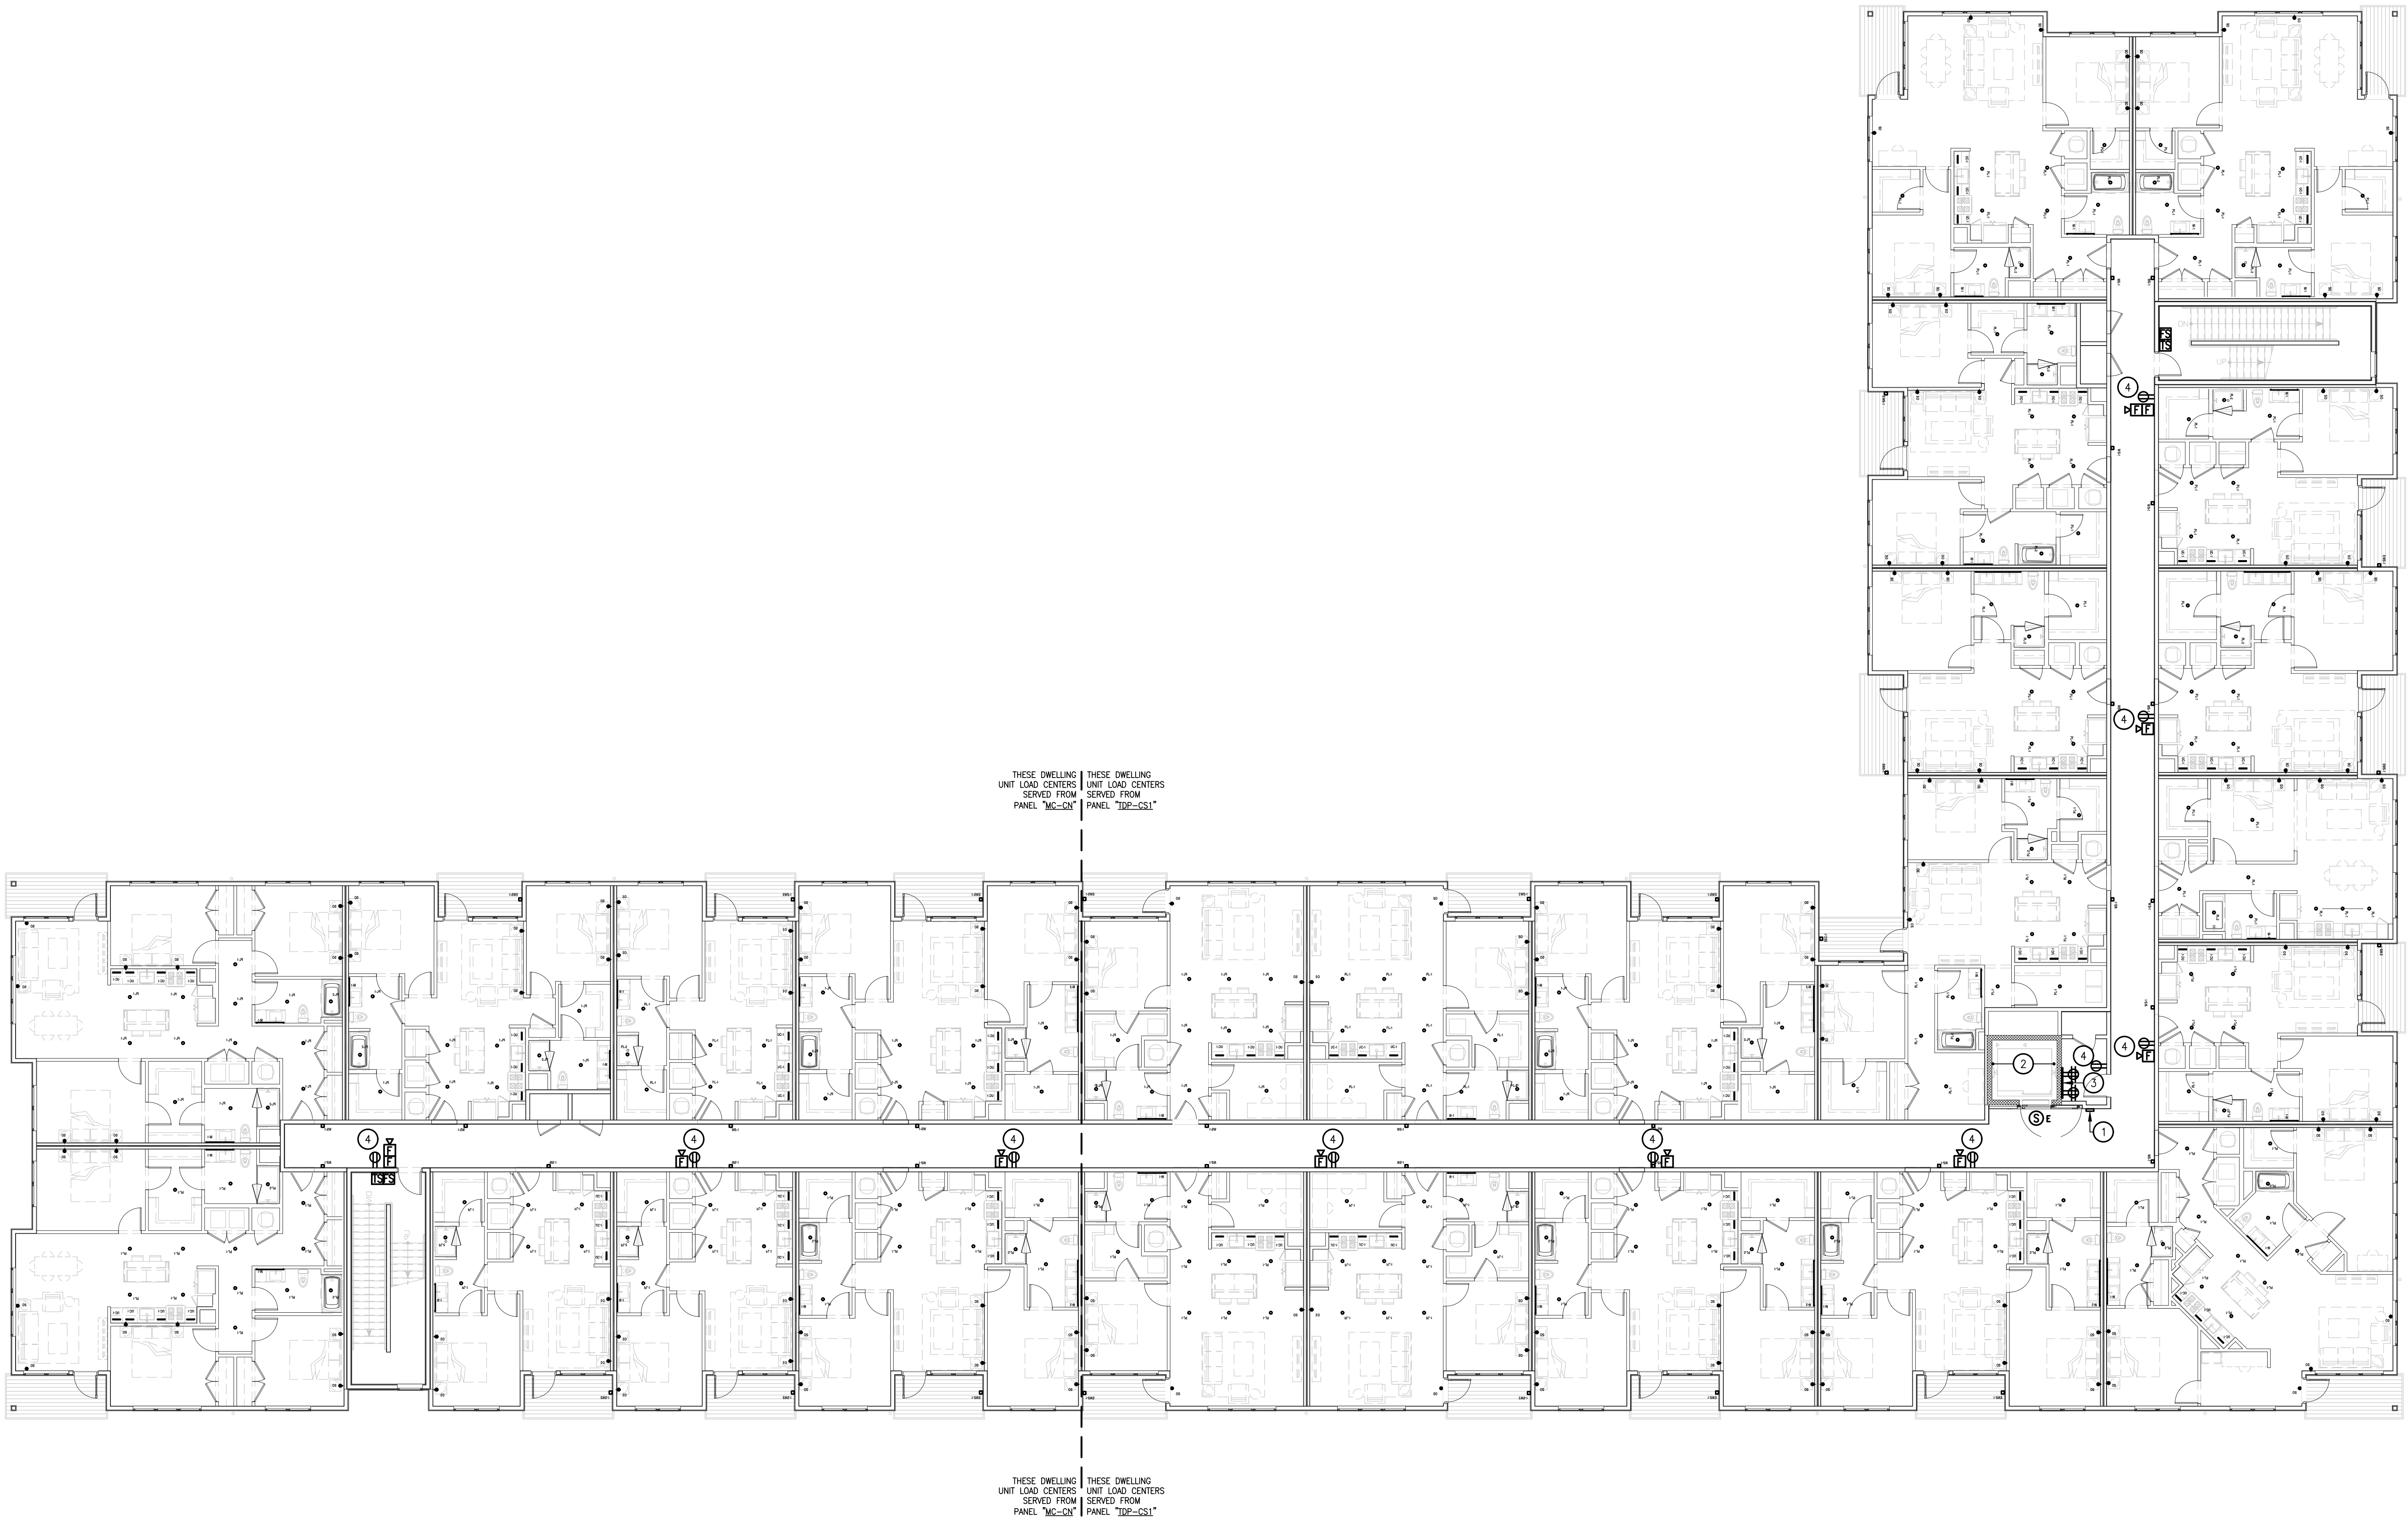

BUILDING C
SECOND FLOOR POWER PLAN
SCALE: 3/32" = 1'-0"

Seal

NOT FOR
CONSTRUCTION

Issue:	Date:	By:
SCHEMATIC DESIGN	01.07.26	BAC
DESIGN DEVELOPMENT	03.05.26	BAC

whs
engineering

2012 West 25th Street, Suite 900
Cleveland, OH 44113
Phone: 216 227 8505

**OSU
AIRPORT WEST
BUILDING C**

3455 W. Dublin Granville Rd,
Columbus OH, 43235

Drawing Title
**SECOND FLOOR POWER
PLAN**


Date: 03.05.2026	Project Number: 24-065
Drawn by: DJS	Drawing Number: E2.02C
Checked by: KDS	
Approved: GSS	

CODED NOTES

- ① LOCATION OF AREA OF RESCUE COMMUNICATION BASE STATION. REFER TO DIAGRAM ON DRAWING #EO-02.
- ② REFER TO ELEVATOR GENERAL INSTALLATION NOTES ON DRAWING #EO-03 FOR ALL ELEVATOR ROOM AND ELEVATOR PIT ELECTRICAL REQUIREMENTS.
- ③ PROVIDE A 4" x 4" x 3/4" THICK PLYWOOD BACKBOARD PAINTED WITH FIRE RETARDANT PAINT FOR MAIN COMMUNICATION TERMINAL BOARD (TELEPHONE, TELEVISION, ETC.). INCLUDE ALL WORK REQUIRED BY RESPECTIVE UTILITIES. PROVIDE A COPPER GROUNDING BUS AND #6 AWG GROUNDING CONDUCTOR TO SERVICE GROUNDING POINT(S) (REFER TO DETAIL ON DRAWING #EO-02). INCLUDE (2) DOUBLE DUPLEX RECEPTACLES INSTALLED AT THIS TERMINAL BOARD SERVED FROM (2) 20A-120V-1Ø DEDICATED CIRCUITS. REFER TO COMMUNICATION RISER DIAGRAM ON DRAWING #EO-02 FOR ADDITIONAL INFORMATION.
- ④ ROUTE BRANCH CIRCUITING FOR RECEPTACLES AT THIS LOCATION VERTICALLY AT EACH FLOOR. PROVIDE HOMERUN AS SHOWN ON FOURTH FLOOR.

GENERAL POWER AND COMMUNICATION PLAN NOTES

- EXACT LOCATION OF MECHANICAL, PLUMBING, KITCHEN, FURNITURE SYSTEMS, OWNER FURNISHED EQUIPMENT, ETC. THAT REQUIRE ELECTRICAL CONNECTIONS ARE SHOWN ON THE MECHANICAL, PLUMBING, AND/OR ARCHITECTURAL DRAWINGS. COORDINATE EXACT LOCATIONS WITH RESPECTIVE CONTRACTORS AND/OR VENDORS PRIOR TO ANY ROUGH-INS.
- PRIOR TO ROUGH-IN, REVIEW AND COORDINATE WITH ALL OTHER TRADES' CONTRACT DOCUMENTS TO DETERMINE SPECIFIC MOUNTING LOCATIONS AND ELECTRICAL REQUIREMENTS (VOLTAGE, PHASE, KW, HP, CONNECTION TYPE, ETC.) FOR HVAC AND PLUMBING EQUIPMENT. COORDINATE EXACT MOUNTING LOCATIONS WITH THE SPECIFIC TRADE AND ARCHITECT.
- REFER TO WIRING SCHEDULE ON SHEET #EO.03A/B/C FOR 15A/20A RECEPTACLE BRANCH CIRCUITS FOR ALL CONDUCTOR SIZES TO ACCOUNT FOR VOLTAGE DROP.
- ALL WIRING SHALL BE IDENTIFIED BY PANELBOARD AND CIRCUIT NUMBER(S) IN ALL CABINETS, JUNCTION BOXES, WIRING TROUGHS, ENCLOSURES, SPLICE OR TERMINATION POINTS, ETC.
- A NEW TYPED PANELBOARD DIRECTORY CARD SHALL BE PROVIDED FOR ALL PANELS INSTALLED OR MODIFIED UNDER THIS CONTRACT. NEW DIRECTORY CARDS SHALL BE LOCATED ON THE INSIDE DOOR OF ASSOCIATED PANELS.

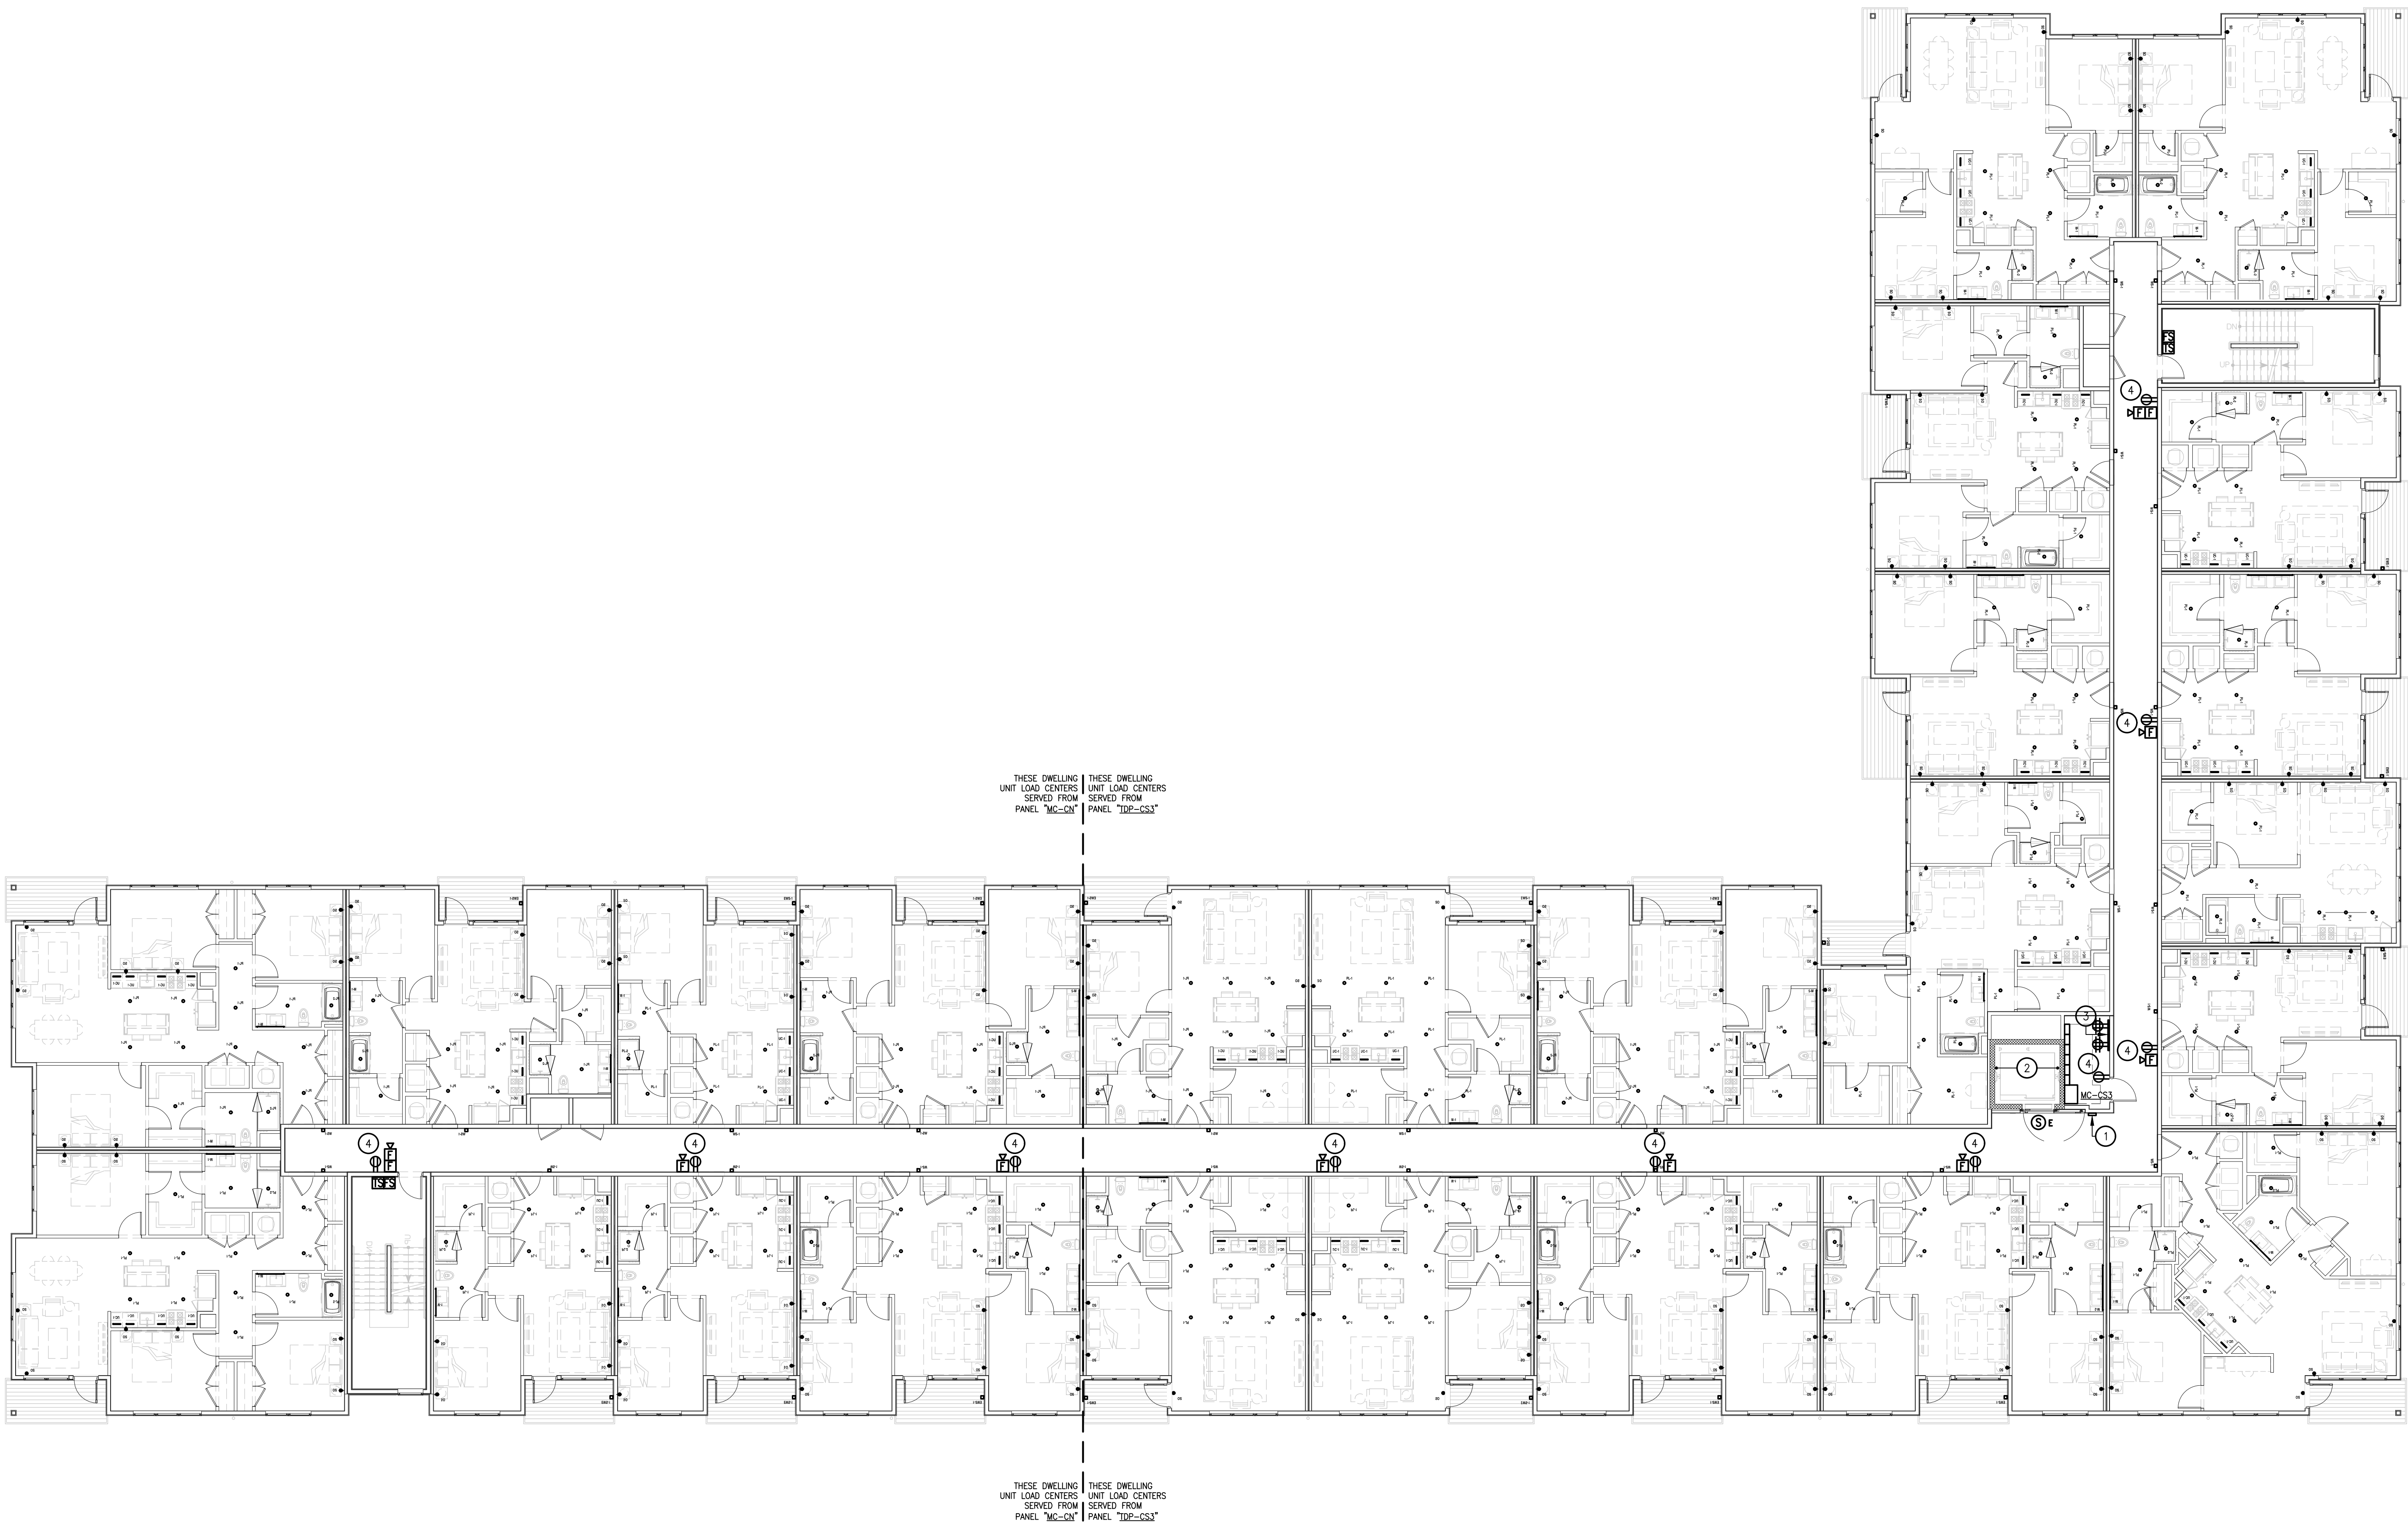

BUILDING C
THIRD FLOOR POWER PLAN
SCALE: 3/32" = 1'-0"

Seal

NOT FOR
CONSTRUCTION

Issue:	Date:	By:
SCHEMATIC DESIGN	01.07.26	BAC
DESIGN DEVELOPMENT	03.05.26	BAC

who
engineering

2012 West 25th Street, Suite 900
Cleveland, OH 44113
Phone: 216 227 8505

**OSU
AIRPORT WEST
BUILDING C**

3455 W. Dublin Granville Rd,
Columbus OH, 43235

Drawing Title
**THIRD FLOOR POWER
PLAN**

Date:	Project Number:
03.05.2026	24-065
Drawn by:	Drawing Number:
DJS	
Checked by:	
KDS	
Approved:	
GSS	


E2.03C

CODED NOTES

- ① LOCATION OF AREA OF RESCUE COMMUNICATION BASE STATION. REFER TO DIAGRAM ON DRAWING #EO-02.
- ② REFER TO ELEVATOR GENERAL INSTALLATION NOTES ON DRAWING #EO-03 FOR ALL ELEVATOR ROOM AND ELEVATOR PIT ELECTRICAL REQUIREMENTS.
- ③ PROVIDE A 4" x 4" x 3/4" THICK PLYWOOD BACKBOARD PAINTED WITH FIRE RETARDANT PAINT FOR MAIN COMMUNICATION TERMINAL BOARD (TELEPHONE, TELEVISION, ETC.). INCLUDE ALL WORK REQUIRED BY RESPECTIVE UTILITIES. PROVIDE A COPPER GROUNDING BUS AND #6 AWG GROUNDING CONDUCTOR TO SERVICE GROUNDING POINT(S) (REFER TO DETAIL ON DRAWING #EO-02). INCLUDE (2) DOUBLE DUPLEX RECEPTACLES INSTALLED AT THIS TERMINAL BOARD SERVED FROM (2) 20A-120V-1Ø DEDICATED CIRCUITS. REFER TO COMMUNICATION RISER DIAGRAM ON DRAWING #EO-02 FOR ADDITIONAL INFORMATION.
- ④ ROUTE BRANCH CIRCUITING FOR RECEPTACLES AT THIS LOCATION VERTICALLY AT EACH FLOOR. PROVIDE HOMERUN AS SHOWN ON FOURTH FLOOR.

GENERAL POWER AND COMMUNICATION PLAN NOTES

- EXACT LOCATION OF MECHANICAL, PLUMBING, KITCHEN, FURNITURE SYSTEMS, OWNER FURNISHED EQUIPMENT, ETC. THAT REQUIRE ELECTRICAL CONNECTIONS ARE SHOWN ON THE MECHANICAL, PLUMBING, AND/OR ARCHITECTURAL DRAWINGS. COORDINATE EXACT LOCATIONS WITH RESPECTIVE CONTRACTORS AND/OR VENDORS PRIOR TO ANY ROUGH-INS.
- PRIOR TO ROUGH-IN, REVIEW AND COORDINATE WITH ALL OTHER TRADES' CONTRACT DOCUMENTS TO DETERMINE SPECIFIC MOUNTING LOCATIONS AND ELECTRICAL REQUIREMENTS (VOLTAGE, PHASE, KW, HP, CONNECTION TYPE, ETC.) FOR HVAC AND PLUMBING EQUIPMENT. COORDINATE EXACT MOUNTING LOCATIONS WITH THE SPECIFIC TRADE AND ARCHITECT.
- REFER TO WIRING SCHEDULE ON SHEET #EO.03A/B/C FOR 15A/20A RECEPTACLE BRANCH CIRCUITS FOR ALL CONDUCTOR SIZES TO ACCOUNT FOR VOLTAGE DROP.
- ALL WIRING SHALL BE IDENTIFIED BY PANELBOARD AND CIRCUIT NUMBER(S) IN ALL CABINETS, JUNCTION BOXES, WIRING TROUGHS, ENCLOSURES, SPLICE OR TERMINATION POINTS, ETC.
- A NEW TYPED PANELBOARD DIRECTORY CARD SHALL BE PROVIDED FOR ALL PANELS INSTALLED OR MODIFIED UNDER THIS CONTRACT. NEW DIRECTORY CARDS SHALL BE LOCATED ON THE INSIDE DOOR OF ASSOCIATED PANELS.

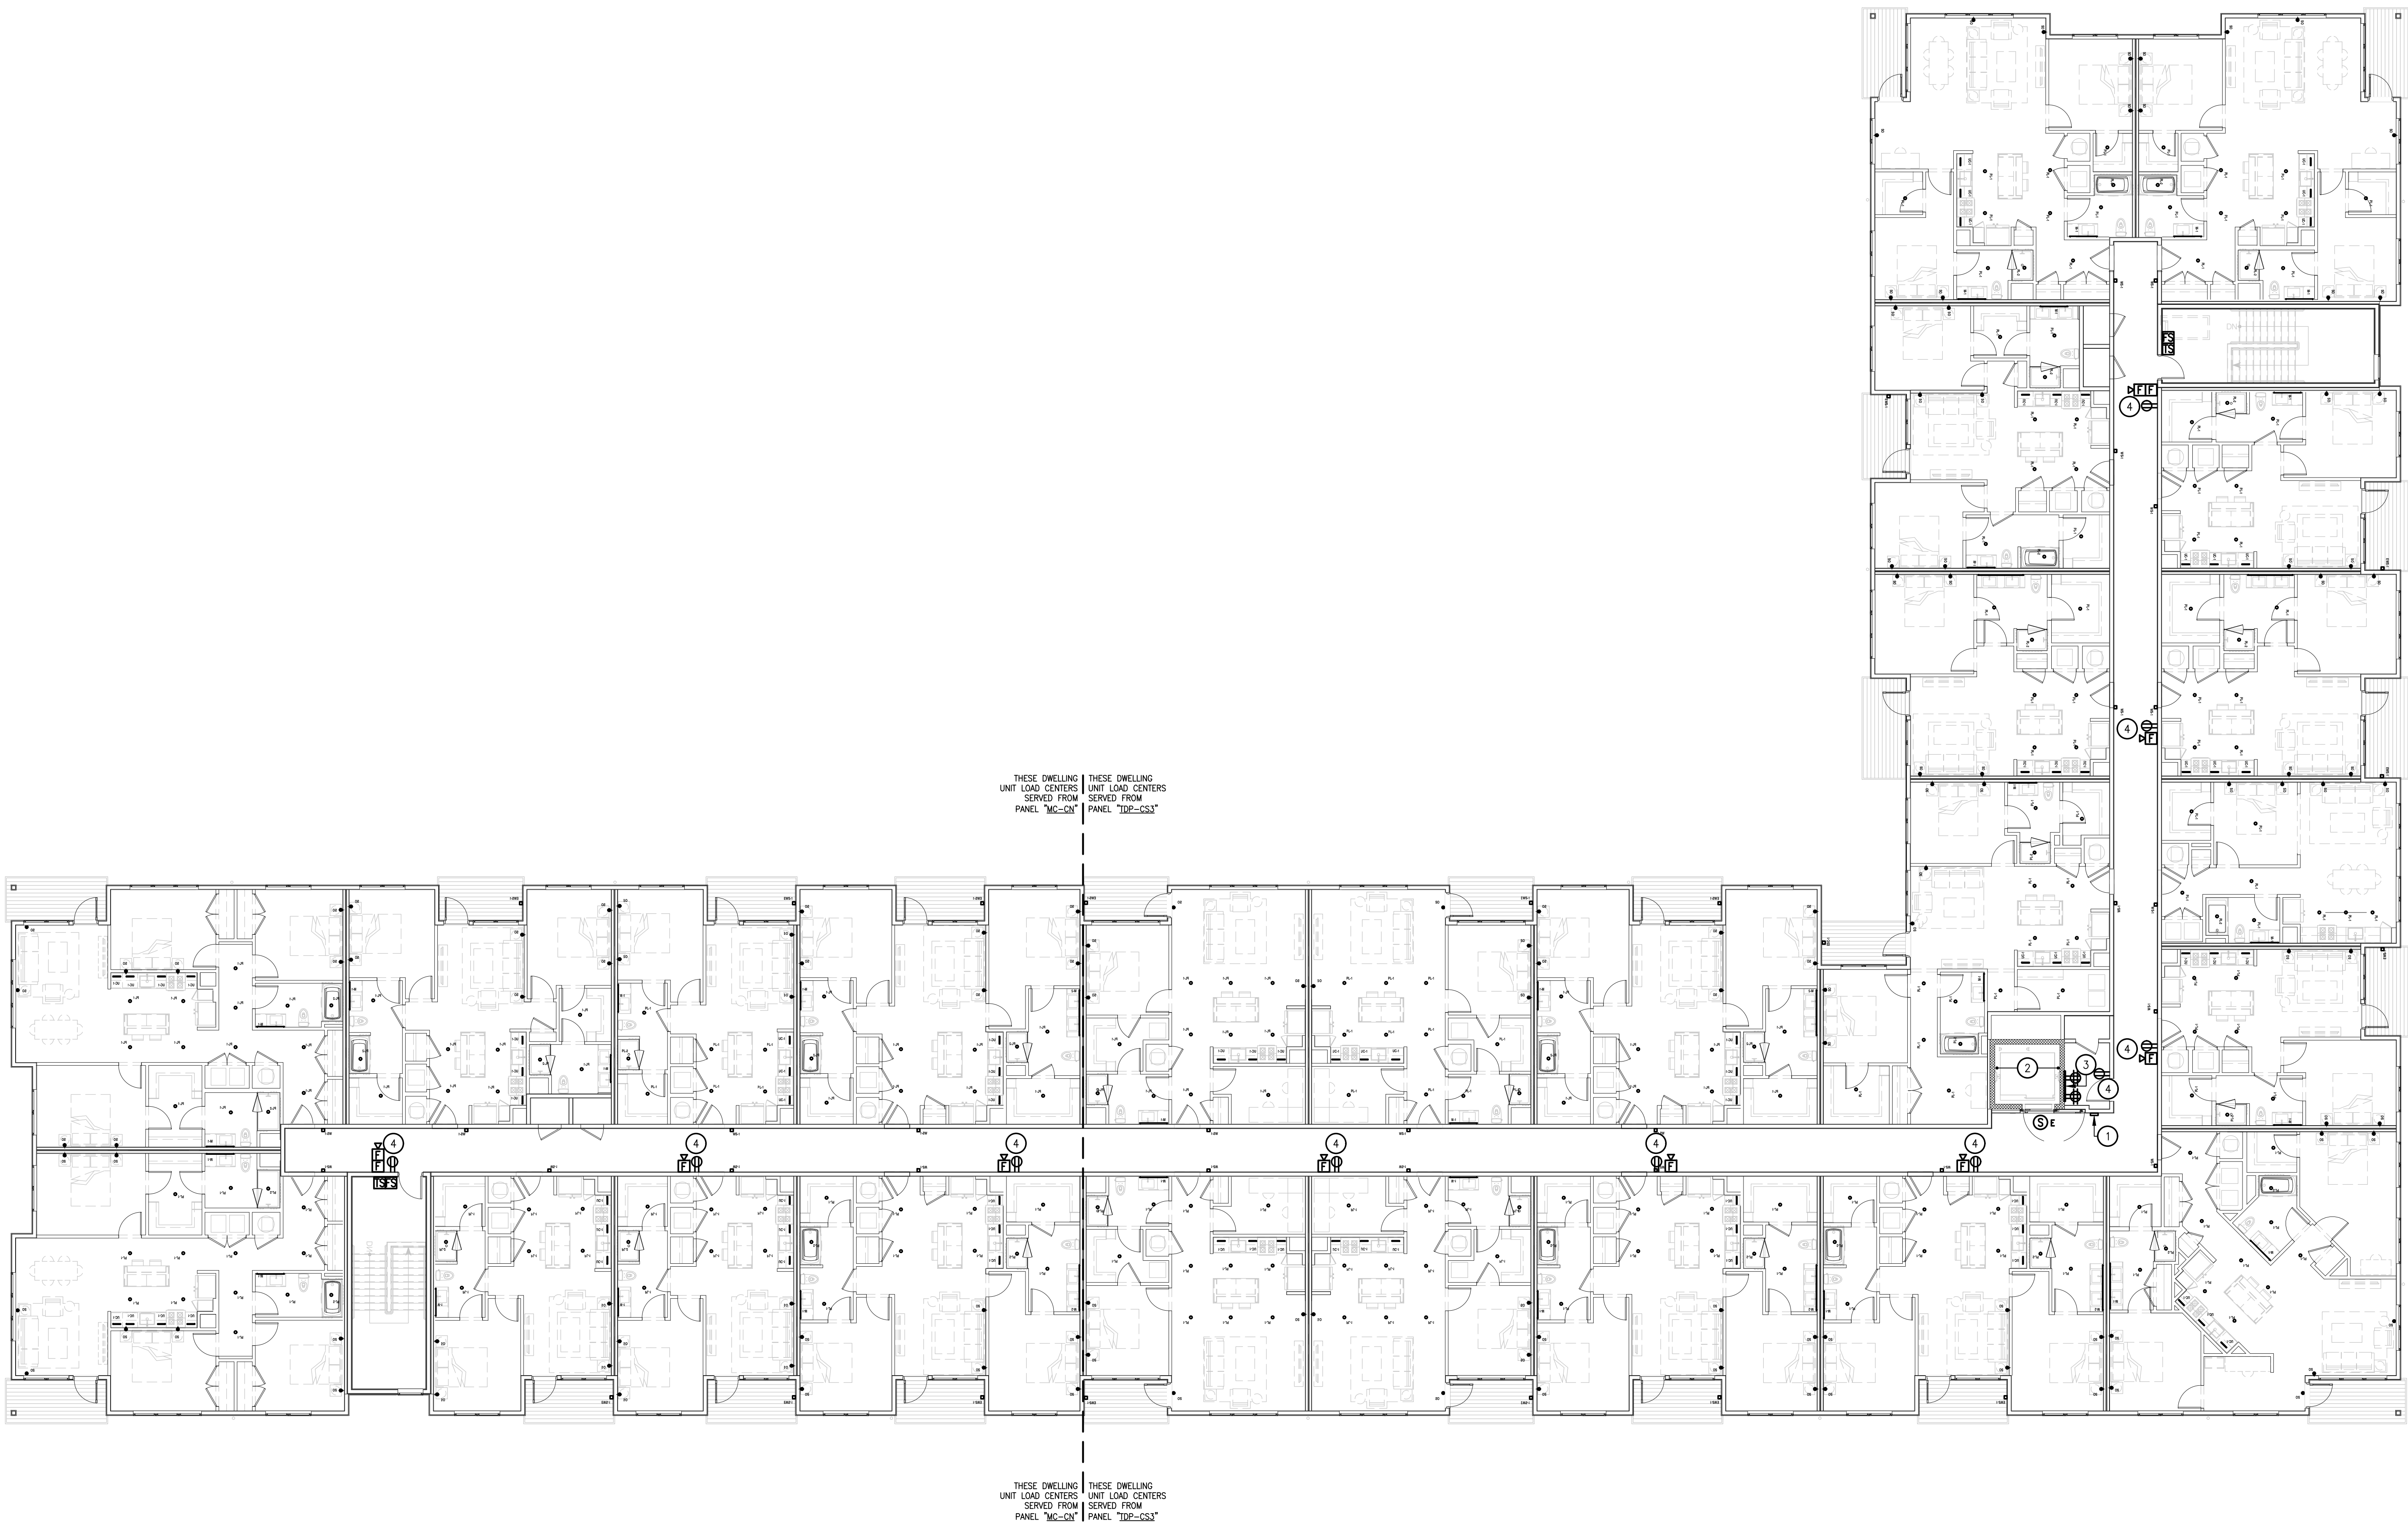

1
E2.04C
BUILDING C
FOURTH FLOOR POWER PLAN
SCALE: 3/32" = 1'-0"

Seal

NOT FOR
CONSTRUCTION

Issue:	Date:	By:
SCHEMATIC DESIGN	01.07.26	BAC
DESIGN DEVELOPMENT	03.05.26	BAC

whs
engineering

2012 West 25th Street, Suite 900
Cleveland, OH 44113
Phone: 216 227 8505

**OSU
AIRPORT WEST
BUILDING C**

3455 W. Dublin Granville Rd,
Columbus OH, 43235

Drawing Title

**FOURTH FLOOR POWER
PLAN**

Date

03.05.2026

Project Number

24-065

Drawn By

DJS

Drawing Number

Checked by

KDS

Approved

GSS


E2.04C

CODED NOTES

- ① DWELLING UNIT HEAT PUMPS TO BE POWERED FROM RESPECTIVE TENANT PANEL. REFER TO TYPICAL DWELLING UNIT APPLIANCE CONNECTION SCHEDULE ON SHEET #E3-00 FOR LOAD INFORMATION, CIRCUIT BREAKER, DISCONNECT, AND CONDUCTOR SIZING.

GENERAL POWER AND COMMUNICATION PLAN NOTES

- EXACT LOCATION OF MECHANICAL, PLUMBING, KITCHEN, FURNITURE SYSTEMS, OWNER FURNISHED EQUIPMENT, ETC. THAT REQUIRE ELECTRICAL CONNECTIONS ARE SHOWN ON THE MECHANICAL, PLUMBING, AND/OR ARCHITECTURAL DRAWINGS. COORDINATE EXACT LOCATIONS WITH RESPECTIVE CONTRACTORS AND/OR VENDORS PRIOR TO ANY ROUGH-INS.
- PRIOR TO ROUGH-IN, REVIEW AND COORDINATE WITH ALL OTHER TRADES' CONTRACT DOCUMENTS TO DETERMINE SPECIFIC MOUNTING LOCATIONS AND ELECTRICAL REQUIREMENTS (VOLTAGE, PHASE, KW, HP, CONNECTION TYPE, ETC.) FOR HVAC AND PLUMBING EQUIPMENT. COORDINATE EXACT MOUNTING LOCATIONS WITH THE SPECIFIC TRADE AND ARCHITECT.
- REFER TO WIRING SCHEDULE ON SHEET #E0.03A/B/C FOR 15A/20A RECEPTACLE BRANCH CIRCUITS FOR ALL CONDUCTOR SIZES TO ACCOUNT FOR VOLTAGE DROP.
- ALL WIRING SHALL BE IDENTIFIED BY PANELBOARD AND CIRCUIT NUMBER(S) IN ALL CABINETS, JUNCTION BOXES, WIRING TROUGHS, ENCLOSURES, SPLICE OR TERMINATION POINTS, ETC.
- A NEW TYPED PANELBOARD DIRECTORY CARD SHALL BE PROVIDED FOR ALL PANELS INSTALLED OR MODIFIED UNDER THIS CONTRACT. NEW DIRECTORY CARDS SHALL BE LOCATED ON THE INSIDE DOOR OF ASSOCIATED PANELS.

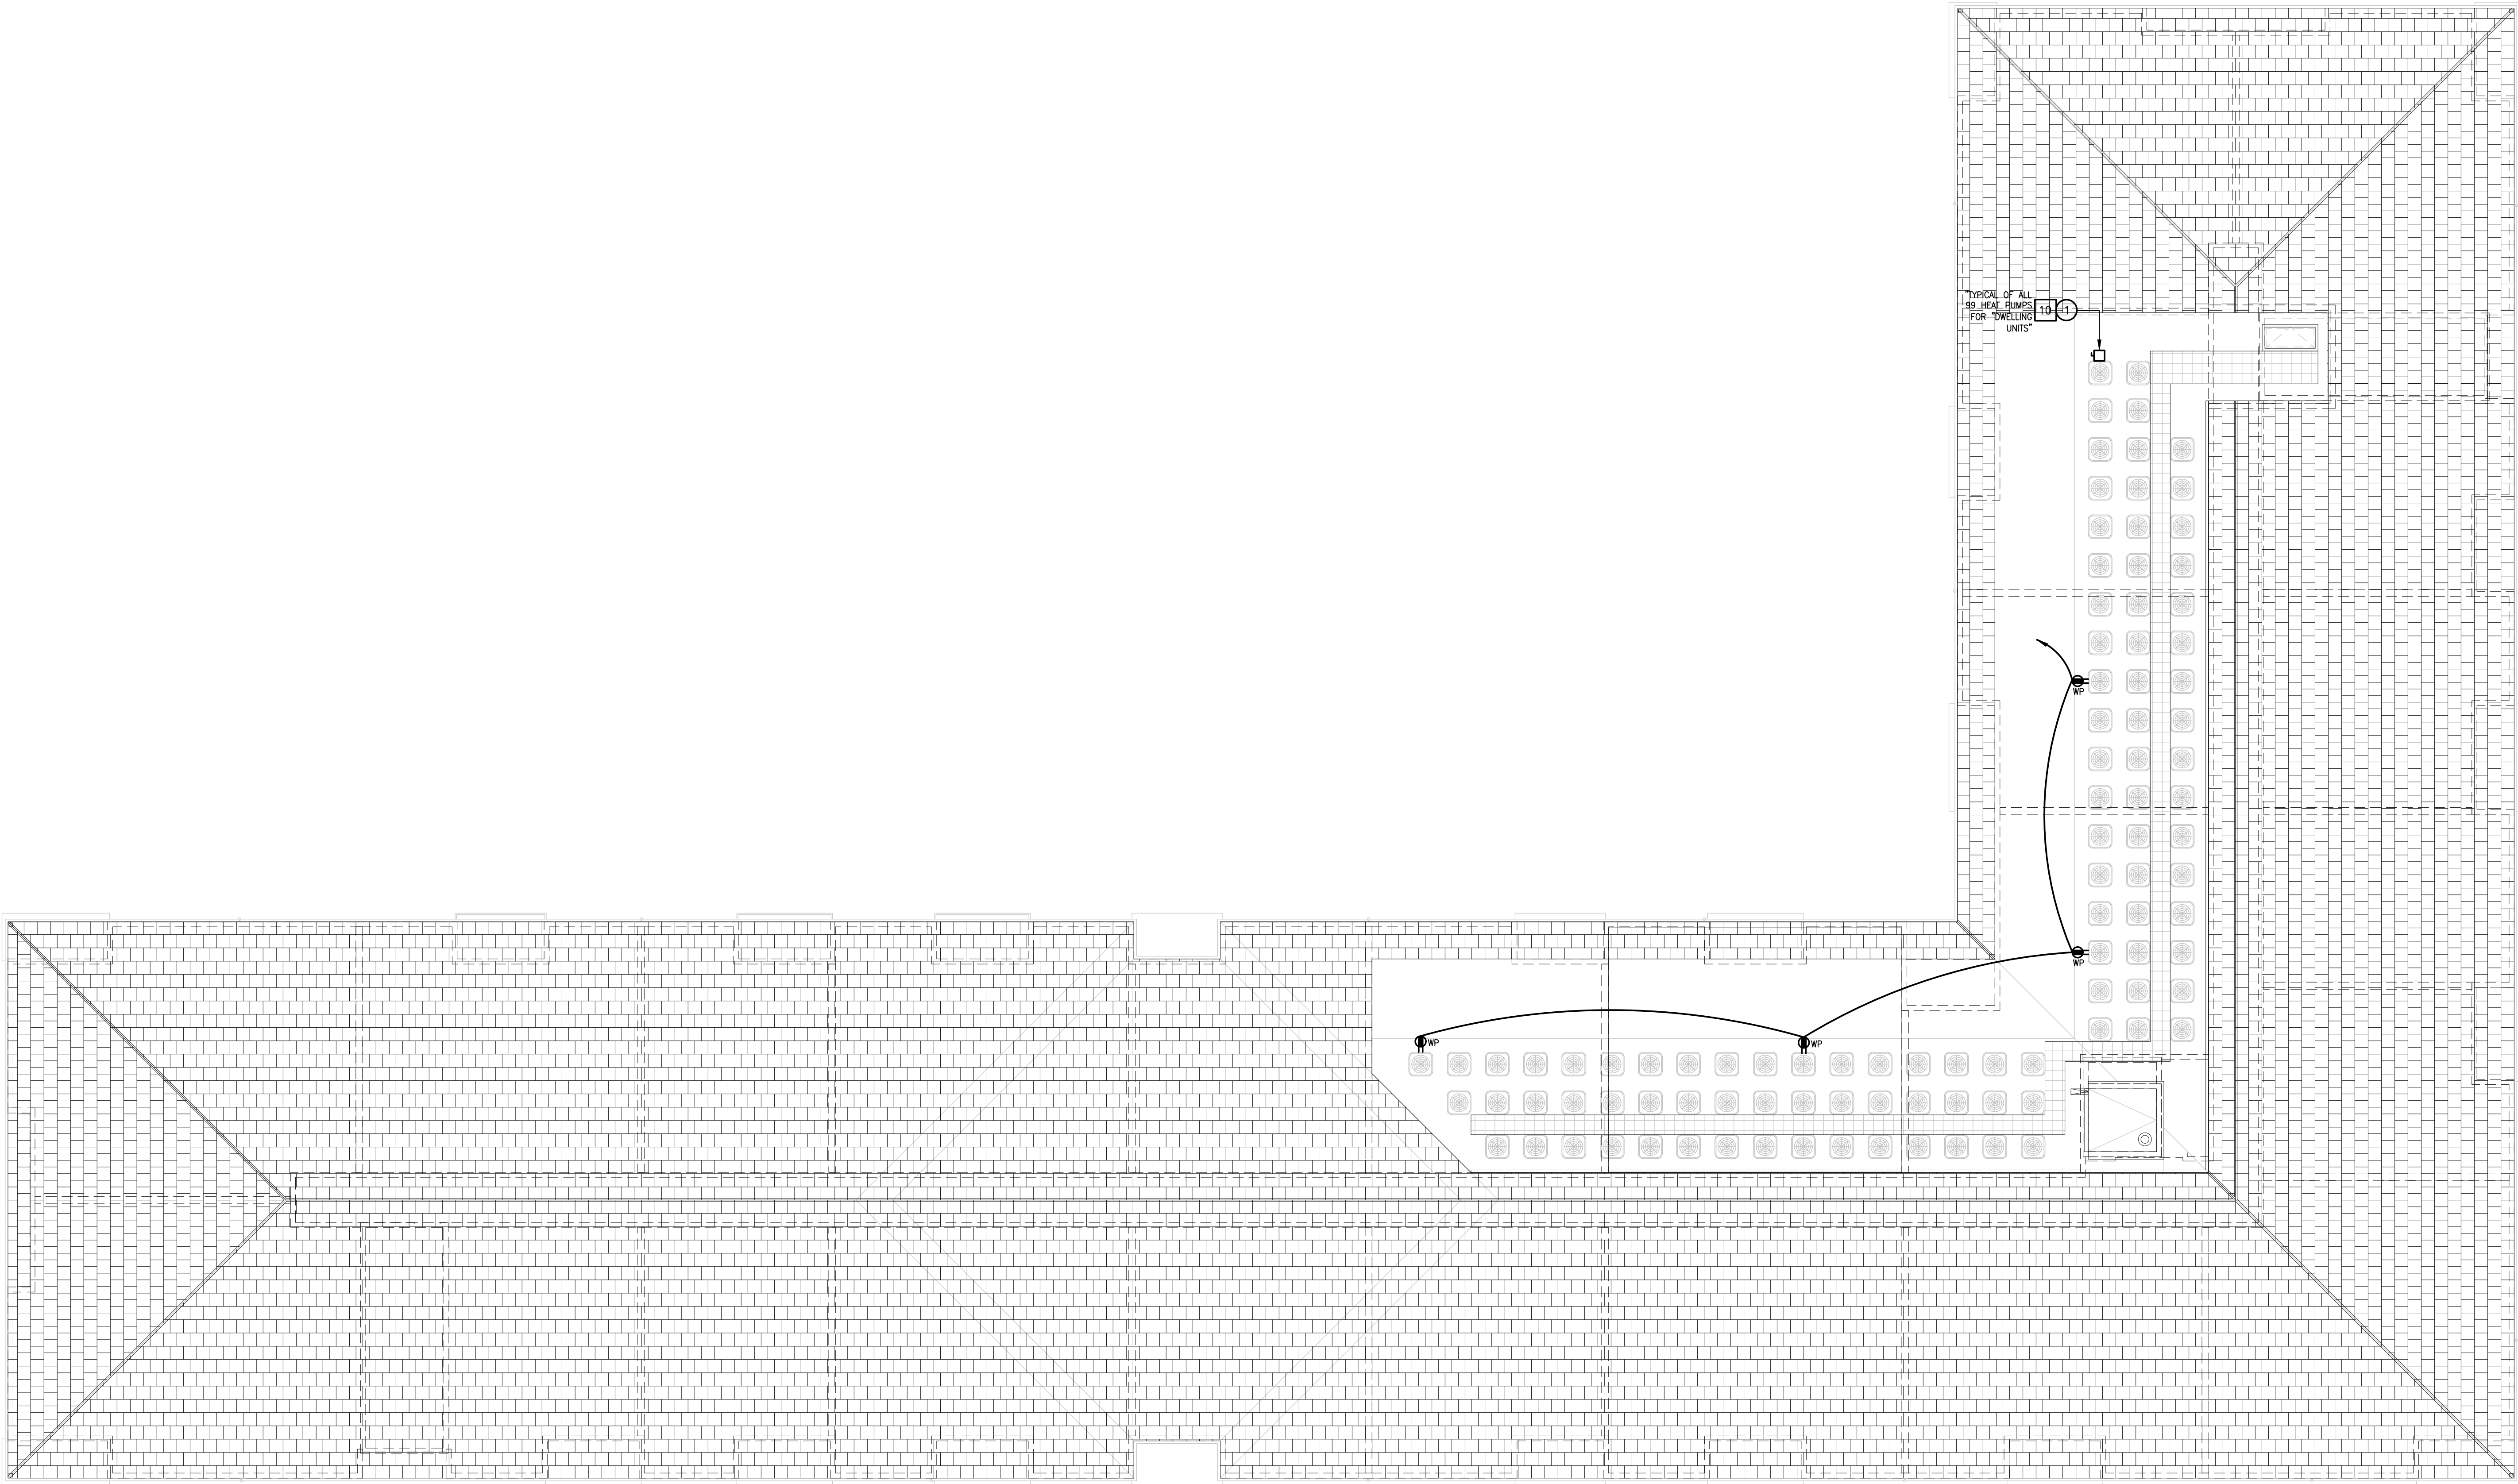

Seal

NOT FOR
CONSTRUCTION

Issue:	Date:	By:
SCHEMATIC DESIGN	01.07.26	BAC
DESIGN DEVELOPMENT	03.05.26	BAC

whs
engineering

2012 West 25th Street, Suite 900
Cleveland, OH 44113
Phone: 216 227 8505

**OSU
AIRPORT WEST
BUILDING C**

3455 W. Dublin Granville Rd,
Columbus OH, 43235

Drawing Title

**ROOF LEVEL POWER
PLAN**

Date: 03.05.2026	Project Number: 24-065
Drawn By: DJS	Drawing Number: E2.05C
Checked By: KDS	
Approved: GSS	

GENERAL "DWELLING UNIT" ELECTRICAL CONSTRUCTION NOTES

- A. EQUIPMENT AND MATERIALS USED ON THIS PROJECT SHALL BE NEW AND U.L. LABELED FOR THE APPLICATION.
- B. WORK SHALL BE INSTALLED IN ACCORDANCE WITH ALL APPLICABLE PROVISIONS OF LOCAL AND STATE CODES AS WELL AS THE CURRENT EDITION OF THE NATIONAL ELECTRICAL CODE (NEC), AS INTERPRETED BY THE LOCAL AUTHORITY HAVING JURISDICTION.
- C. MATERIAL OR LABOR WHICH IS NOT INDICATED ON THE DRAWINGS OR SPECIFICATION BUT WHICH IS OBVIOUSLY NECESSARY TO COMPLETE THE WORK SHALL BE PROVIDED. DRAWINGS AND SPECIFICATIONS ARE TO BE CONSIDERED AS SUPPLEMENTING EACH OTHER.
- D. VISIT THE SITE OF THE WORK AND BECOME FAMILIAR WITH CONDITIONS AFFECTING THE INSTALLATION. SUBMISSION OF A PROPOSAL SHALL PRESUPPOSE KNOWLEDGE OF SUCH CONDITIONS AND NO ADDITIONAL COMPENSATION SHALL BE ALLOWED WHERE EXTRA LABOR OR MATERIALS ARE REQUIRED BECAUSE OF IGNORANCE OF THESE CONDITIONS.
- E. WHERE LIGHT SWITCHES ARE SHOWN ADJACENT TO ONE ANOTHER, THEY SHALL BE GROUPED TOGETHER INTO A 2, 3, OR 4 GANG DEVICE BOX WITH COMMON COVERPLATE.
- F. BACK BOXES IN DEMISING WALLS SHALL NOT BE ROUGHED-IN BACK TO BACK IN THE SAME STUD SPACE. PROVIDE FIRE-STOPPING AS REQUIRED TO MAINTAIN FIRE RATING.
- G. ELECTRICAL BOXES, ELECTRICAL EQUIPMENT, ETC. MUST BE FIRESTOPPED UNDER THE FOLLOWING CONDITIONS: BOXES LARGER THAN 16 SQUARE INCHES, IF HORIZONTAL SPACING BETWEEN BOXES IS LESS THAN 24 INCHES. WHEN MULTIPLE BOXES ARE LOCATED IN ONE STUD CAVITY OR IF THE AGGREGATE OF ALL BOXES EXCEEDS 100 SQUARE INCHES PER 100 SQUARE FEET. REFER TO LISTED SYSTEM DETAILS AND APPLICABLE LOCAL BUILDING CODE REQUIREMENTS.
- H. WHERE ELECTRICAL EQUIPMENT, OUTLET BOXES, ETC. ARE INSTALLED IN A FIRE RATED ASSEMBLY AND AS REQUIRED UNDER THE PARAMETERS LISTED ABOVE, FIRE (PUTTY) PADS SHALL BE PROVIDED TO MAINTAIN THE INTEGRITY OF THE FIRE RATED ASSEMBLY.
- I. WHEN ELECTRICAL EQUIPMENT, OUTLET BOXES, ETC. ARE INSTALLED IN A STUD PARTITION WHERE ADJACENT ROOMS ARE SIMILAR, THE OUTLETS SHALL BE STAGGERED AND FIRE RATED (PUTTY) PADS SHALL ALSO BE INSTALLED.
- J. FIRE RATED (PUTTY) PADS SHALL BE 3M "FIRE BARRIER MOLDABLE PUTTY PADS MPP+", FIRE RATED PRODUCTS SPECIALTIES CORPORATION TYPE "FRPS" ENCLOSURES, OR APPROVED EQUAL PRIOR TO PLACING BASE BID PRICE.
- K. THE ELECTRICAL CONTRACTOR IS RESPONSIBLE FOR MAINTAINING THE FIRE RATING OF ALL CEILINGS, STRUCTURES, ETC. IN COMPLIANCE WITH ALL STANDARDS. WHERE BACK BOXES ARE REQUIRED TO BE INSTALLED TO SERVE LIGHT FIXTURES IN FIRE RATED CEILINGS, FIRE (PUTTY) PADS SHALL BE PROVIDED.
- L. REFER TO ARCHITECTURAL ELEVATIONS FOR MOUNTING LOCATION AND HEIGHT OF ALL WIRING DEVICES.
- M. COORDINATE THE EXACT LOCATION OF ALL RECEPTACLES AT CABINET LOCATIONS WITH G.C. CUT AND PATCH AS DIRECTED BY THE G.C.
- N. ALL DEVICES SHALL BE RESIDENTIAL GRADE, 15/20 AMP DEVICES. RECEPTACLES SHALL BE TAMPER RESISTANT TYPE IN COMPLIANCE WITH N.E.C. #406.12.
- O. SMOKE DETECTORS MUST BE INSTALLED FREE OF DUST OR ANY OTHER CONTAMINATION. LOCATE A MINIMUM OF 3'-0" FROM ALL SUPPLY AIR DIFFUSERS. LOCATE A MINIMUM OF 1'-0" FROM ANY PART OF ANY LIGHTING FIXTURES. DO NOT LOCATE ABOVE PENDANT MOUNTED OR INDIRECT LIGHTING FIXTURES. DO NOT LOCATE ABOVE CEILING FANS.
- P. IN ALL SINGLE, OR, MULTI-FAMILY DWELLING UNITS, RECEPTACLES SHALL BE LOCATED AND INSTALLED IN ACCORDANCE WITH THE CURRENT EDITION OF THE N.E.C. ELECTRICAL EQUIPMENT, DEVICES, ETC. SHALL BE INSTALLED AND SPACED AS DIRECTED BY THE N.E.C. WITH SPECIFIC ATTENTION TO ARTICLE #210.52(A) THROUGH #210.52(I).
- Q. ALL PENETRATIONS IN FIRE RATED FLOORS, SHAFTS AND WALLS SHALL BE FIRE STOPPED. THE INSTALLATION OF FIRE STOPPING MATERIALS SHALL CONFORM TO THE LATEST FIRE RESISTANCE DIRECTORY AS PUBLISHED BY U.L.
- U. ALL RECEPTACLES SERVING KITCHEN COUNTER TOP SURFACES SHALL BE G.F.C.I. PROTECTED IN ACCORDANCE WITH N.E.C. ARTICLE #210.8(A)(6).
- V. ALL RECEPTACLES SHALL LOCATED WITHIN 6'-0" OF THE OUTSIDE OF ALL SINKS, SHOWER STALLS, AND, BATH TUBS SHALL BE G.F.C.I. PROTECTED IN ACCORDANCE WITH N.E.C. ARTICLE #210.8(A)(7).
- W. WHERE G.F.C.I. DEVICES ARE INSTALLED TO SERVE LARGE APPLIANCES, OR, APPLIANCES BELOW COUNTERTOP SURFACES, THE G.F.C.I. DEVICE SHALL BE READILY ACCESSIBLE AS REQUIRED BY N.E.C. ARTICLE #422.5 AND AS DEFINED BY N.E.C. ARTICLE #100. PROVIDE G.F.C.I. TYPE CIRCUIT BREAKERS WHERE APPLICABLE. PROVIDE PROPER IDENTIFICATION AT RELATED DEVICE LOCATIONS INDICATING "G.F.C.I. PROTECTED".
- X. PROVIDE ARC-FAULT PROTECTION FOR APPLICABLE BRANCH CIRCUITS IN ACCORDANCE WITH N.E.C. ARTICLE #210.12(A).

TYPICAL UNIT APPLIANCE/EQUIPMENT CONNECTION SCHEDULE									
·	APPLIANCE/EQUIPMENT DESCRIPTION	VOLTAGE/ PHASE	KW	CONNECTION TYPE			WIRE/CONDUIT SIZE	NOTE	S
				NEMA TYPE	DISCONNECT/SWITCH	HEIGHT			
1	REFRIGERATOR	120V-1ø	0.600	5-20R	—	54"	2ø12, 1ø12(G), 3/4"C.	1	
2	ELECTRIC RANGE/OVEN	120/ 208V-1ø	8.000	14-50R	—	VERIFY	3ø6, 1ø10(G), 1"C.	1	
3A	RANGE HOOD (ADA UNITS)	120V-1ø	0.480		DIRECT	VERIFY	2ø12, 1ø12(G), 3/4"C.	1,4	
3B	RANGE HOOD/MICROWAVE	120V-1ø	1.680	5-20R	—	VERIFY	2ø12, 1ø12(G), 3/4"C.	1	
4	DISHWASHER	120V-1ø			—	SEE NOTE 2	2ø12, 1ø12(G), 3/4"C.	1,2	
5	DISPOSER	120V-1ø	1.200	5-20R	—				
6	WASHING MACHINE/LAUNDRY	120V-1ø	1.500	5-20R	—	42"	2ø12, 1ø12(G), 3/4"C.	1	
7	ELECTRIC DRYER	120/ 208V-1ø	5.000	14-30R	—	42"	3ø10, 1ø10(G), 3/4"C.	1	
8	ELECTRIC WATER HEATER	208V-1ø	4.500	—	30A-2P, NEMA 1	AT UNIT	2ø10, 1ø10(G), 3/4"C.	1,6	
9A	1.5 TON AIR HANDLER	208V-1ø	4.784	—	30A-2P, NEMA 1	AT UNIT	2ø10, 1ø10(G), 3/4"C.	1,6	
9B	2.5 TON AIR HANDLER	208V-1ø	5.824	—	30A-2P, NEMA 1	AT UNIT	2ø10, 1ø10(G), 3/4"C.	1,6	
9C	2.5 TON AIR HANDLER	208V-1ø	8.528	—	60A-2P, NEMA 1	AT UNIT	2ø6, 1ø10(G), 1"C.	1,6	
10A	1.5 TON ROOFTOP HEAT PUMP	208V-1ø	2.080	—	30A-2P, NEMA 3R	AT UNIT	2ø10, 1ø10(G), 3/4"C.	1,5	
10B	2 TON ROOFTOP HEAT PUMP	208V-1ø	2.704	—	30A-2P, NEMA 3R	AT UNIT	2ø10, 1ø10(G), 3/4"C.	1,5	
10C	2.5 TON ROOFTOP HEAT PUMP	208V-1ø	3.328	—	30A-2P, NEMA 3R	AT UNIT	2ø8, 1ø10(G), 3/4"C.	1,5	
11	EXHAUST FAN	120V-1ø	0.055	—	INTEGRAL	CEILING	2ø12, 1ø12(G), 3/4"C.	1,3	

APPLIANCE/EQUIPMENT CONNECTION SCHEDULE NOTES:

- VERIFY ALL EQUIPMENT SPECIFICATIONS (VOLTAGE, CONNECTION, ETC.) WITH OWNER AND/OR ARCHITECT PRIOR TO PLACING PURCHASE ORDER FOR DEVICES AND ROUGH-IN. VERIFY THE EXACT MOUNTING HEIGHT WITH ARCHITECTURAL ELEVATIONS, MILLWORK, ETC. PRIOR TO ROUGH-IN.
- PROVIDE A DUPLEX RECEPTACLE TO SERVE DISHWASHER AND DISPOSER PROTECTED BY AN UPSTREAM GFCI TYPE CIRCUIT BREAKER. COORDINATE LOCATION OF DEVICE IN MILLWORK WITH ARCHITECT/G.C. AT ISLAND LOCATIONS, INSTALL AN AIR PUSH BUTTON TYPE BUTTON (PROVIDED BY P.C.) FOR CONTROL OF DISHWASHER. INCLUDE ALL COSTS OF CORE DRILLING MILLWORK/SINK TO INSTALL PUSH BUTTON. ENSURE INSTALLED BUTTON ALLOWS FOR DISHWASHER TO BE SERVED BY THE SAME RECEPTACLE. AT NON-ISLAND KITCHEN COUNTER LOCATIONS, PROVIDE A SINGLE POLE SWITCH AT THE KITCHEN BACKSPLASH (FINAL LOCATION BY ARCHITECT). SPLIT-WIRE THE RECEPTACLE AND WIRE SUCH THE SWITCH ONLY CONTROLS THE TOP OUTLET. **ALL FINAL DEVICE LOCATIONS SHALL BE ADA COMPLIANT IN ADA COMPLIANT UNITS.**
- CONNECT TO INTEGRAL DISCONNECT SWITCH AND CONNECT TO APARTMENT UNIT LIGHTING CIRCUIT. VERIFY EXACT REQUIREMENTS WITH EQUIPMENT. WIRE SUCH THAT EXHAUST FAN RECEIVES CONSTANT LINE VOLTAGE POWER AHEAD OF ALL SWITCHING AND CONTROL. **REFER TO DETAIL ON THIS SHEET.**
- PROVIDE A REDUNDANT (3-WAY) SWITCH IN ADA UNITS FOR CONTROL OF RANGE HOOD. SWITCH SHALL BE LOCATED IN ADA-COMPLIANT LOCATION. MODIFY RANGE HOOD WIRING AS REQUIRED (REFER TO HOOD UNIT WIRING DIAGRAM) FOR ADDITIONAL CONTROL LOCATION.
- BRANCH CIRCUITING SIZED TO ACCOUNT FOR VOLTAGE DROP.
- INSTALL DISCONNECT IN CLOSET SUCH THAT NEC #110.26 WORKING CLEARANCE IS MAINTAINED.

DWELLING UNIT LUMINAIRE SCHEDULE

TYPE	LAMP	WATTAGE	VOLTAGE	DIMMING TYPE	DESCRIPTION	CATALOG NUMBER	EQUIVALENT MANUFACTURER/REMARKS
M-1	—	—	120	—	LED MIRROR LIGHT USED IN BATHROOMS.	—	—
PL-1	—	—	120	—	LED PENDANT LIGHT USED THROUGHOUT THE UNITS.	—	—
PL-2	—	—	120	—	LED PENDANT USED OVER BATHROOM SHOWERS.	—	—
UC-1	—	—	120	—	LED UNDERCOUNTER LIGHT USED IN KITCHEN AREA.	—	—

LUMINAIRE SCHEDULE GENERAL NOTES:

- VERIFY ALL LUMINAIRE COLORS, TRIMS, LENGTHS, ETC. WITH THE **ARCHITECT/OWNER/DEVELOPER/DESIGNER** PRIOR TO PLACING FINAL PURCHASE ORDERS. SUBMISSION OF SHOP DRAWINGS WILL BE INTERPRETED AS HAVING BEEN COORDINATED WITH THE AFOREMENTIONED PARTIES.
- PROVIDE ALL LENGTHS, FEEDS, ACCESSORIES, CONNECTORS, WIRING, POWER SUPPLIES, DRIVERS, ETC. FOR A COMPLETE INSTALLATION. VERIFY THE COMPLETE BILL OF MATERIAL WITH MANUFACTURER'S REPRESENTATIVE AND ENSURE ALL EQUIPMENT IS INCLUDED IN BID PRICE. COORDINATE INSTALLATION WITH ARCHITECTURAL DETAILS.
- VERIFY FINAL LUMINAIRE LOCATIONS WITH OTHER CEILING MOUNTED EQUIPMENT SUCH AS DIFFUSERS, FIRE ALARM DEVICES, SPEAKERS, ETC., WITH ARCHITECTURAL REFLECTED CEILING PLANS.
- VERIFY EXACT MOUNTING HEIGHT AND LOCATIONS OF ALL WALL MOUNTED AND PENDANT MOUNTED LUMINAIRES WITH ARCHITECTURAL PLANS AND ELEVATIONS PRIOR TO ROUGH-IN.
- ANY PROPOSED ALTERNATE LUMINAIRES SHALL BE APPROVED BY THE **ARCHITECT/OWNER/DEVELOPER/DESIGNER** PRIOR TO FINAL BID PRICING.
- SHOULD THE CONTRACTOR PROPOSE TO FURNISH MATERIALS, EQUIPMENT, AND DEVICES, OTHER THAN THOSE SPECIFIED AND LISTED, THE CONTRACTOR SHALL SUBMIT A WRITTEN REQUEST FOR SUBSTITUTIONS, TO THE ENGINEER AT LEAST TEN (10) BUSINESS DAYS PRIOR TO BID OPENING. THE REQUEST SHALL BE AN ALTERNATE TO THE ORIGINAL BID AND SHALL INCLUDE A COMPLETE SPECIFICATIONS CUT SHEET SUBMITTAL AS OUTLINED IN THE SPECIFICATIONS, COMPLETE WITH DESCRIPTIVE (MANUFACTURER, BRAND NAME, CATALOG NUMBER, ETC.) AND TECHNICAL DATA FOR ALL ITEMS. INDICATE ANY ADDITIONS OR DEDUCTIONS TO THE CONTRACT PRICE WITH THE SUBSTITUTION SUBMITTAL AND ON THE BID FORM.
- ANY FINAL SELECTED/INSTALLED LIGHT FIXTURES WITHOUT A SPECIFICATION (OR TO BE SPECIFIED LATER BY **ARCHITECT/OWNER/DEVELOPER/DESIGNER**) LISTED IN THIS SCHEDULE SHALL NOT EXCEED THE WATTAGE LISTED, SHALL NOT HAVE A LOWERED DELIVERED LUMENS (IF LISTED), AND SHALL MATCH THE COLOR TEMPERATURE (IF LISTED).

TYPICAL DWELLING UNIT PANEL SCHEDULE									
NAME: TP1		VOLTAGE: 120/ 208 -1ø-3W							
MINIMUM KAIC: 10		TYPE: FLUSH MOUNTED							
MCR: 125A MLO		KWD: SEE ADJACENT CALC.							
CKT	DESCRIPTION	C/B	ø	C/B	DESCRIPTION	CKT			
A/G	1 SMALL APPLIANCE REC.	20/1	A	20/1	REFRIGERATOR	2	A/G		
A/G	3 SMALL APPLIANCE REC.	20/1	B	50/2	ELECTRIC RANGE	4	G2		
A	5 LIVING REC.	20/1	A			6			
G	7 BATHROOM REC.	20/1	B	20/1	RANGE HOOD/MICRO.	8	A/G		
A	9 LIGHTING/S.D.	20/1	A	20/1	DISHWASHER/DISPOSER	10	A/G		
A	11 BEDROOM REC.	20/1	B	20/1	WASHING MACHINE	12	A/G		
13	SPACE	—	A						
15	SPACE	—	B	30/2	ELECTRIC DRYER	14	G2		
17						16			
19						18			
	SURGE PROTECTION	—	A	30/2	ELECTRIC WATER HEATER	20			
			B			22			
21						24			
23	AIR HANDLER	25/2	A	15/2	ROOFTOP HEAT PUMP				

TYPICAL DWELLING UNIT PANEL SCHEDULE NOTES:

Δ: PROVIDE AN ARC-FAULT CIRCUIT INTERRUPTER (AFCI) TYPE CIRCUIT BREAKER FOR THIS BRANCH CIRCUIT.

⊘: PROVIDE GROUND-FAULT CIRCUIT INTERRUPTER (GFCI) PROTECTION FOR THIS BRANCH CIRCUIT. PROVIDE A GFCI-TYPE CIRCUIT BREAKER IF GFCI-TYPE RECEPTACLES/DEVICES ARE NOT PROVIDED DOWNSTREAM ON THIS BRANCH CIRCUIT.

⊘2: PROVIDE A GROUND-FAULT CIRCUIT INTERRUPTER (GFCI) TYPE CIRCUIT BREAKER FOR THIS BRANCH CIRCUIT.

TYPICAL DWELLING UNIT PANEL SCHEDULE									
NAME: TP2		VOLTAGE: 120/ 208 -1ø-3W							
MINIMUM KAIC: 10		TYPE: FLUSH MOUNTED							
MCR: 125A MLO		KWD: SEE ADJACENT CALC.							
CKT	DESCRIPTION	C/B	ø	C/B	DESCRIPTION	CKT			
A/G	1 SMALL APPLIANCE REC.	20/1	A	20/1	REFRIGERATOR	2	A/G		
A/G	3 SMALL APPLIANCE REC.	20/1	B	50/2	ELECTRIC RANGE	4	G2		
A	5 LIVING REC.	20/1	A			6			
G	7 BATHROOM REC.	20/1	B	20/1	RANGE HOOD/MICRO.	8	A/G		
A	9 LIGHTING/S.D.	20/1	A	20/1	DISHWASHER/DISPOSER	10	A/G		
A	11 BEDROOM REC.	20/1	B	20/1	WASHING MACHINE	12	A/G		
A	13 BEDROOM REC.	20/1	A	30/2	ELECTRIC DRYER	14	G2		
G	15 BATHROOM REC.	20/1	B			16			
17			A	30/2	ELECTRIC WATER HEATER	18			
19			B			20			
	SURGE PROTECTION	—	A	30/2	ELECTRIC WATER HEATER	22			
			B			24			
21									
23	AIR HANDLER	30/2	A	20/2	ROOFTOP HEAT PUMP				

TYPICAL DWELLING UNIT PANEL SCHEDULE NOTES:

Δ: PROVIDE AN ARC-FAULT CIRCUIT INTERRUPTER (AFCI) TYPE CIRCUIT BREAKER FOR THIS BRANCH CIRCUIT.

⊘: PROVIDE GROUND-FAULT CIRCUIT INTERRUPTER (GFCI) PROTECTION FOR THIS BRANCH CIRCUIT. PROVIDE A GFCI-TYPE CIRCUIT BREAKER IF GFCI-TYPE RECEPTACLES/DEVICES ARE NOT PROVIDED DOWNSTREAM ON THIS BRANCH CIRCUIT.

⊘2: PROVIDE A GROUND-FAULT CIRCUIT INTERRUPTER (GFCI) TYPE CIRCUIT BREAKER FOR THIS BRANCH CIRCUIT.


TYPICAL DWELLING UNIT PANEL SCHEDULE									
NAME: TP3		VOLTAGE: 120/ 208 -1ø-3W							
MINIMUM KAIC: 10		TYPE: FLUSH MOUNTED							
MCR: 150A MLO		KWD: SEE ADJACENT CALC.							
CKT	DESCRIPTION	C/B	ø	C/B	DESCRIPTION	CKT			
A/G	1 SMALL APPLIANCE REC.	20/1	A	20/1	REFRIGERATOR	2	A/G		
A/G	3 SMALL APPLIANCE REC.	20/1	B	50/2	ELECTRIC RANGE	4	G2		
A	5 LIVING REC.	20/1	A			6			
G	7 BATHROOM REC.	20/1	B	20/1	RANGE HOOD/MICRO.	8	A/G		
A	9 LIGHTING/S.D.	20/1	A	20/1	DISHWASHER/DISPOSER	10	A/G		
A	11 BEDROOM REC.	20/1	B	20/1	WASHING MACHINE	12	A/G		
A	13 BEDROOM REC.	20/1	A	30/2	ELECTRIC DRYER	14	G2		
G	15 BATHROOM REC.	20/1	B			16			
17			A	30/2	ELECTRIC WATER HEATER	18			
19			B			20			
21						22			
23	INTERIOR AIR HANDLER	45/2	A	25/2	ROOFTOP HEAT PUMP	24			
A	25 BEDROOM REC.	20/1	A	—	SPACE	26			
A	27 SPACE	—	B	—	SPACE	28			

TYPICAL DWELLING UNIT PANEL SCHEDULE NOTES:

Δ: PROVIDE AN ARC-FAULT CIRCUIT INTERRUPTER (AFCI) TYPE CIRCUIT BREAKER FOR THIS BRANCH CIRCUIT.

⊘: PROVIDE GROUND-FAULT CIRCUIT INTERRUPTER (GFCI) PROTECTION FOR THIS BRANCH CIRCUIT. PROVIDE A GFCI-TYPE CIRCUIT BREAKER IF GFCI-TYPE RECEPTACLES/DEVICES ARE NOT PROVIDED DOWNSTREAM ON THIS BRANCH CIRCUIT.

⊘2: PROVIDE A GROUND-FAULT CIRCUIT INTERRUPTER (GFCI) TYPE CIRCUIT BREAKER FOR THIS BRANCH CIRCUIT.

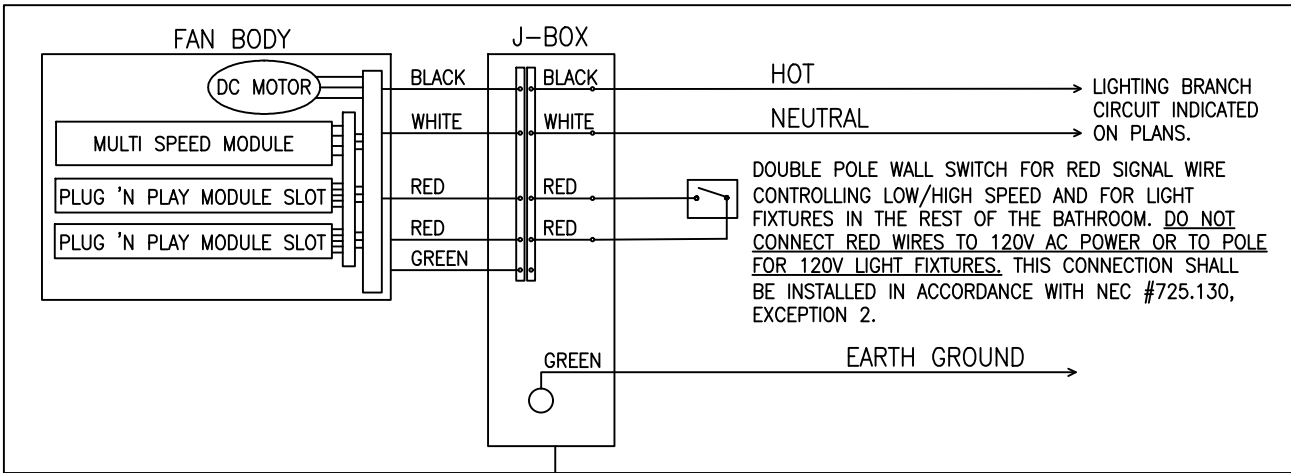

DWELLING UNIT BATHROOM EXHAUST FAN WIRING DIAGRAM
NO SCALE

Seal

NOT FOR
CONSTRUCTION

Issue: Date: By:
SCHEMATIC DESIGN 01.07.26 BAC
DESIGN DEVELOPMENT 03.05.26 BAC

who
engineering
2012 West 25th Street, Suite 900
Cleveland, OH 44113
Phone: 216 227 8505

**OSU
AIRPORT WEST
BUILDING C**







**3455 W. Dublin Granville Rd,
Columbus OH, 43235**


Drawing Title

**TYPICAL DWELLING UNIT
ELECTRICAL DETAILS**


Date 03.05.2026	Project Number 24-065
Drawn By DJS	Drawing Number
Checked by KDS	
Approved gss	

E3.00C

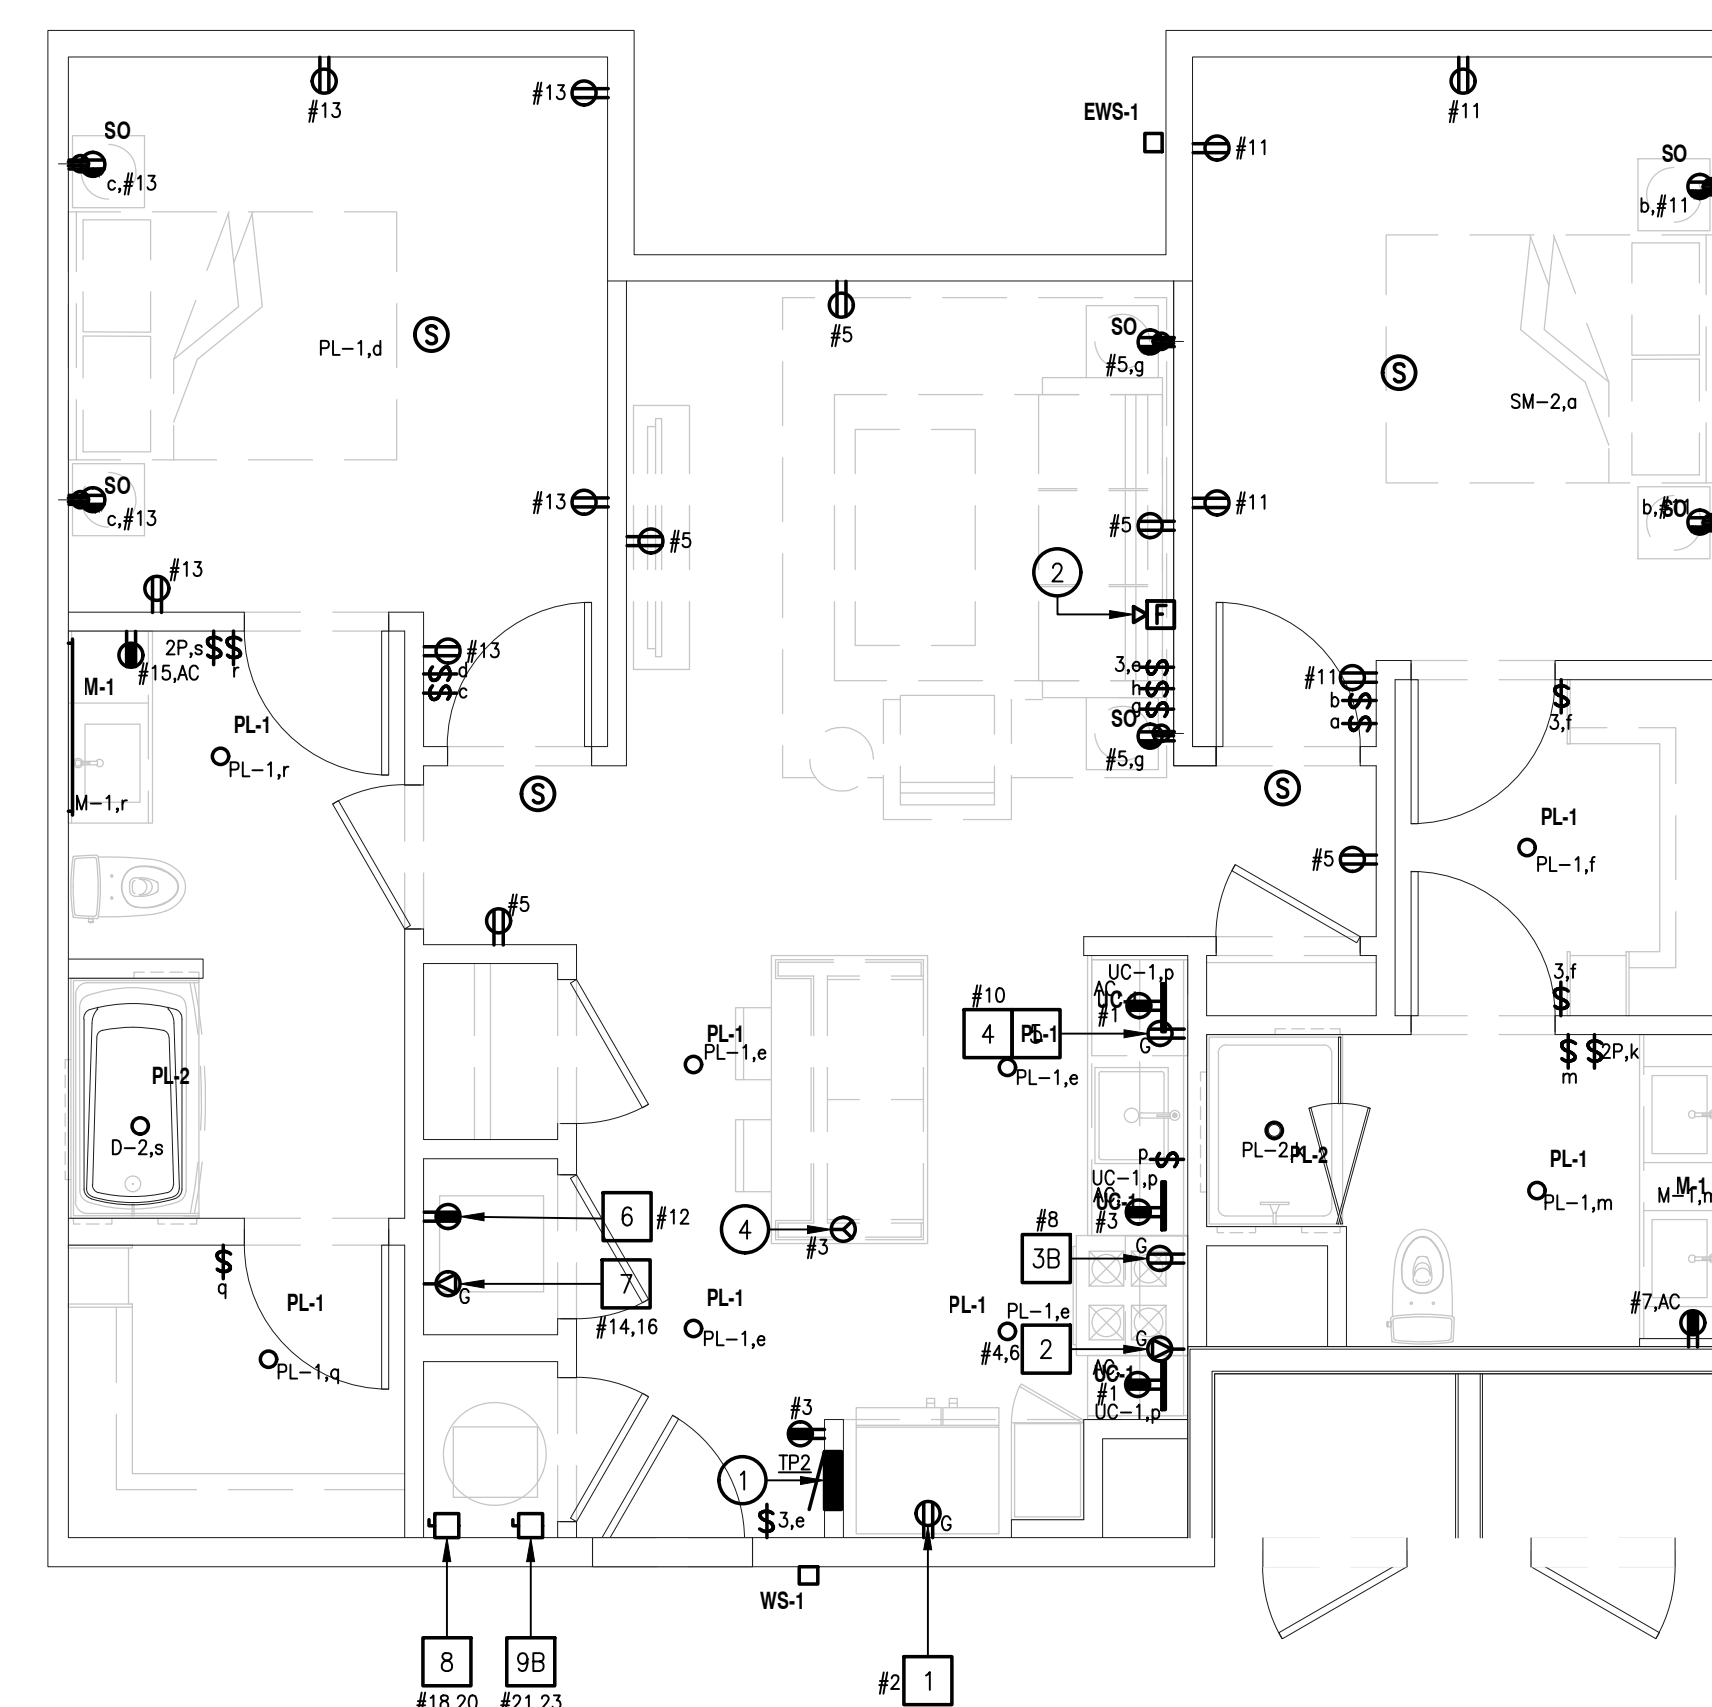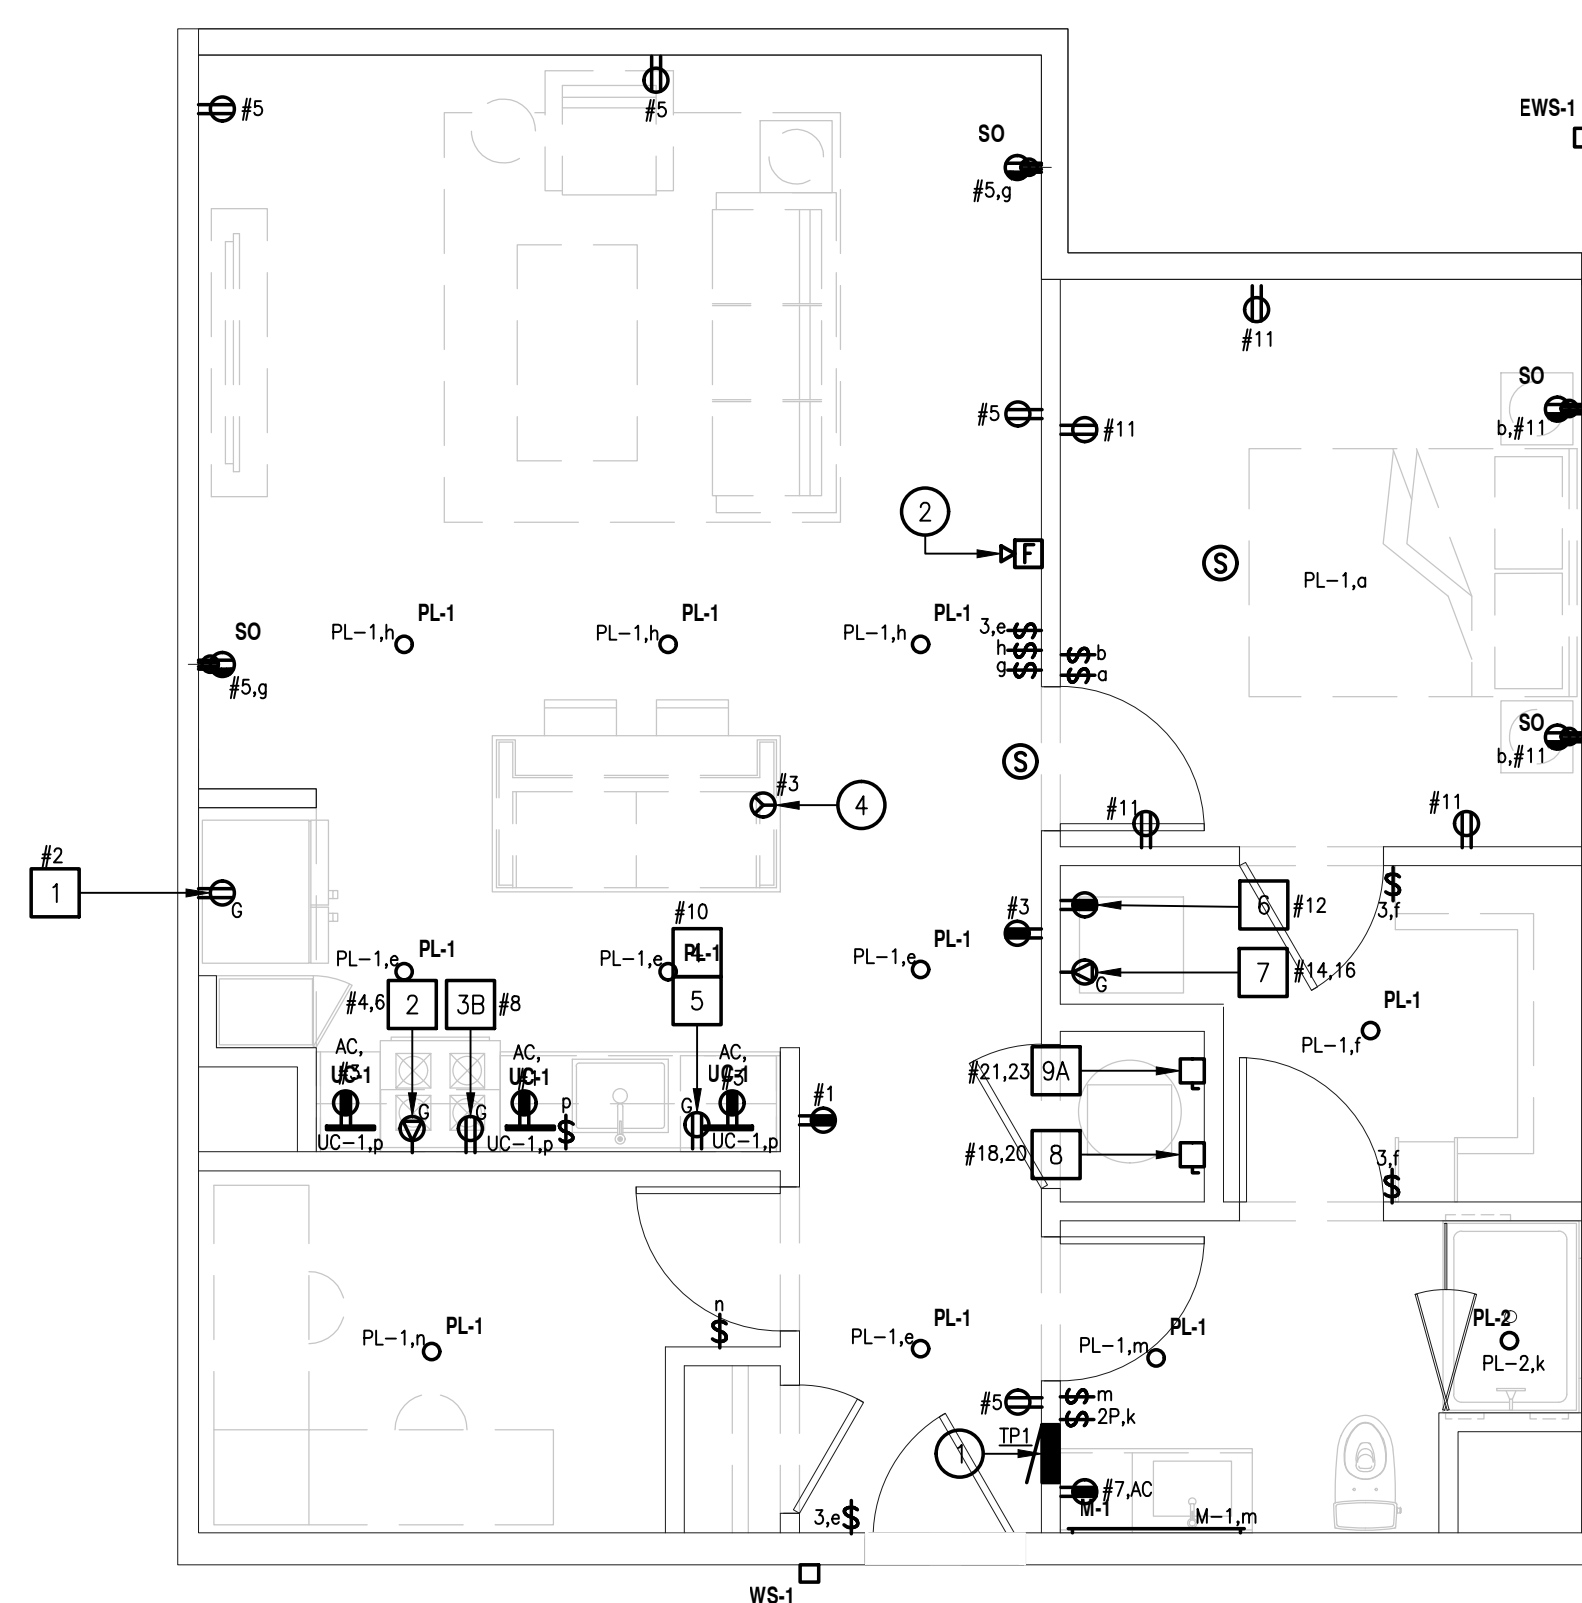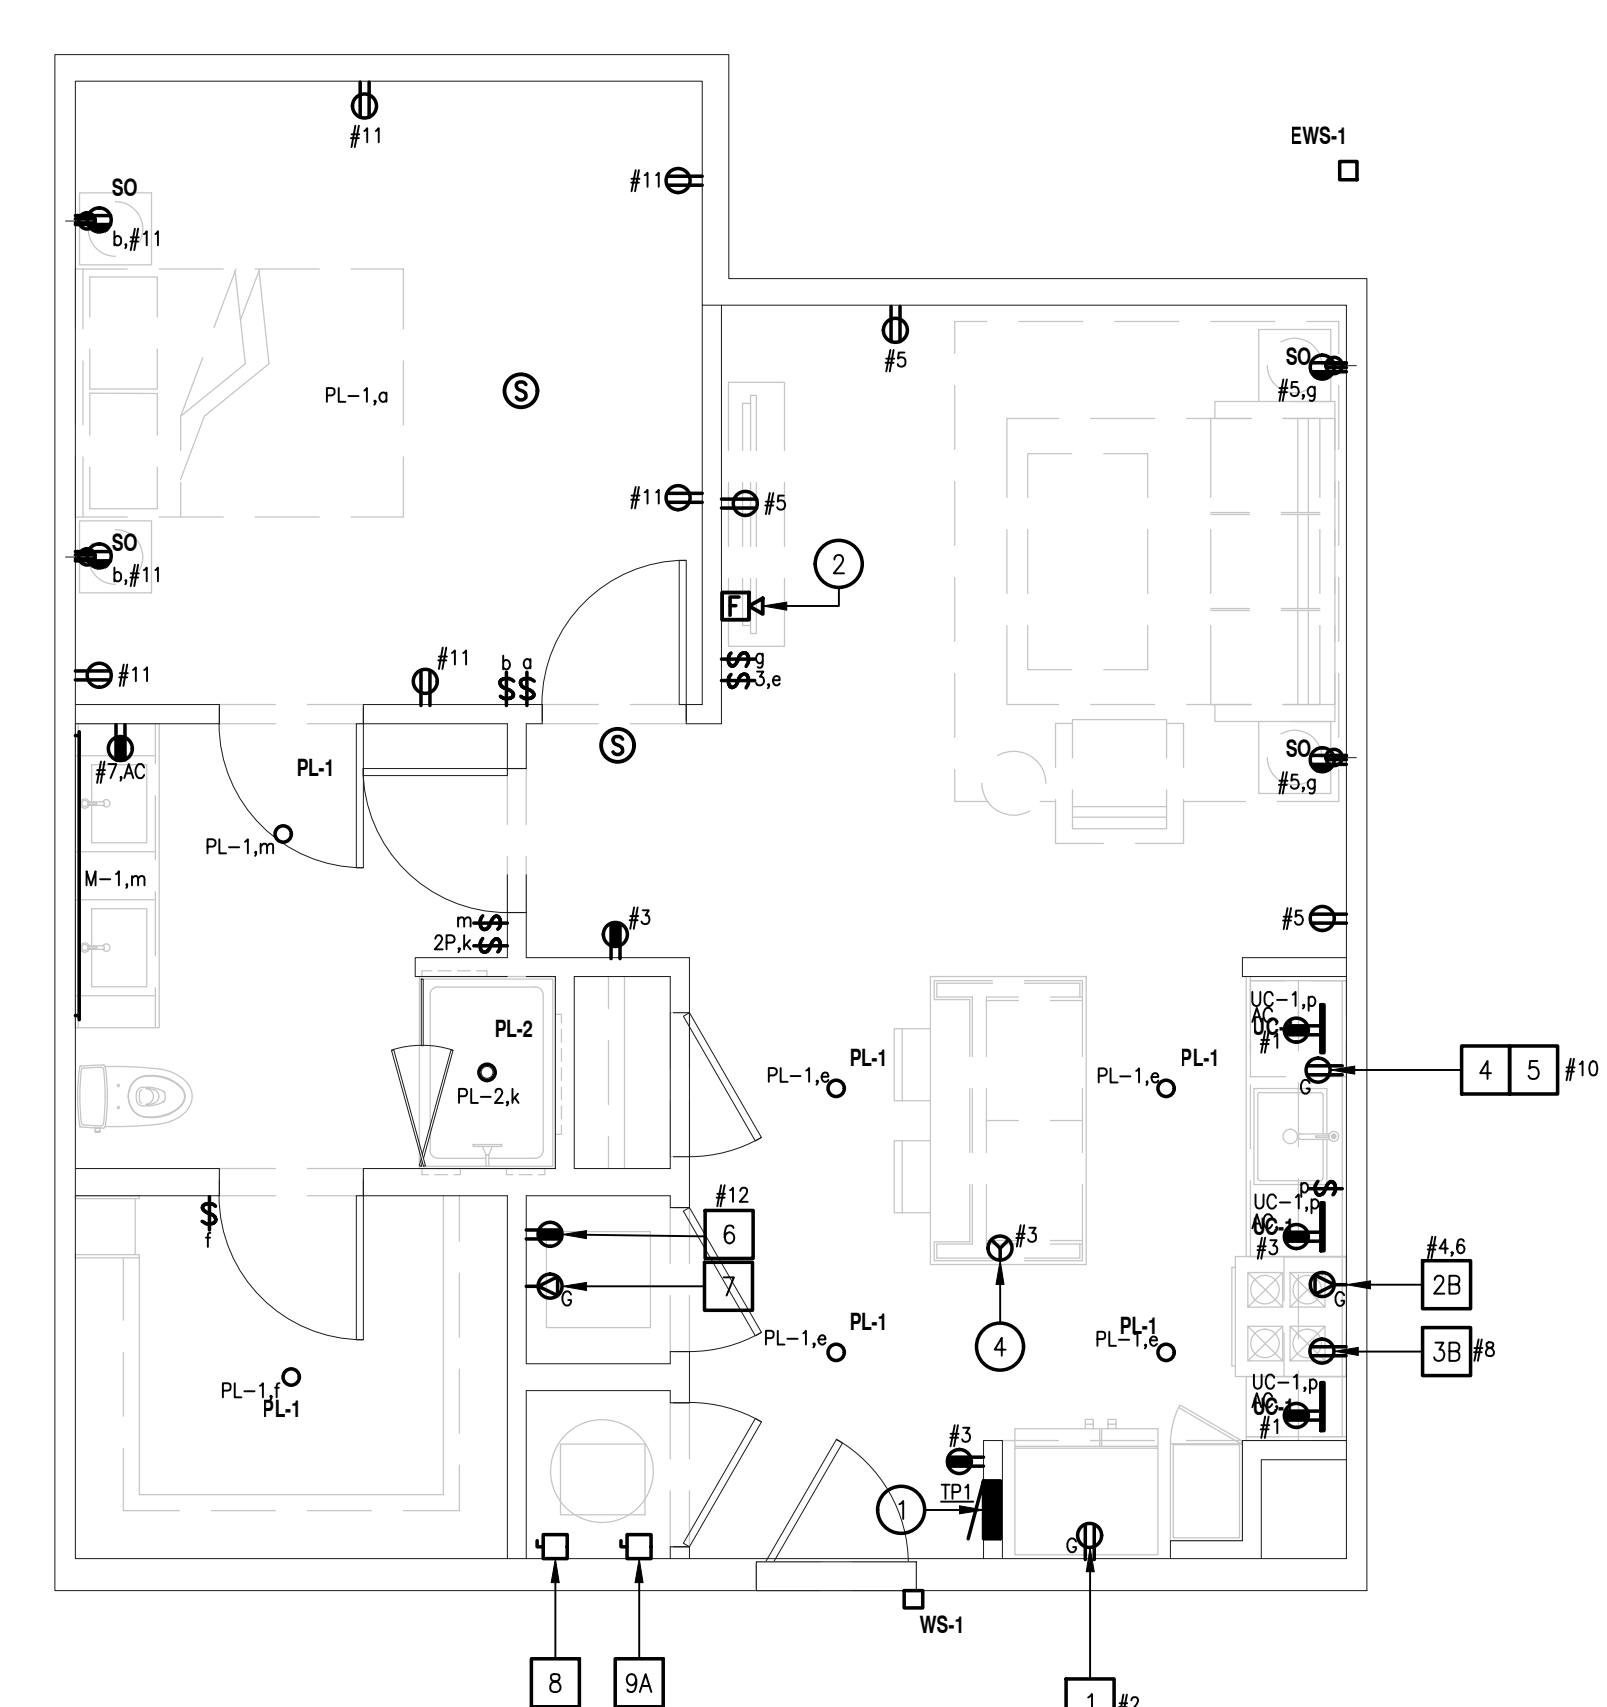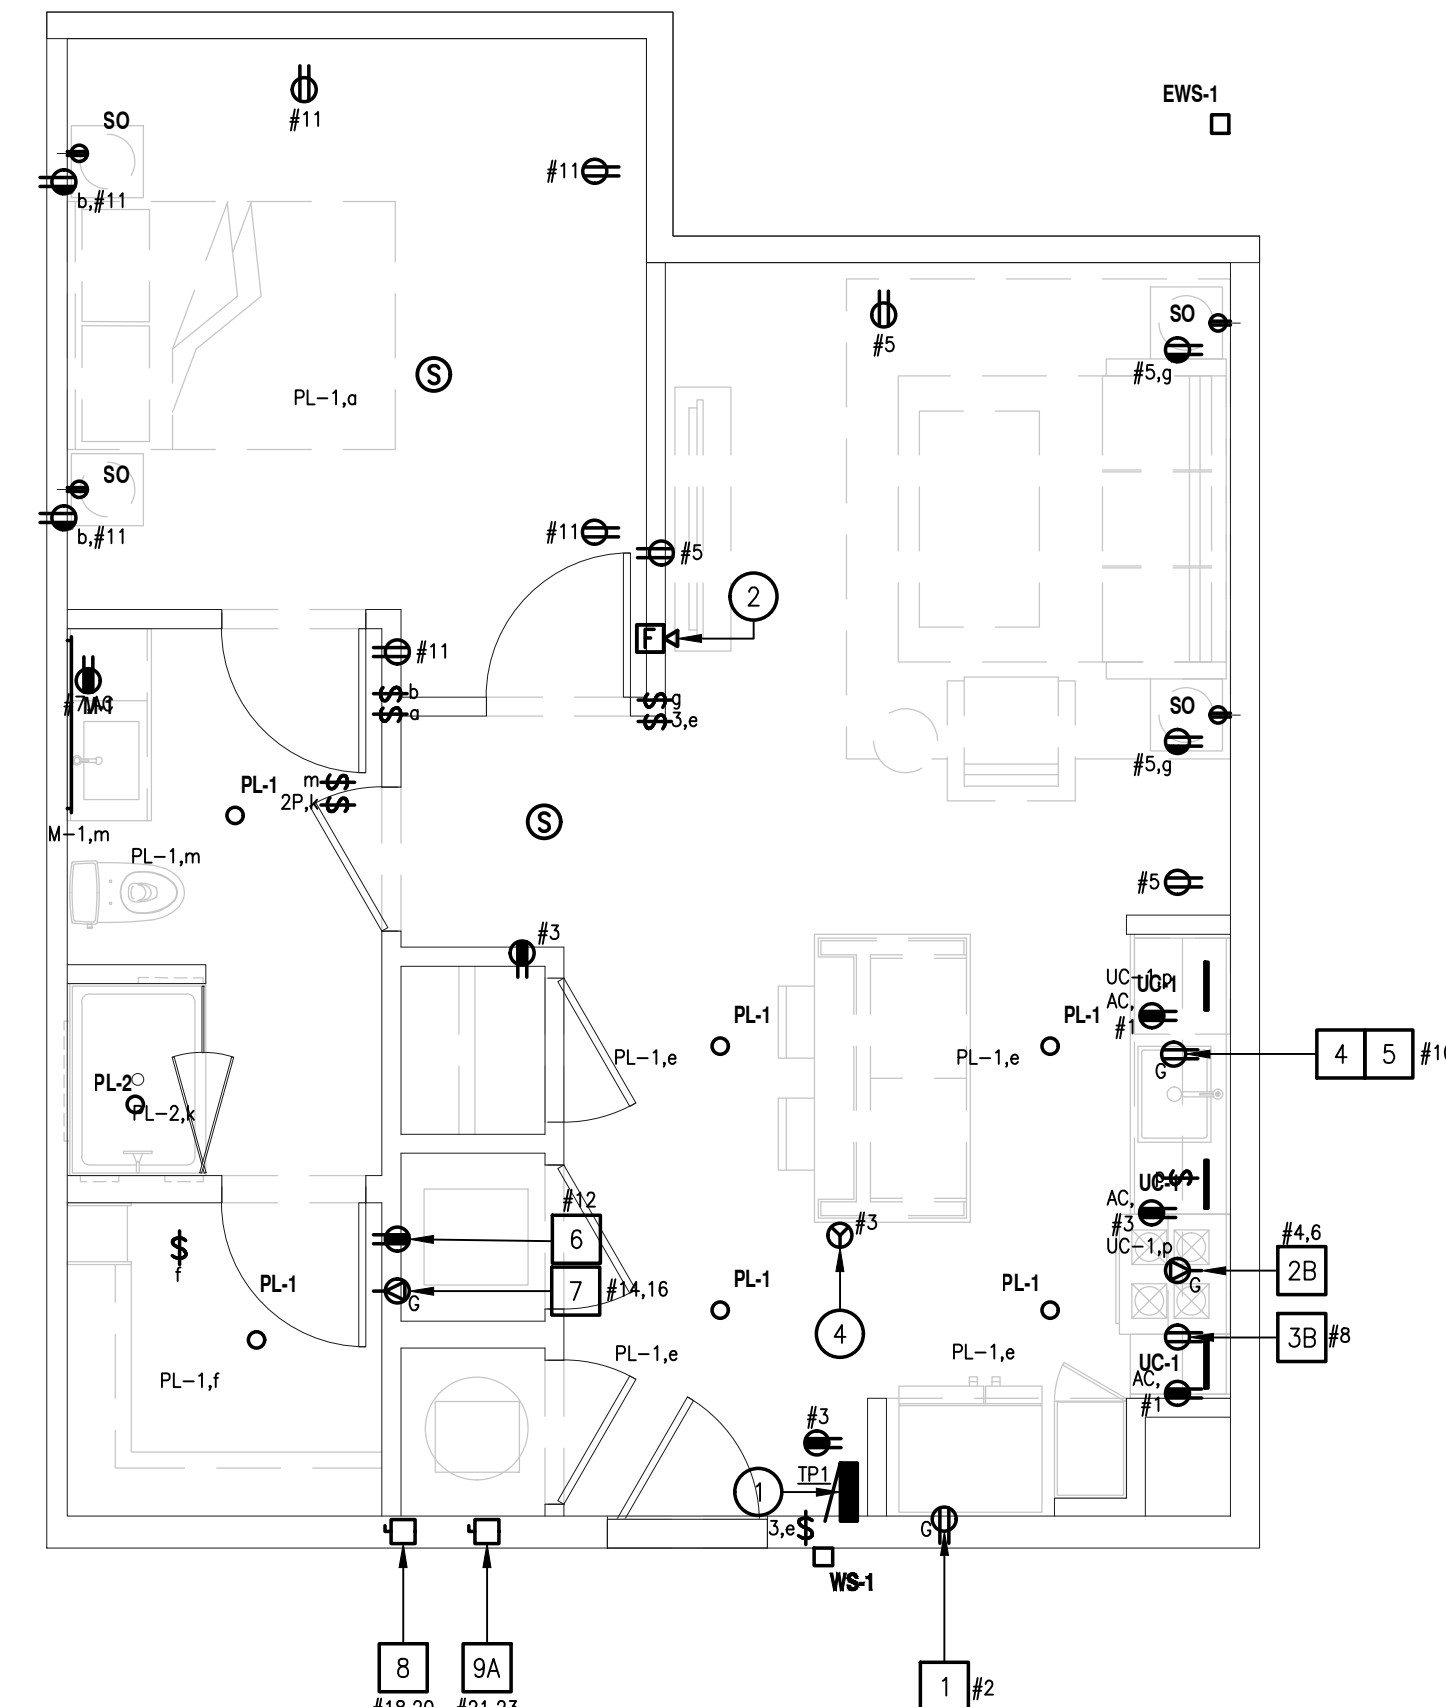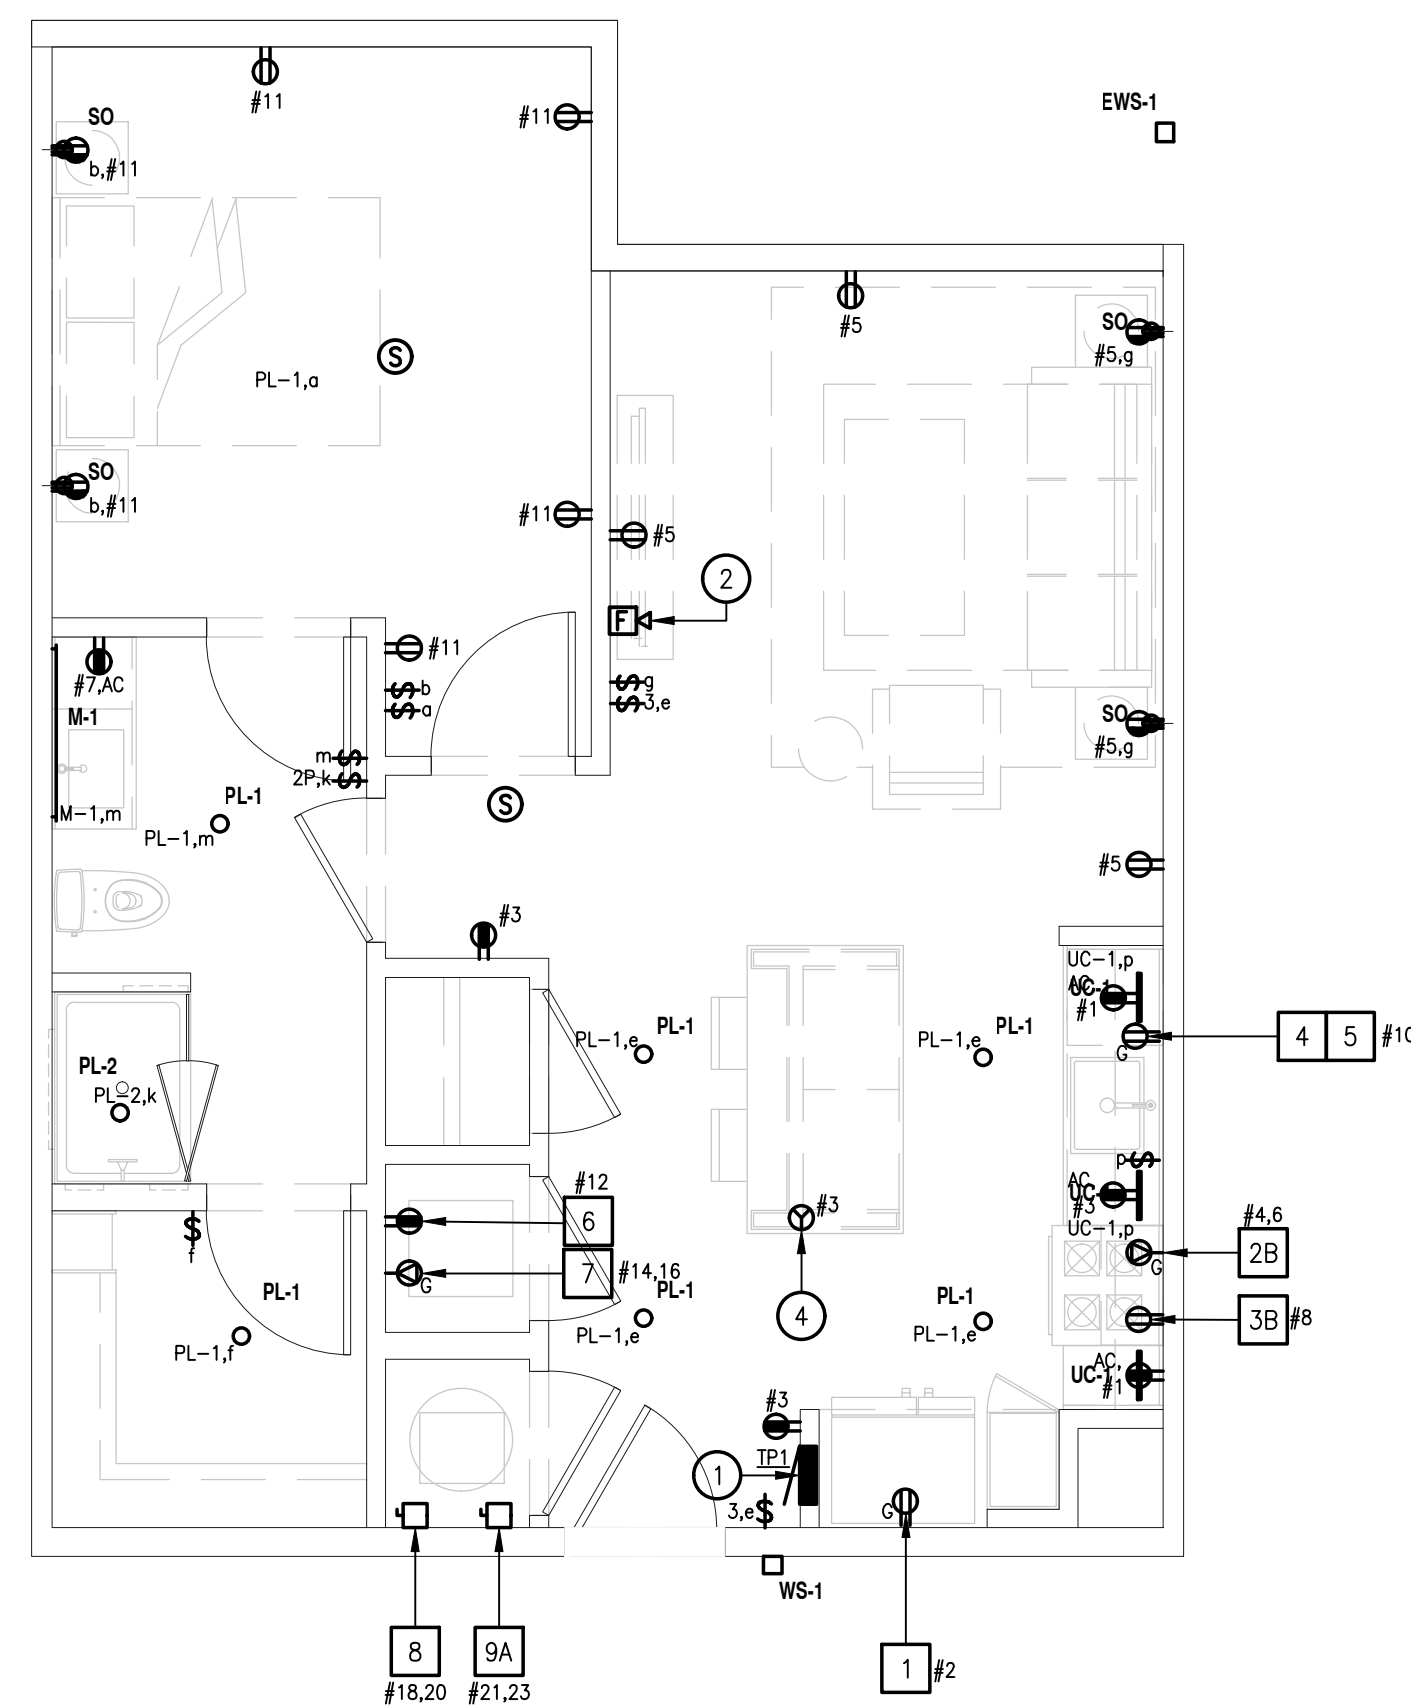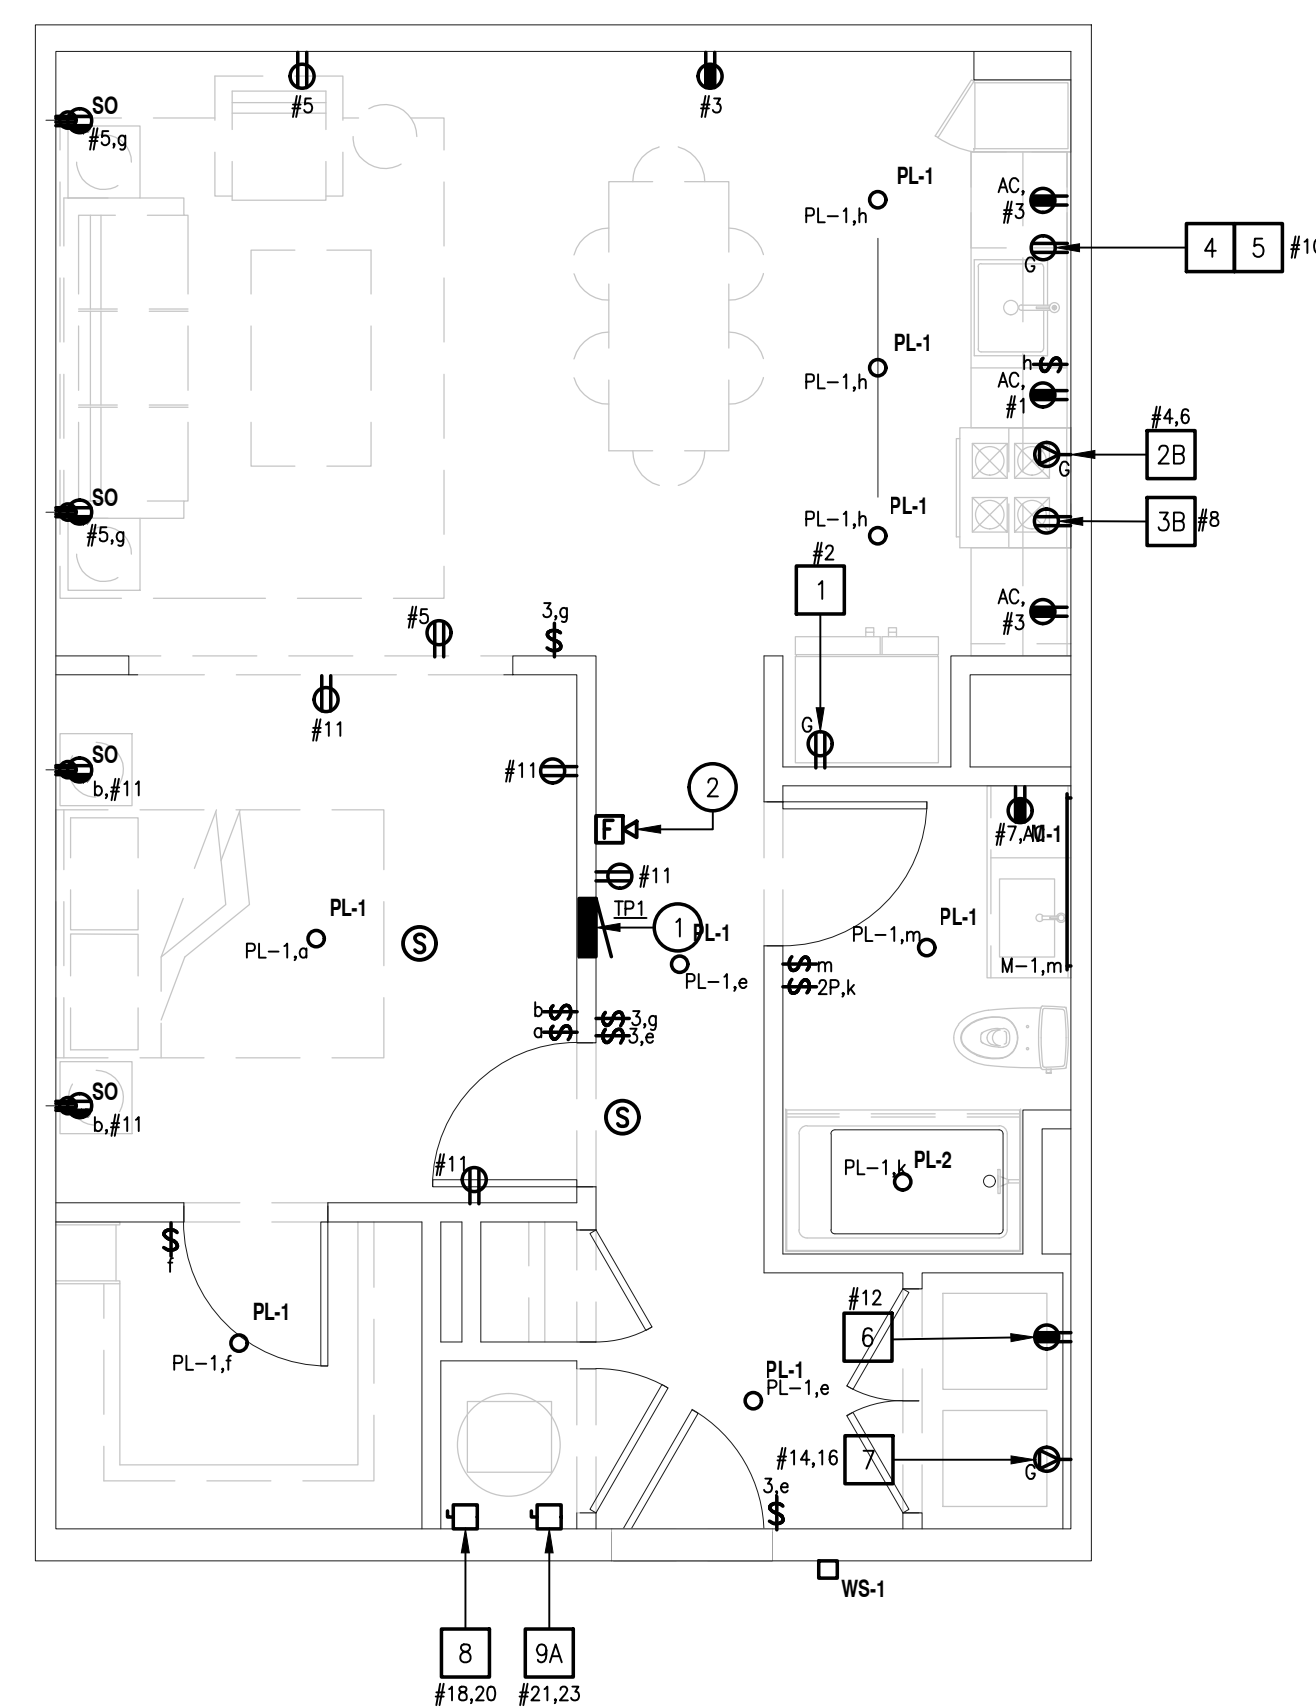


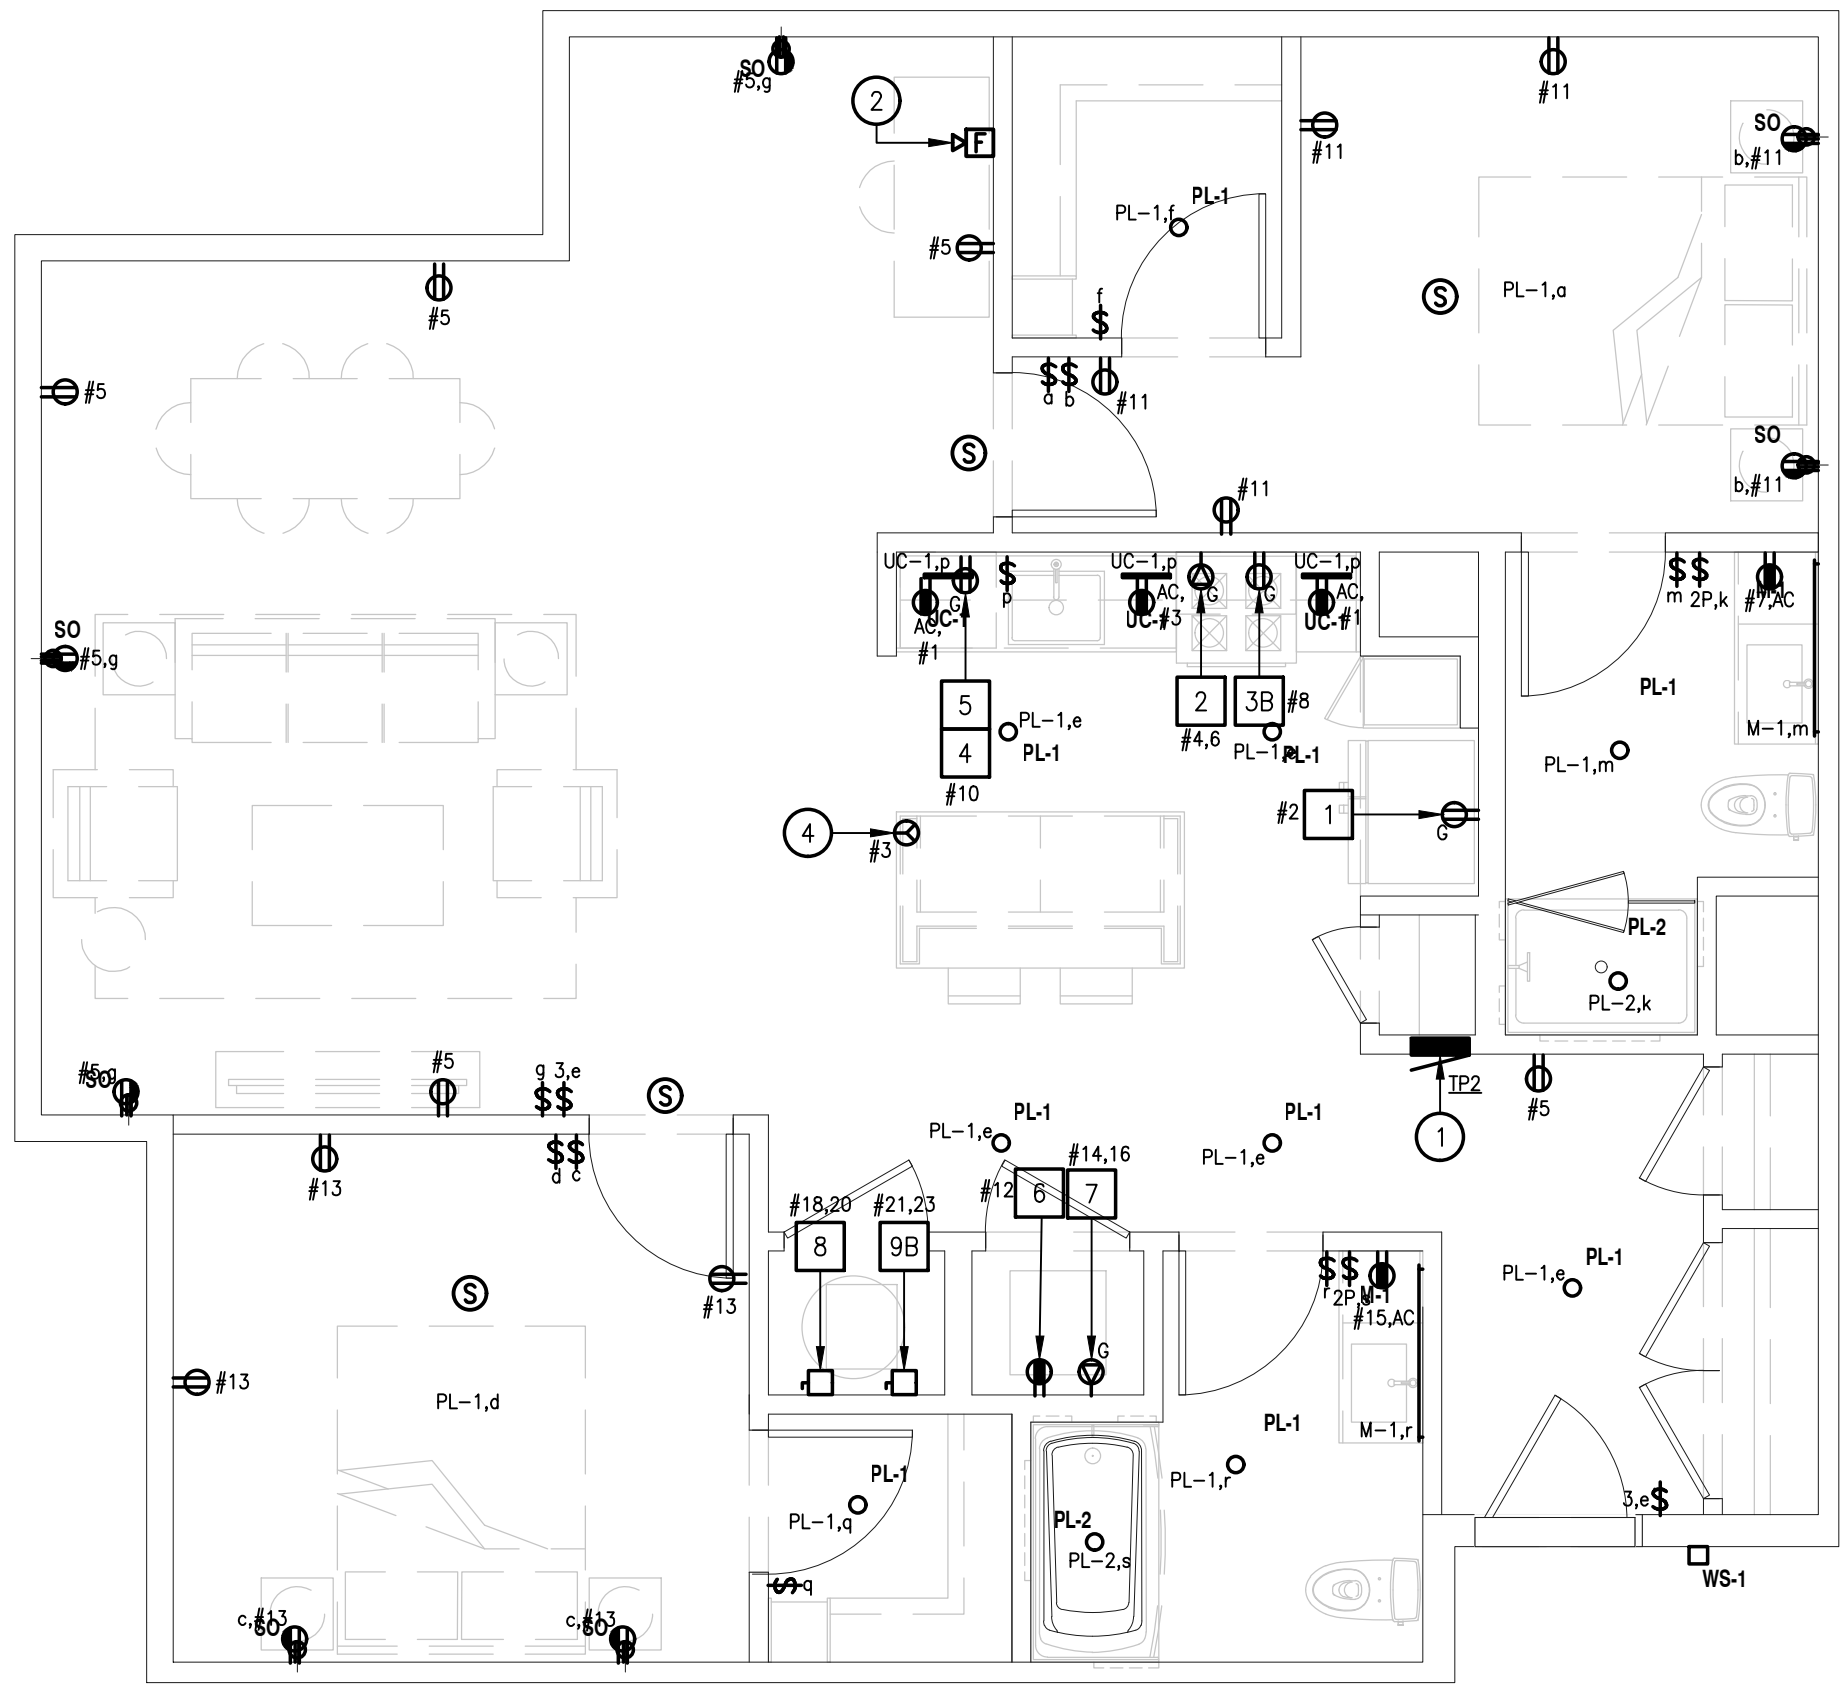


1 BUILDING 2
UNIT TYPE BD1 ELECTRICAL PLAN
A3.02B SCALE: 1/4" = 1'-0"

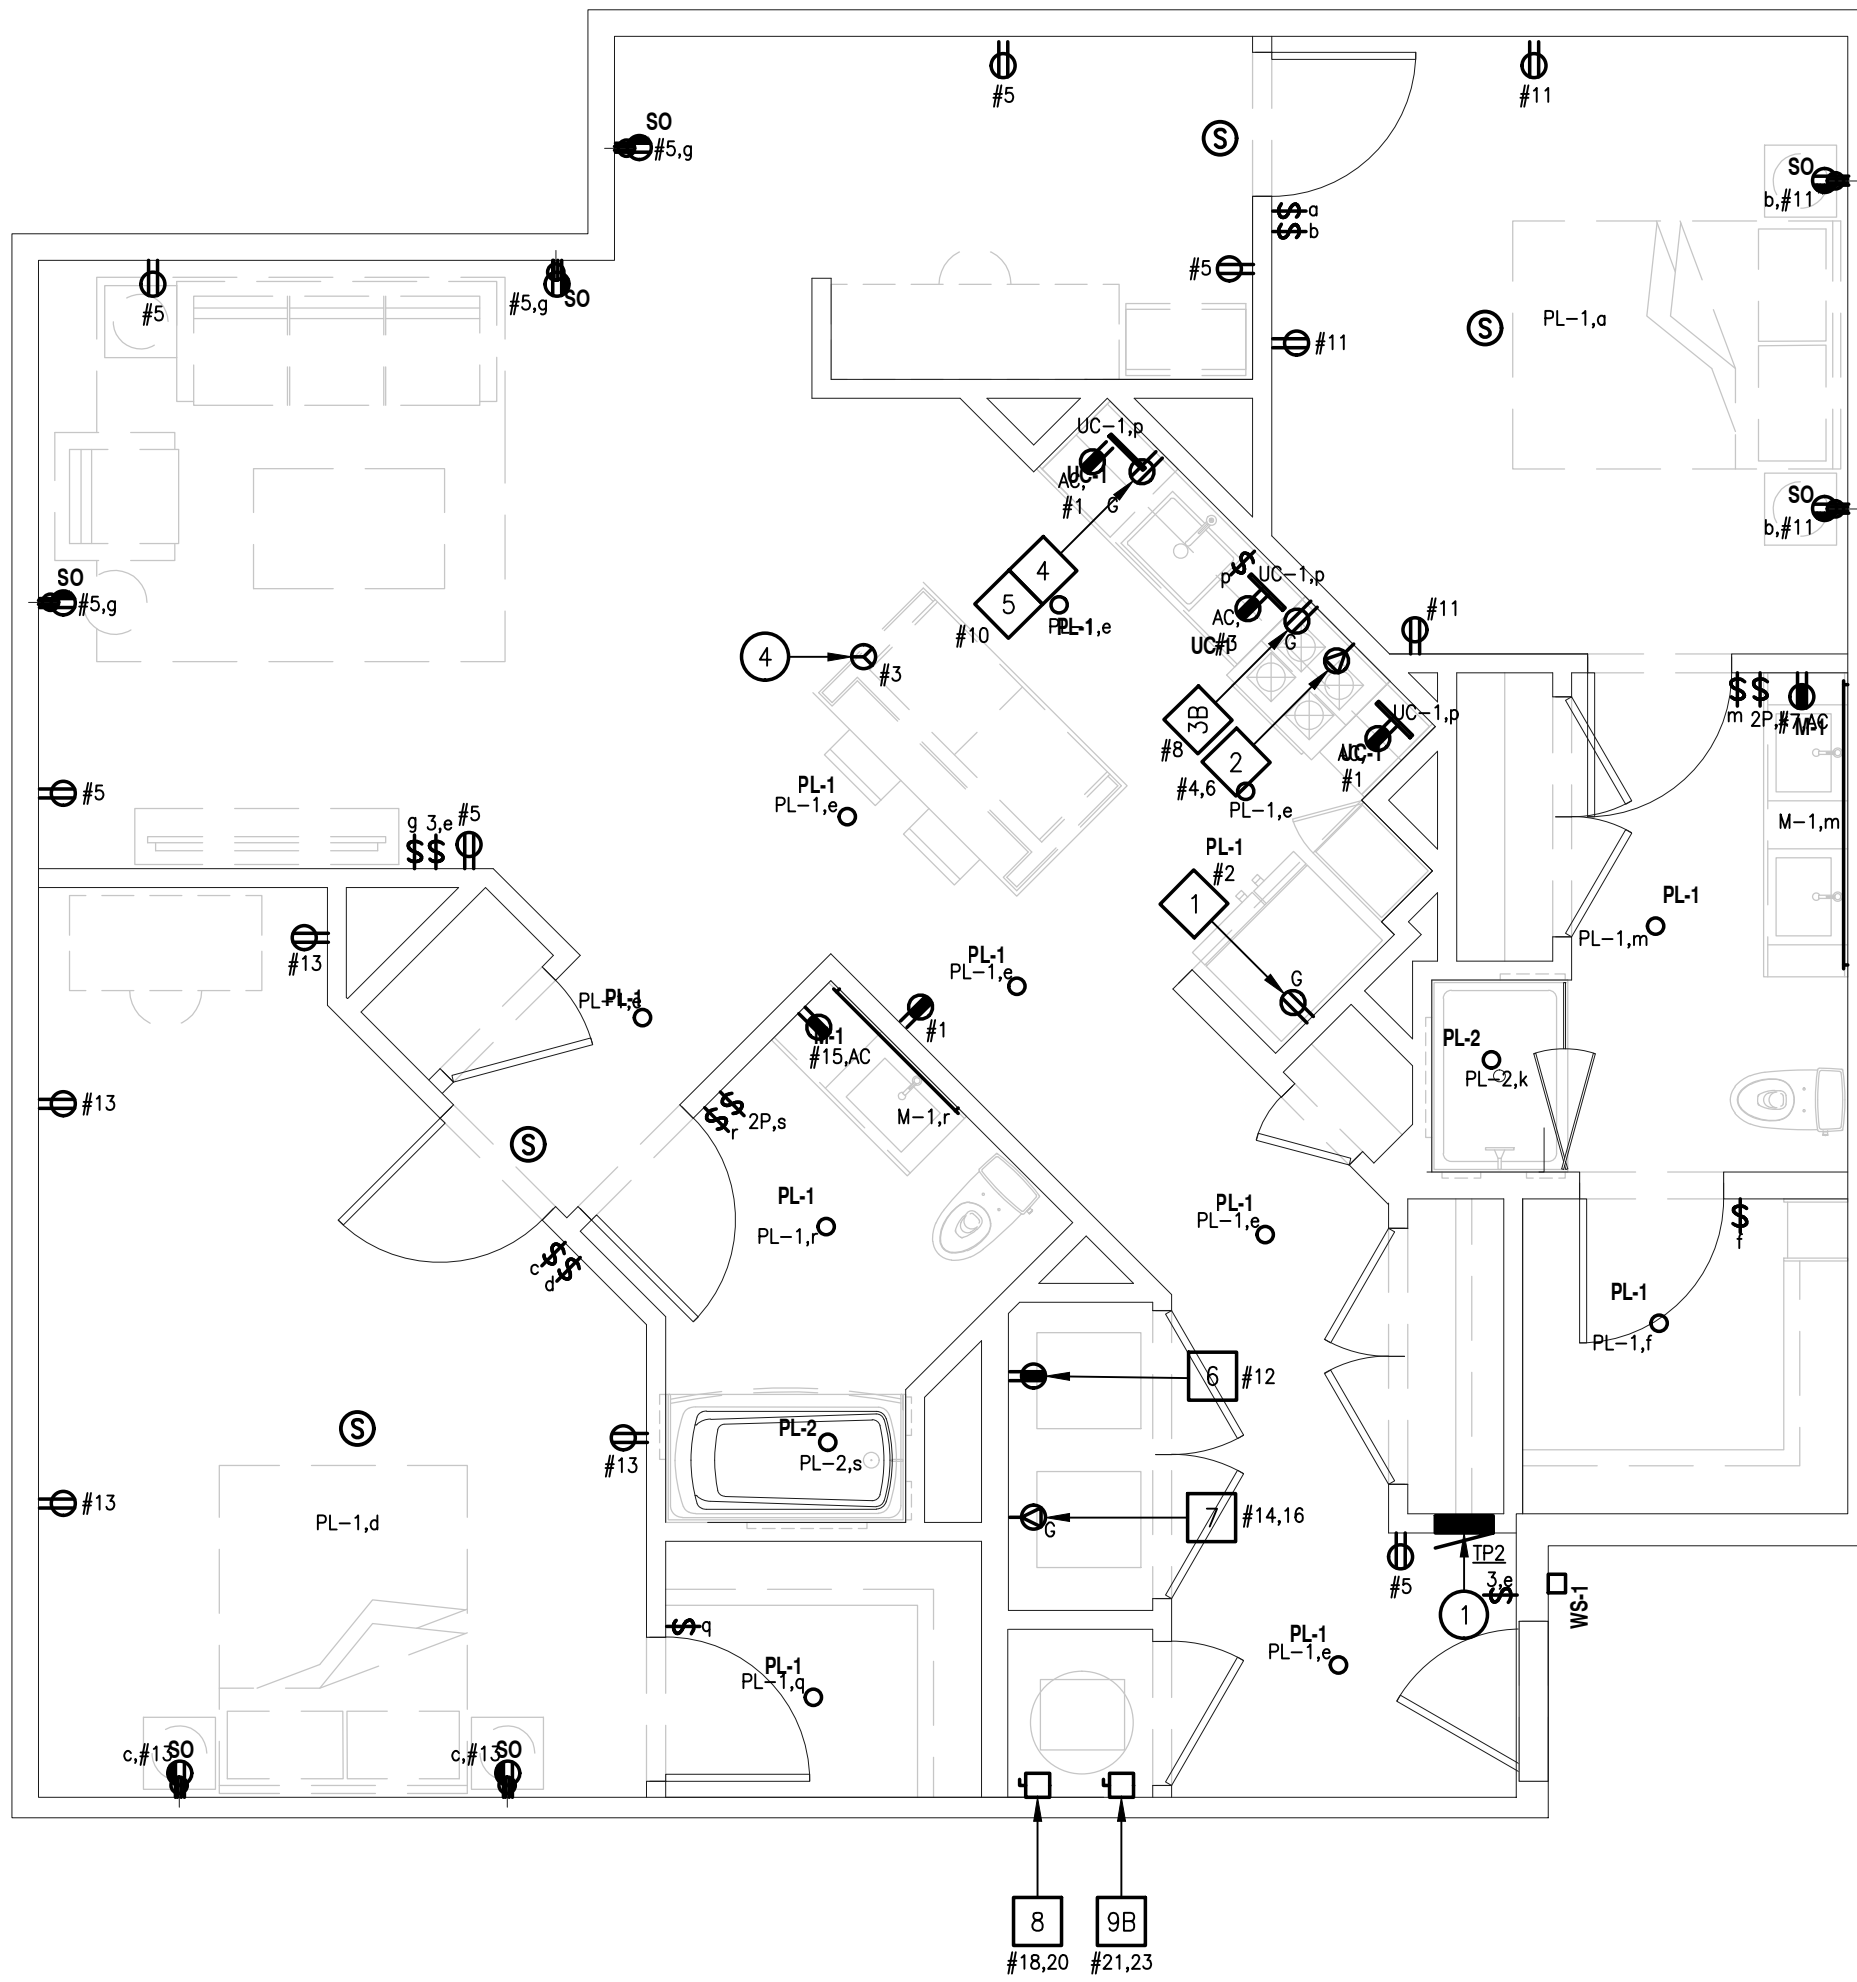


2 BUILDING 2
UNIT TYPE BD3 ELECTRICAL PLAN
A3.02B SCALE: 1/4" = 1'-0"

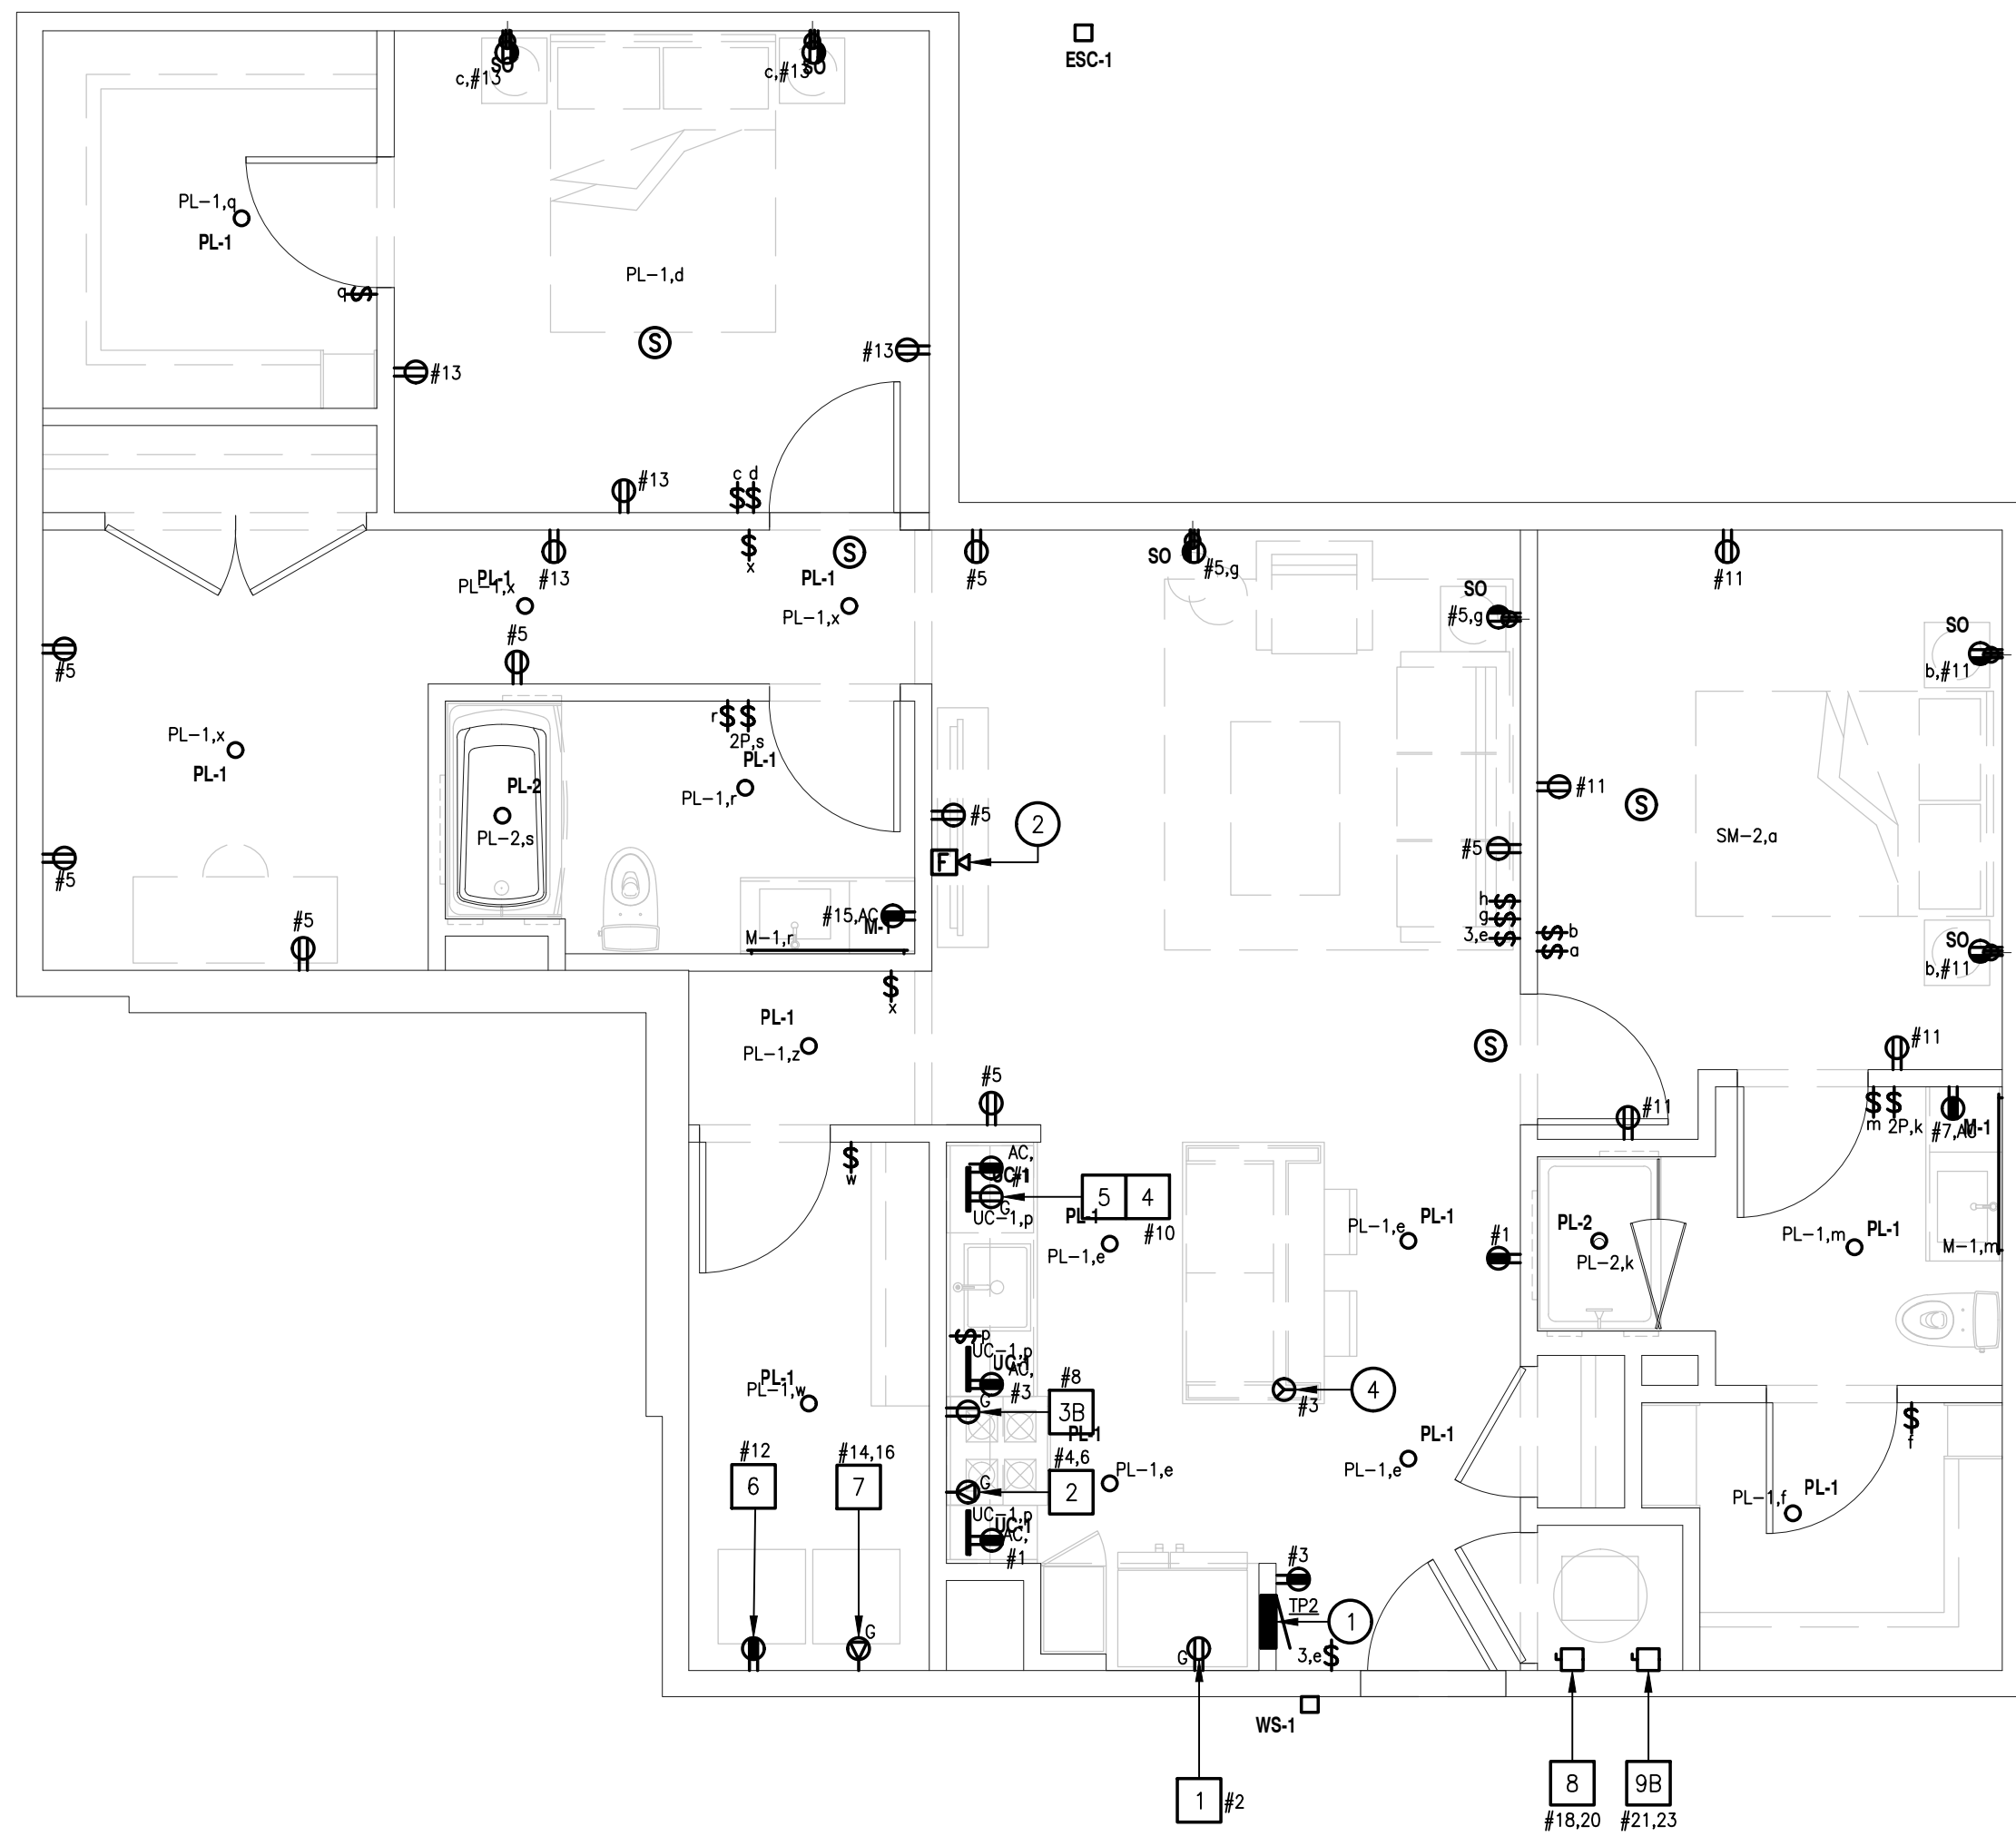

3 BUILDING 2
UNIT TYPE BD3.1 ELECTRICAL PLAN
A3.02B SCALE: 1/4" = 1'-0"

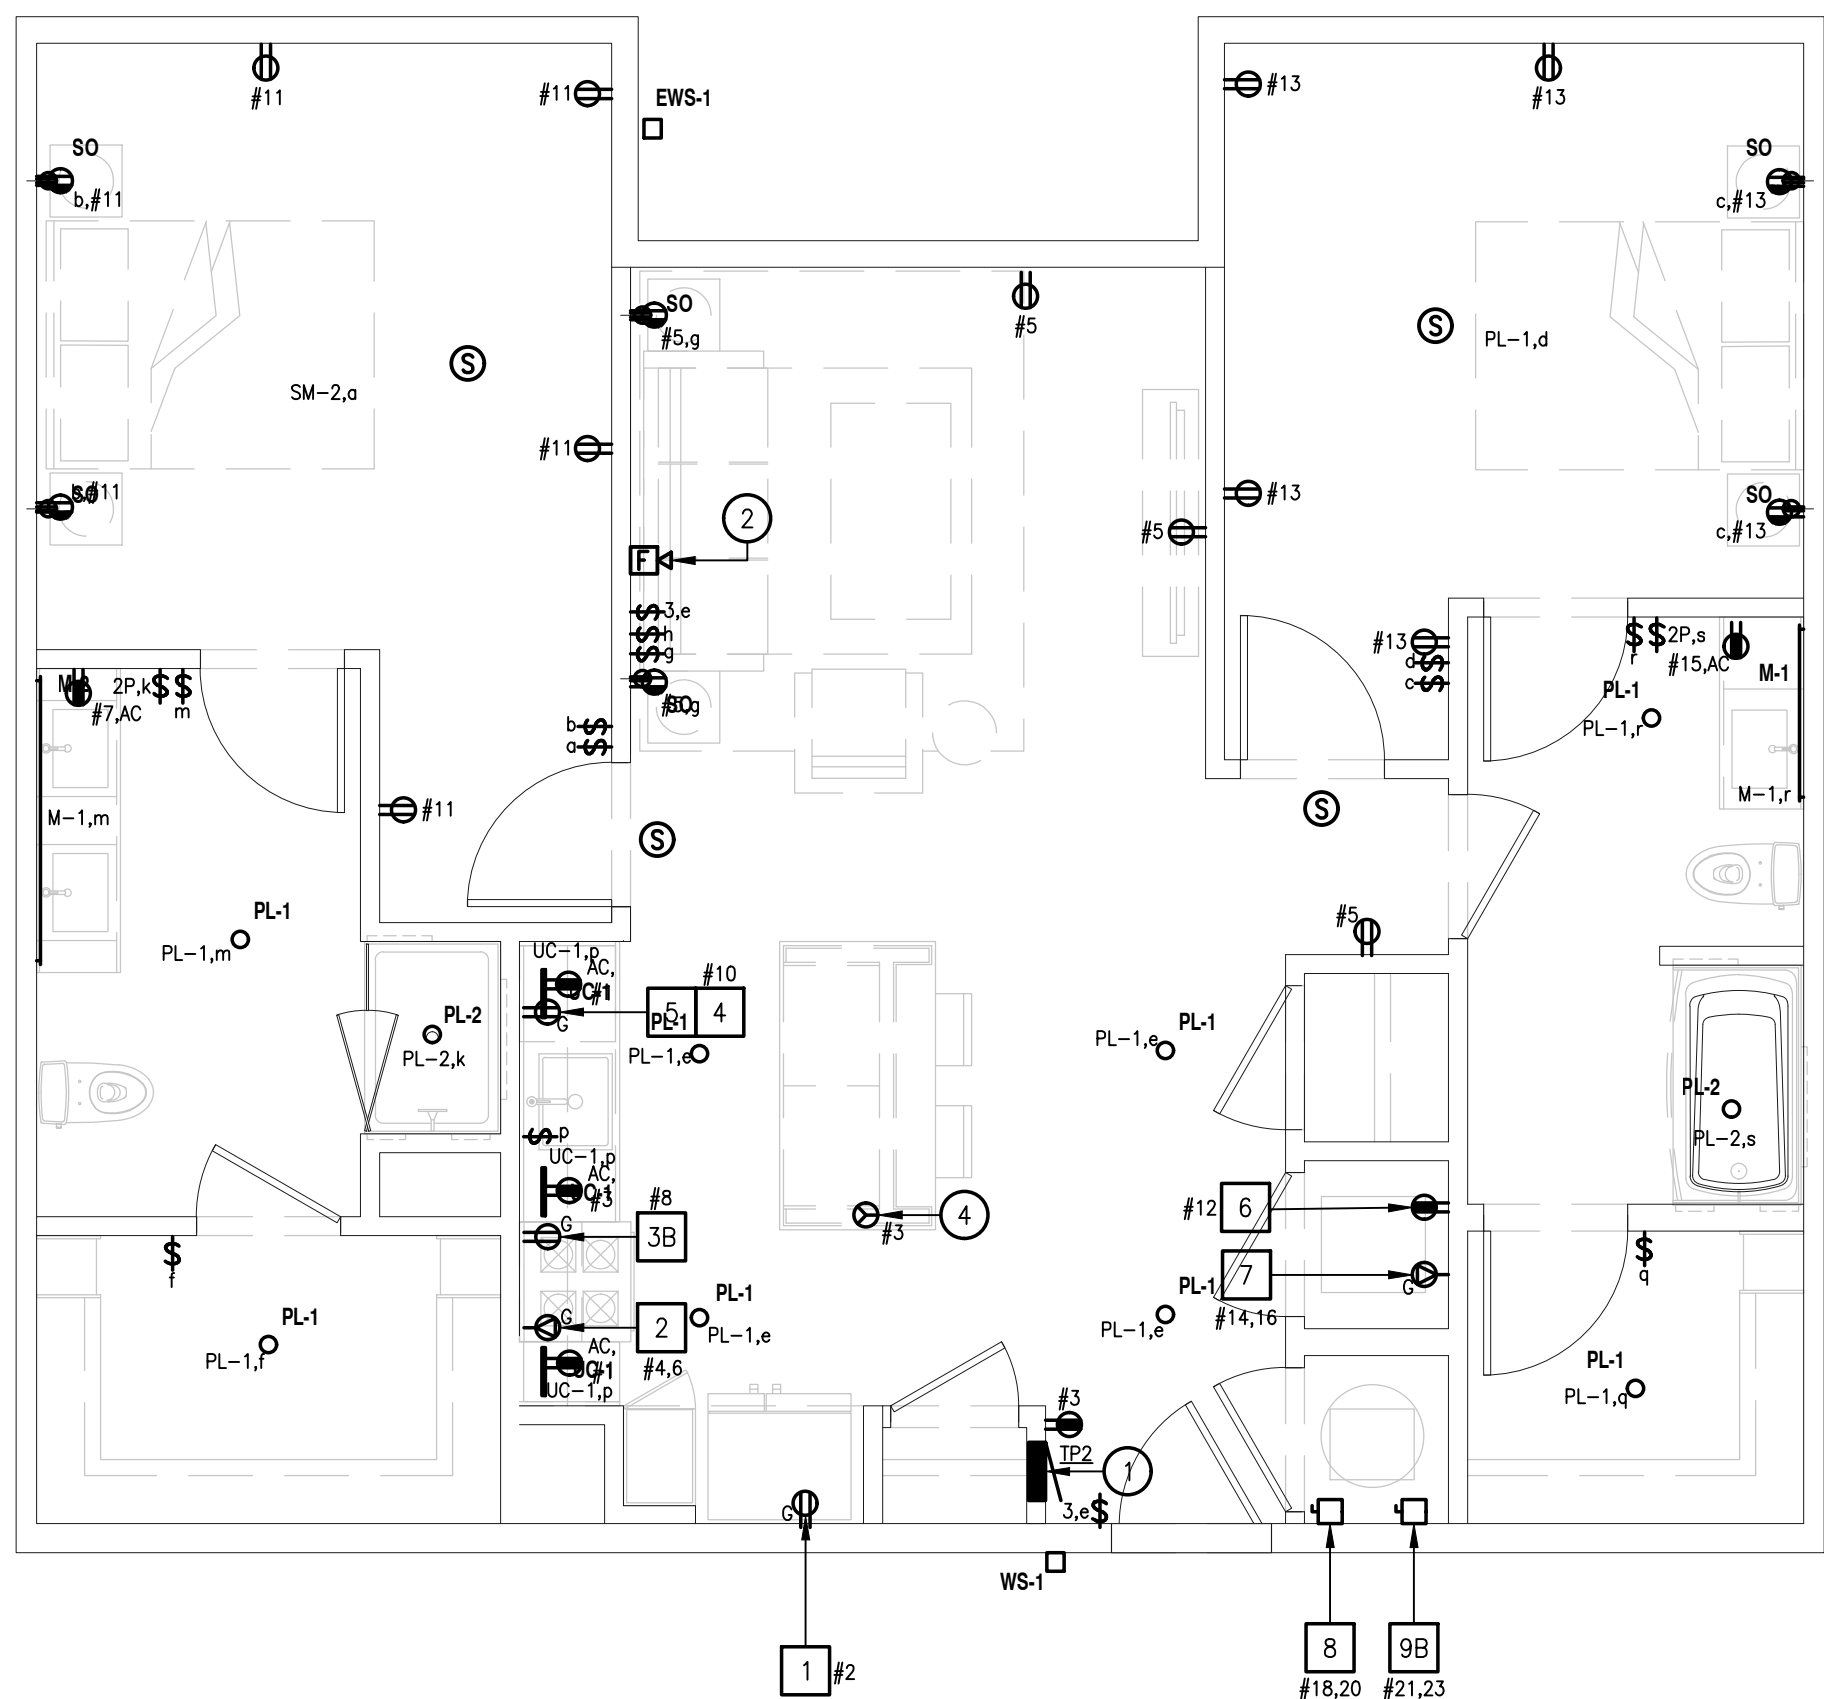

4 BUILDING 2
UNIT TYPE B2 ELECTRICAL PLAN
A3.02B SCALE: 1/4" = 1'-0"

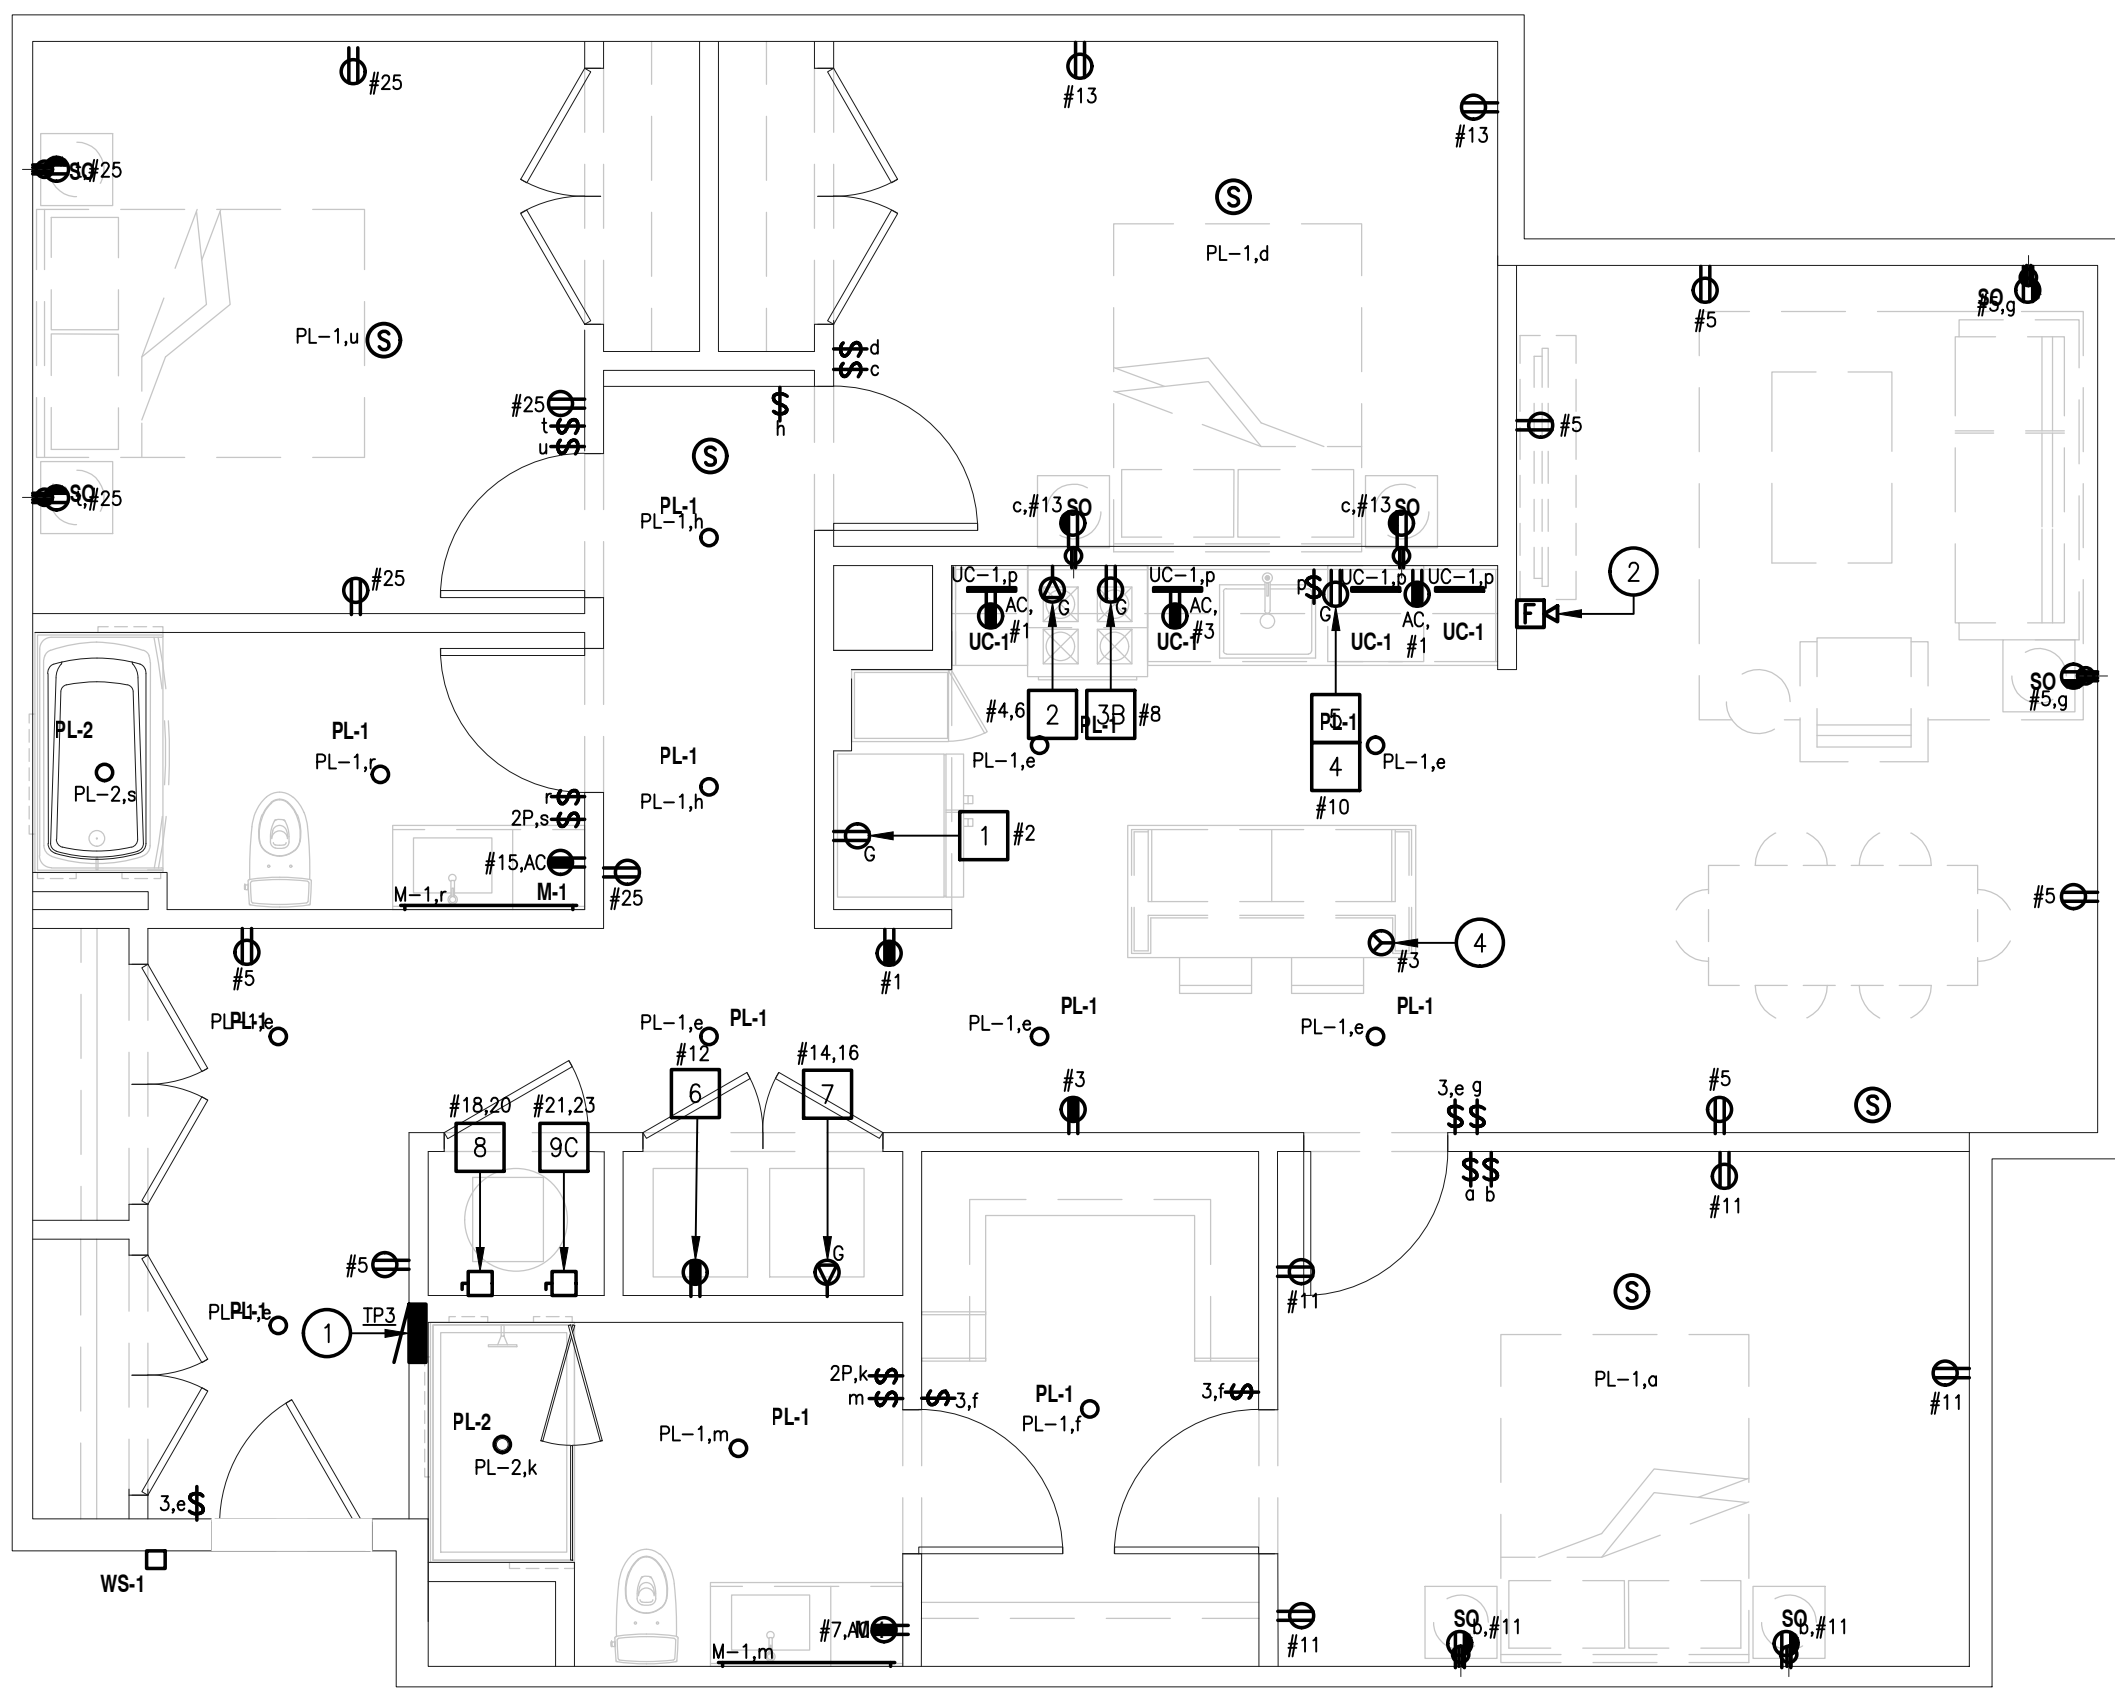

5 BUILDING 2
UNIT TYPE C2 ELECTRICAL PLAN
A3.02B SCALE: 1/4" = 1'-0"

- GENERAL DWELLING UNIT ELECTRICAL PLAN NOTES
- ALL LIGHT FIXTURES, CEILING FANS, AND BATHROOM/KITCHEN EXHAUST FANS SHALL BE CONNECTED TO CIRCUIT #9 IN RESPECTIVE UNIT LOAD CENTER UNLESS SHOWN OTHERWISE.
 - REFER TO SHEET #E3-00 FOR ALL UNIT DETAILS, INCLUDING APPLIANCE SCHEDULES.
 - FLOOR RECEPTACLES MAY BE INSTALLED IN LIEU OF WALL RECEPTACLES SHOULD WINDOWS/GLAZING OR SLIDING DOOR RECESSED POCKETS INTERFERE WITH WALL MOUNTING AT ANY LOCATION WITHIN THE DWELLING UNIT. FLOOR RECEPTACLES SHALL BE INSTALLED WITHIN 18" OF WINDOWS/WALLS OR PER NEC #210.52(A)(3).

- CODED NOTES
- LOCATION OF NEW TENANT CIRCUIT BREAKER LOAD CENTER. REFER TO TYPICAL UNIT CIRCUIT BREAKER PANEL SCHEDULE ON SHEET #E3-00 FOR ADDITIONAL INFORMATION. ALL LIVING AREA BRANCH CIRCUITS SHALL BE PROVIDED WITH ARC-FAULT CIRCUIT INTERRUPTER PROTECTION IN ACCORDANCE WITH N.E.C. ARTICLE #210.12(A).
 - THIS FIRE ALARM DEVICE SHALL BE CONNECTED TO THE BASE BUILDING FIRE ALARM SYSTEM. VERIFY FINAL LOCATION WITH A.H.J. AND FIRE MARSHAL.
 - LOCATION OF STRUCTURED MEDIA ENCLOSURE "SME". REFER TO DETAIL ON DRAWING #E3-00 FOR ADDITIONAL INFORMATION. PROVIDE POWER FROM NEAREST LIVING AREA BRANCH CIRCUIT.
 - COORDINATE FINAL LOCATION OF JUNCTION BOX FOR FUTURE KITCHEN COUNTER RECEPTACLE WITH G.C. AND OWNERSHIP. ROUTE AN EMPTY 1" C. WITH PULLWIRE TO NEAREST SMALL APPLIANCE BRANCH CIRCUIT (#1 OR #3) FOR FUTURE WIRING. THE FINAL INSTALLATION SHALL BE IN COMPLIANCE WITH NEC SECTION 210.52(C)(3).

Seal

NOT FOR
CONSTRUCTION

Issue: Date: By:
SCHEMATIC DESIGN 01.07.26 BAC
DESIGN DEVELOPMENT 03.05.26 BAC

who
engineering
2012 West 25th Street, Suite 900
Cleveland, OH 44113
Phone: 216 227 8505

**OSU
AIRPORT WEST
BUILDING C**

**3455 W. Dublin Granville Rd,
Columbus OH, 43235**

Drawing Title
**TYPICAL DWELLING UNIT
ELECTRICAL PLANS**

Date: 03.05.2026	Project Number: 24-065
Drawn By: DJS	Checking By: KDS
Approved: GSS	

E3.02C